
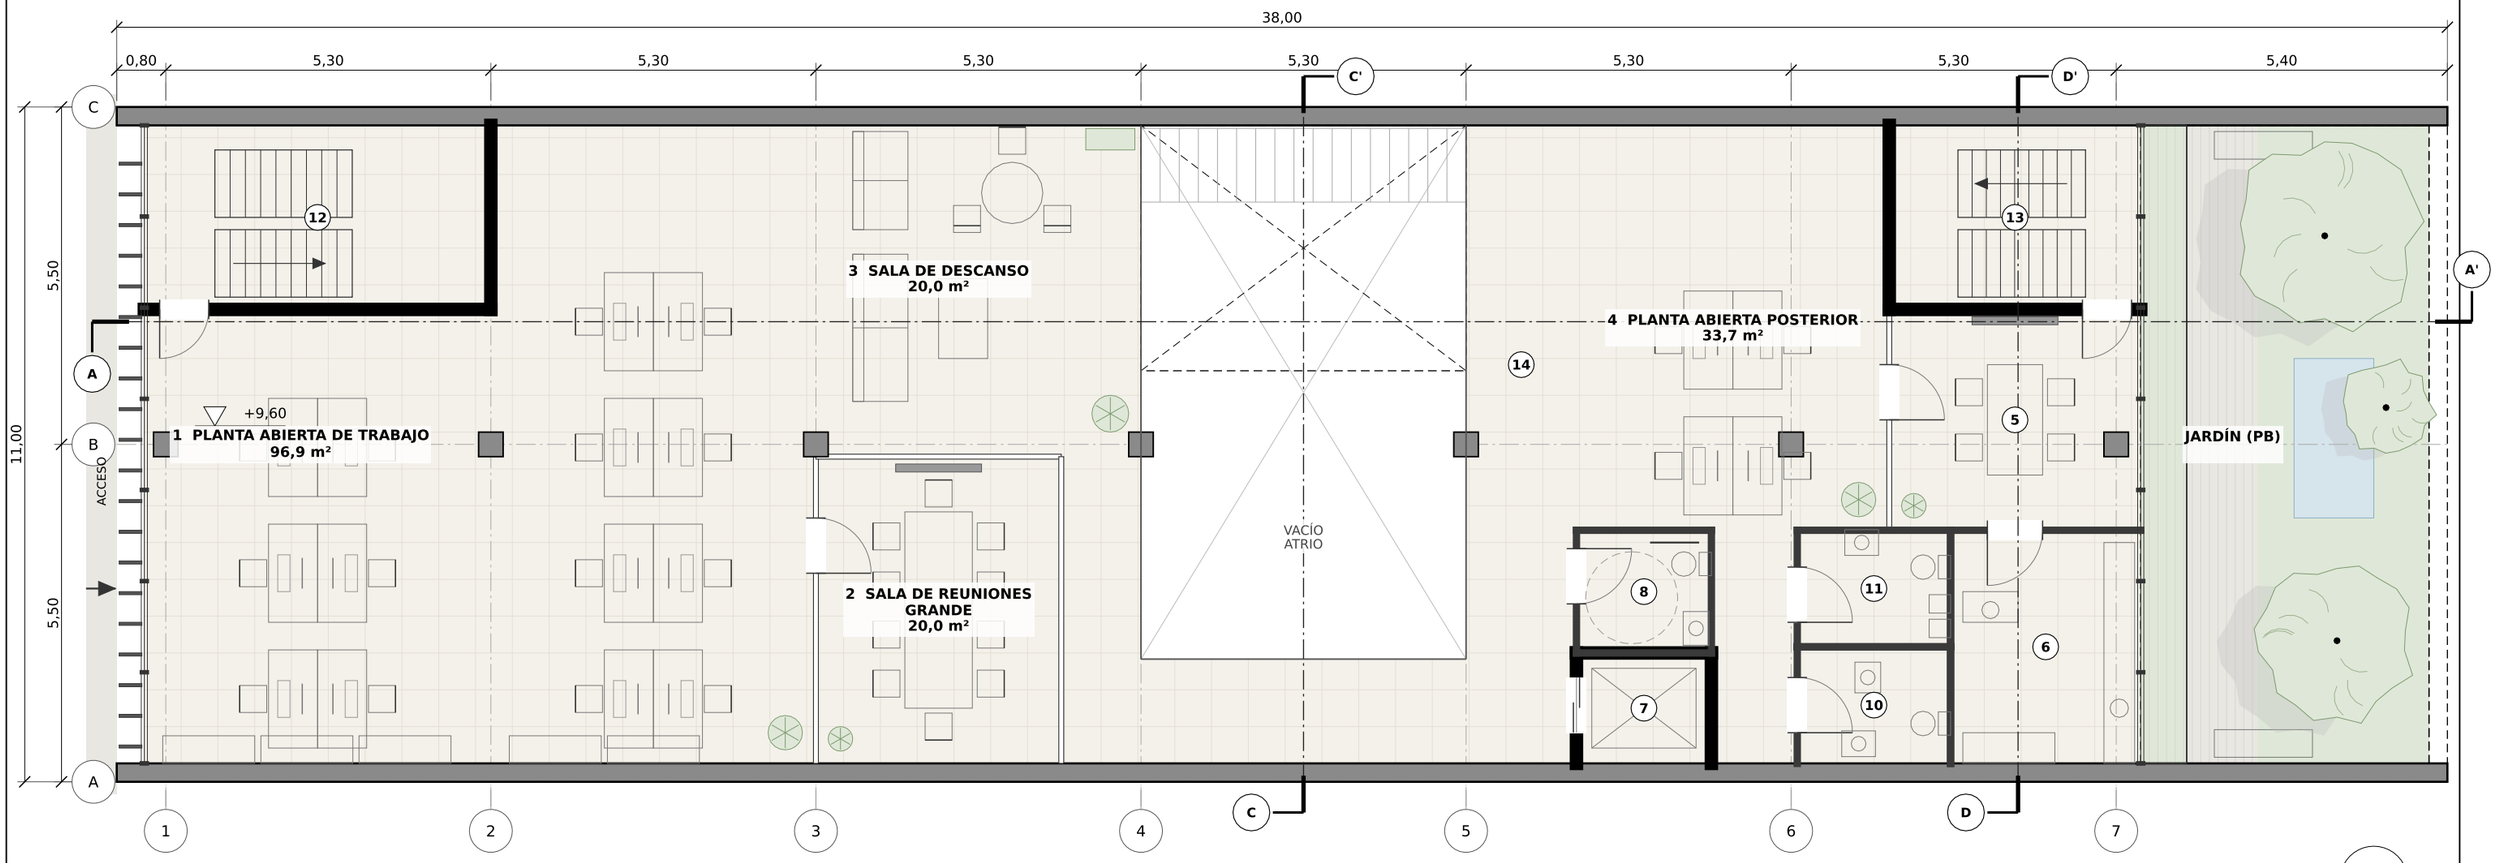


PLANTA TERCERA

E 1:100

0 1 2 5 10 m

ESQUEMA DE ACCESIBILIDAD Y EVACUACIÓN · E 1:200

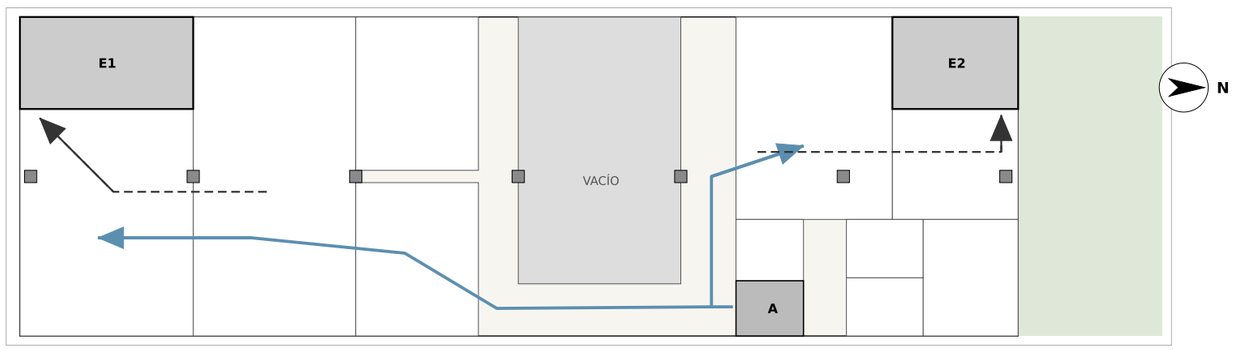

LEYENDA

- Existente que se conserva (medianeras, pilares y forjados)
- Obra nueva: muros de hormigón de núcleos y escaleras
- Tabique nuevo / vidrio de salas (línea fina doble)
- Existente que se demuele (trazo discontinuo)
- Itinerario accesible (ascensor y plano a nivel)
- Recorrido de evacuación hacia escalera protegida

CUADRO DE SUPERFICIES ÚTILES

1	Planta abierta de trabajo	96,9 m²	8	Aseo adaptado	4,4 m²
2	Sala de reuniones grande	20,0 m²	9	Vestíbulo de aseos	5,3 m²
3	Sala de descanso	20,0 m²	10	Aseo mujeres	4,8 m²
4	Planta abierta posterior	33,7 m²	11	Aseo hombres	4,7 m²
5	Sala de reuniones mediana	14,8 m²	12	Escalera de emergencia 1	16,9 m²
6	Office y archivo	11,8 m²	13	Escalera de emergencia 2	12,3 m²
7	Ascensor accesible	4,0 m²	14	Circulación y distribución	41,2 m²

Superficie útil del nivel: 290,8 m²

Superficie construida del nivel: 325,1 m²

CASO_009 · PROPUESTA B — Anteproyecto

Planta tercera

Escala 1:100
Medidas en metros

Lámina P04