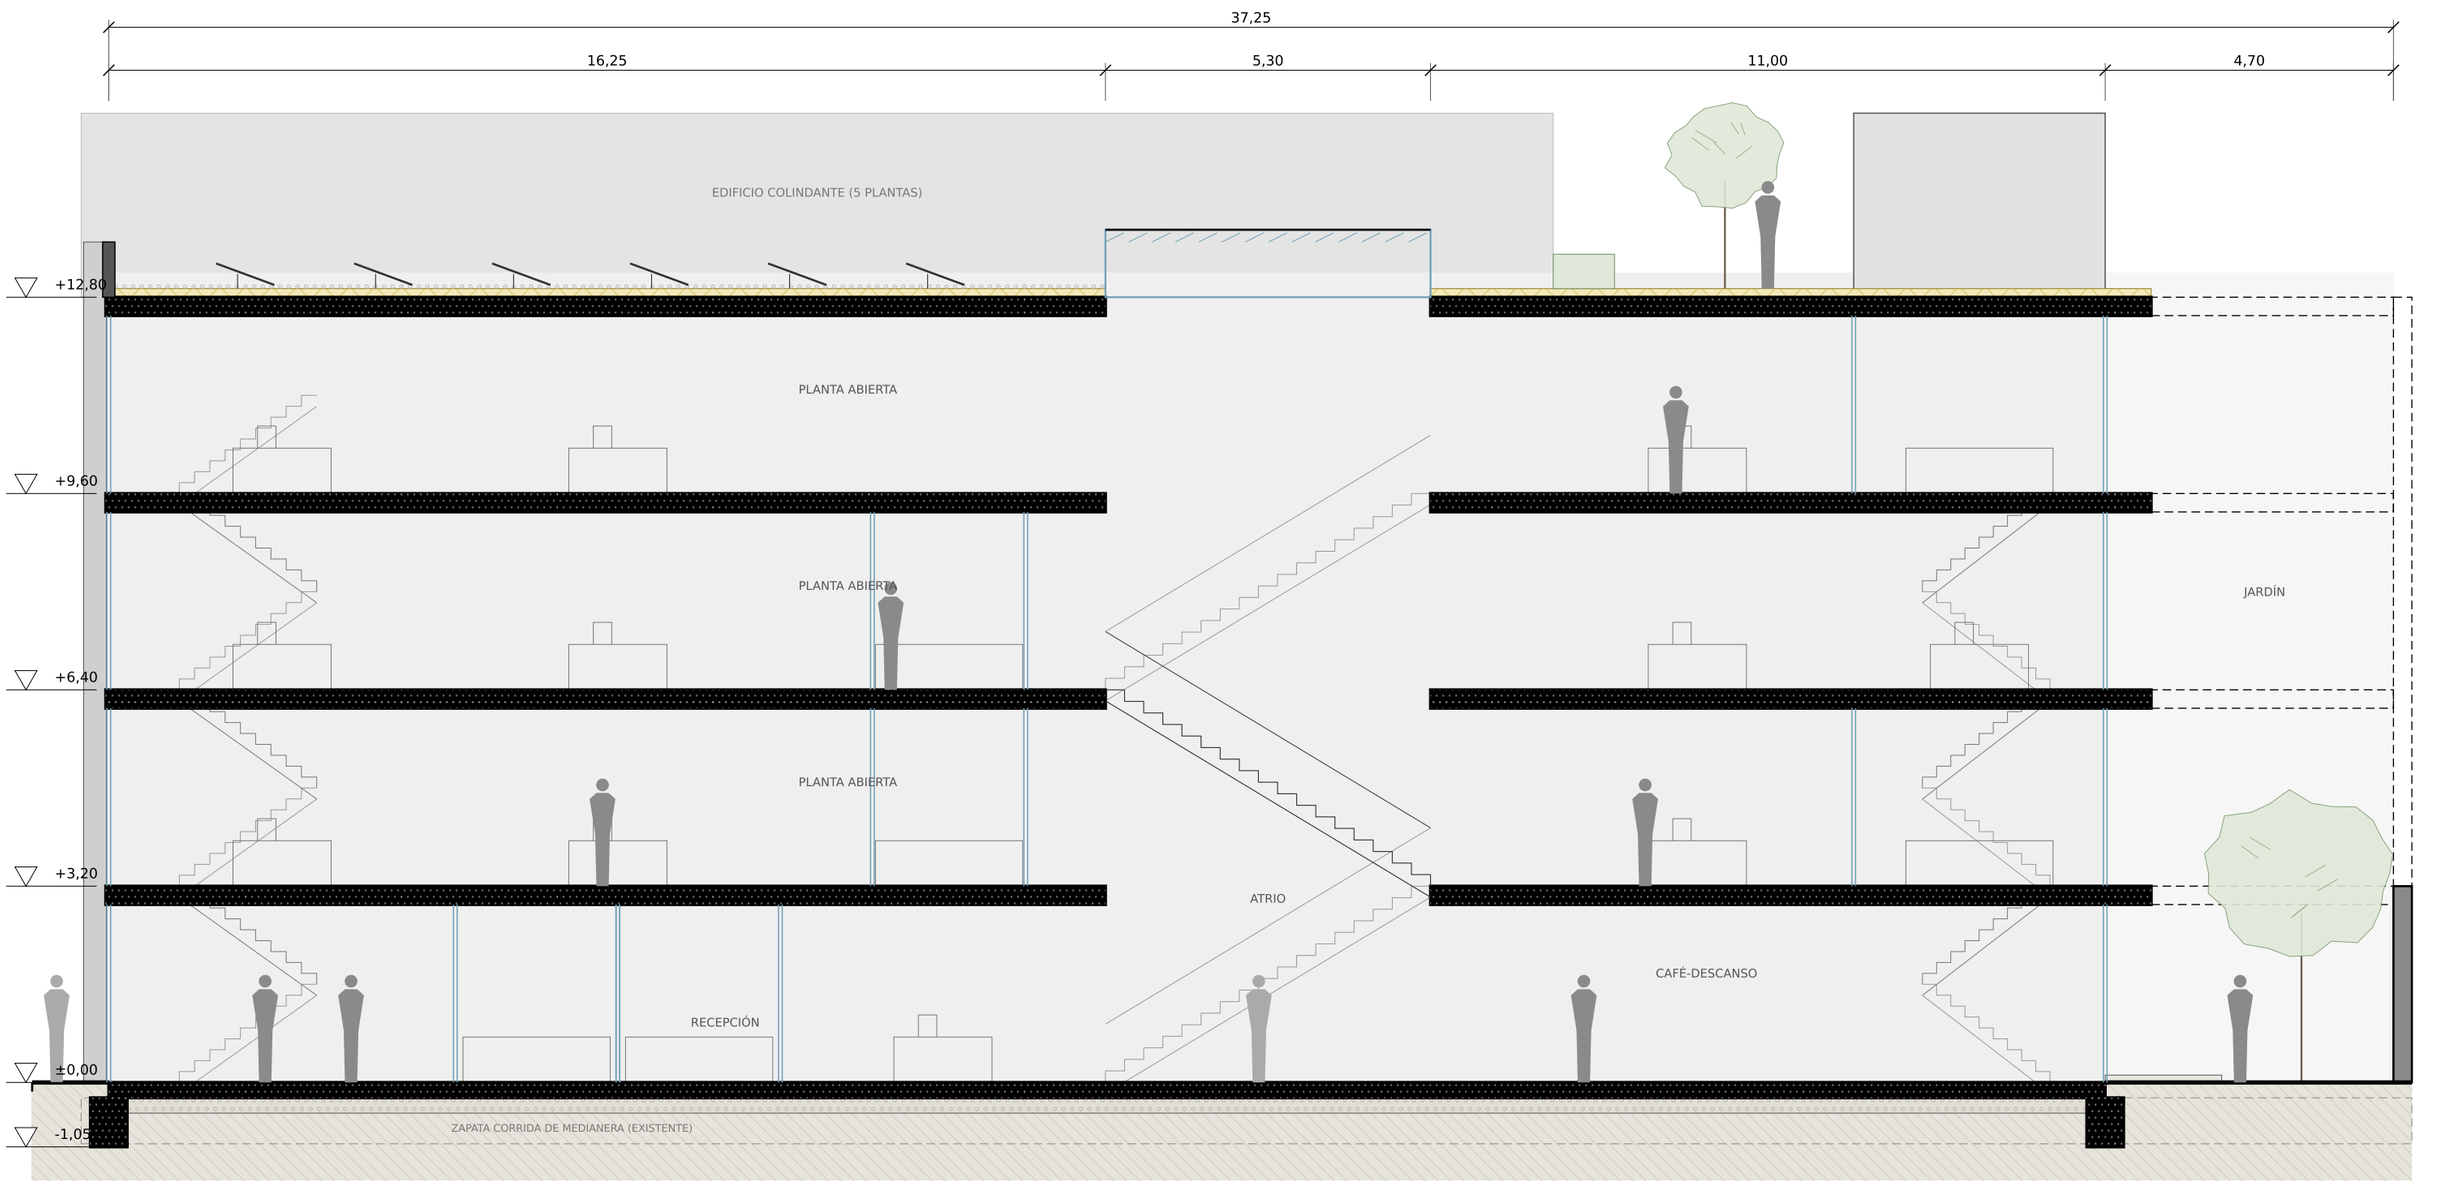


SECCIÓN LONGITUDINAL A-A'

E 1:100

0 1 2 5 10 m

(se mira hacia el oeste)

N

CAPAS Y ALTURAS

Forjado: losa maciza de hormigón existente de 25 cm + recrecido 5 cm (refuerzo con fibra de carbono en zonas de mayor carga).

Pavimento: linóleo 1 cm sobre mortero autonivelante 4 cm; altura libre 2,90 m con instalaciones vistas y difusores perimetrales.

Solera sobre terreno: hormigón 25 cm + lámina + grava 25 cm + terreno compactado. Cimentación de medianeras existente, conservada.

Cubierta plana invertida: formación de pendientes, lámina impermeable, aislante XPS 14 cm, grava 5 cm / pavimento flotante.

Muro cortina frontal con lamas verticales de aluminio anodizado (0,05 x 0,40 m, cada 0,50 m); fachada posterior de vidrio con voladizo de 0,75 m.

CASO_009 · PROPUESTA B — Anteproyecto

Sección longitudinal A-A'

Escala 1:100
Cotas de nivel en metros

Lámina S01