
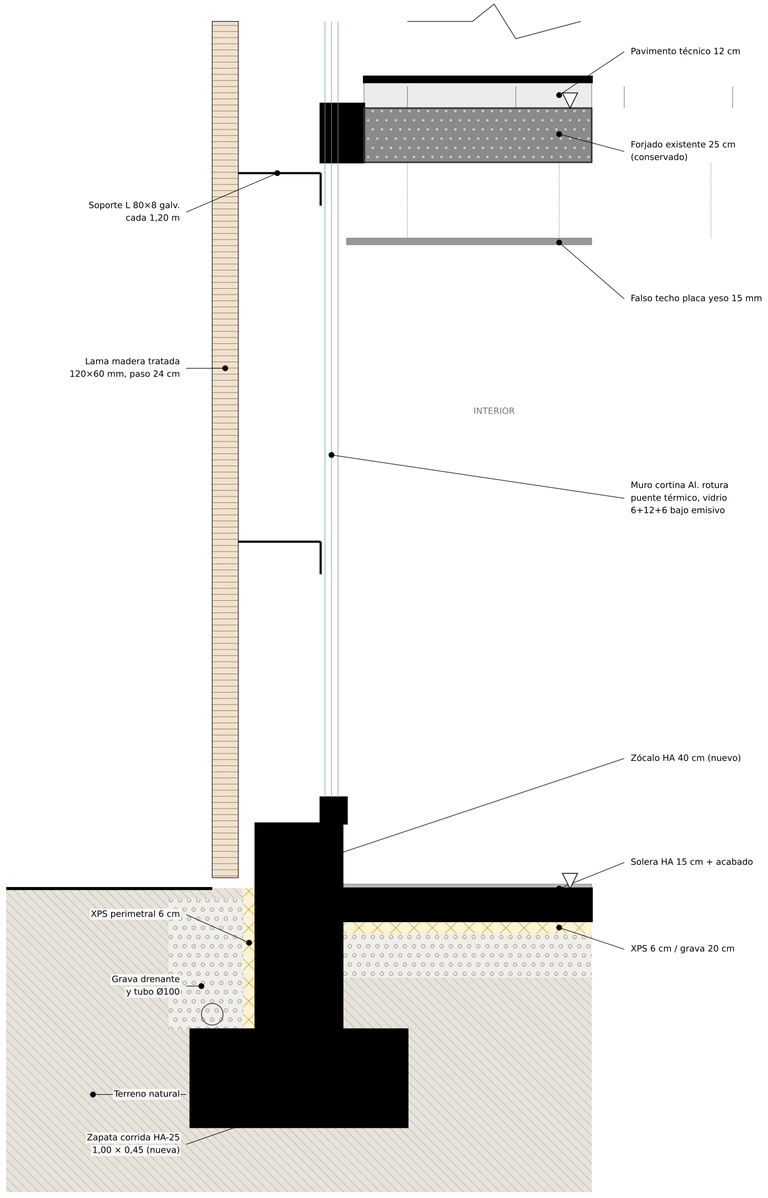



F1 · Arranque: cimentación y planta baja

E 1:20

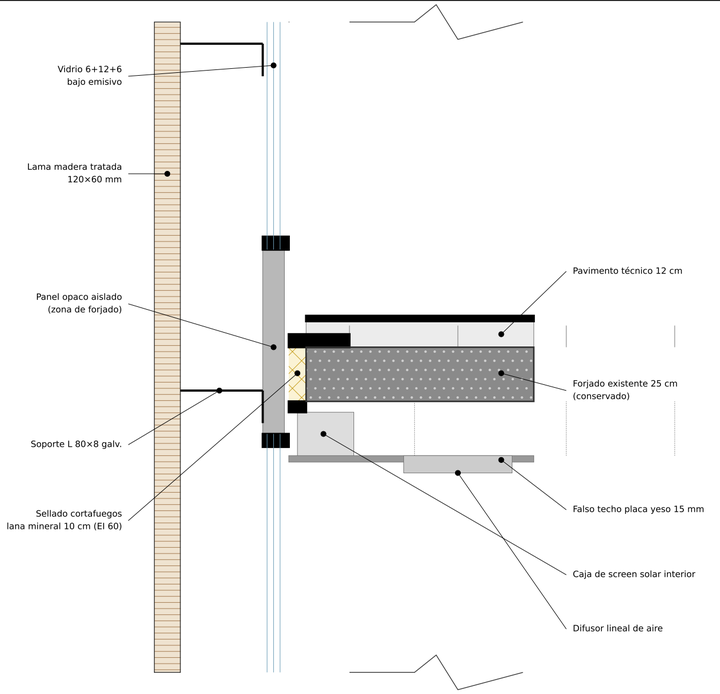

F2 · Forjado intermedio (+7,20)

E 1:20

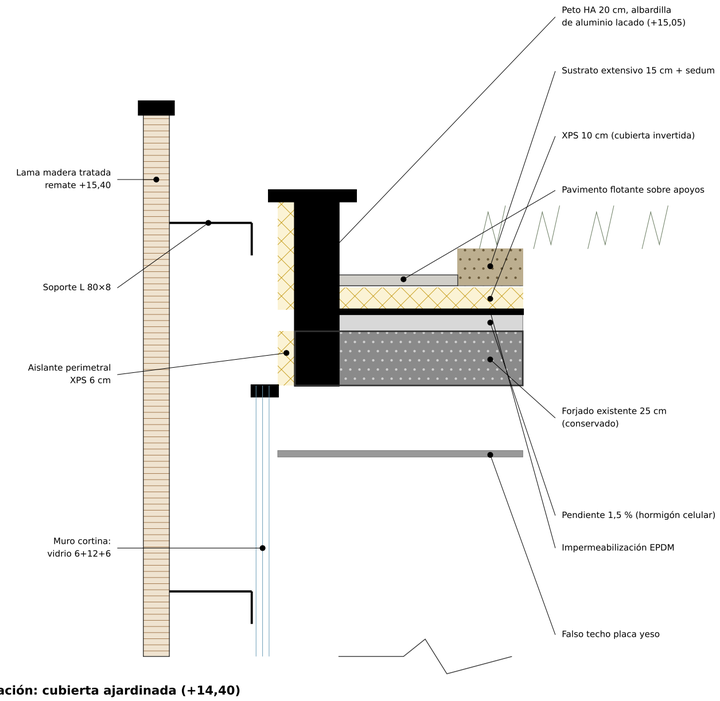

F3 · Coronación: cubierta ajardinada (+14,40)

E 1:20

LEYENDA DE MATERIALES

- Hormigón armado nuevo
- Hormigón existente (conservado)
- Madera tratada (lamas)
- Aislante térmico (XPS / lana mineral)
- Grava / relleno
- Terreno natural
- Vidrio (líneas finas paralelas)

CAPAS Y MATERIALES (de fuera a dentro)

· FACHADA: lamas de madera tratada 120×60 mm (pantalla ventilada, cámara 38 cm) + muro cortina de aluminio con rotura de puente térmico y vidrio 6+12+6 bajo emisivo.

· FORJADO: existente de viguetas y bovedilla 25 cm conservado; pavimento técnico registrable 12 cm; falso techo de placa de yeso 15 mm con plenum de instalaciones.

· CIMENTACIÓN: zapata corrida nueva HA-25 bajo zócalo; solera HA 15 cm sobre XPS 6 cm y grava 20 cm; drenaje perimetral.

· CUBIERTA: invertida ajardinada. Pendiente 1,5 %, EPDM, XPS 10 cm, sustrato extensivo 15 cm y pavimento flotante en la zona de estar.

· INCENDIO: sellado cortafuegos de lana mineral en cada forjado (EI 60). U fachada ≈ 1,3 W/m²K en vidrio y 0,25 en opaco.

CASO_009 · PROPUESTA C

Detalle constructivo de fachada

Renovación integral de edificio de oficinas

ESCALA

1:20

LÁMINA

D01

Anteproyecto