PLANTA BAJA

LEYENDA

- Obra nueva (muros, núcleos, fachada)
- Existente que se conserva
- Existente que se demuele
- Tabique nuevo

ESQUEMA DE EVACUACIÓN Y ACCESIBILIDAD


- Recorrido de evacuación
- Itinerario accesible (Ø 1,50 giro)

EP escalera protegida (EI 120)

ASC ascensor accesible 1,10 × 1,40

Ancho mín. de paso 1,20 m

Atrio con control de humos en lucernario

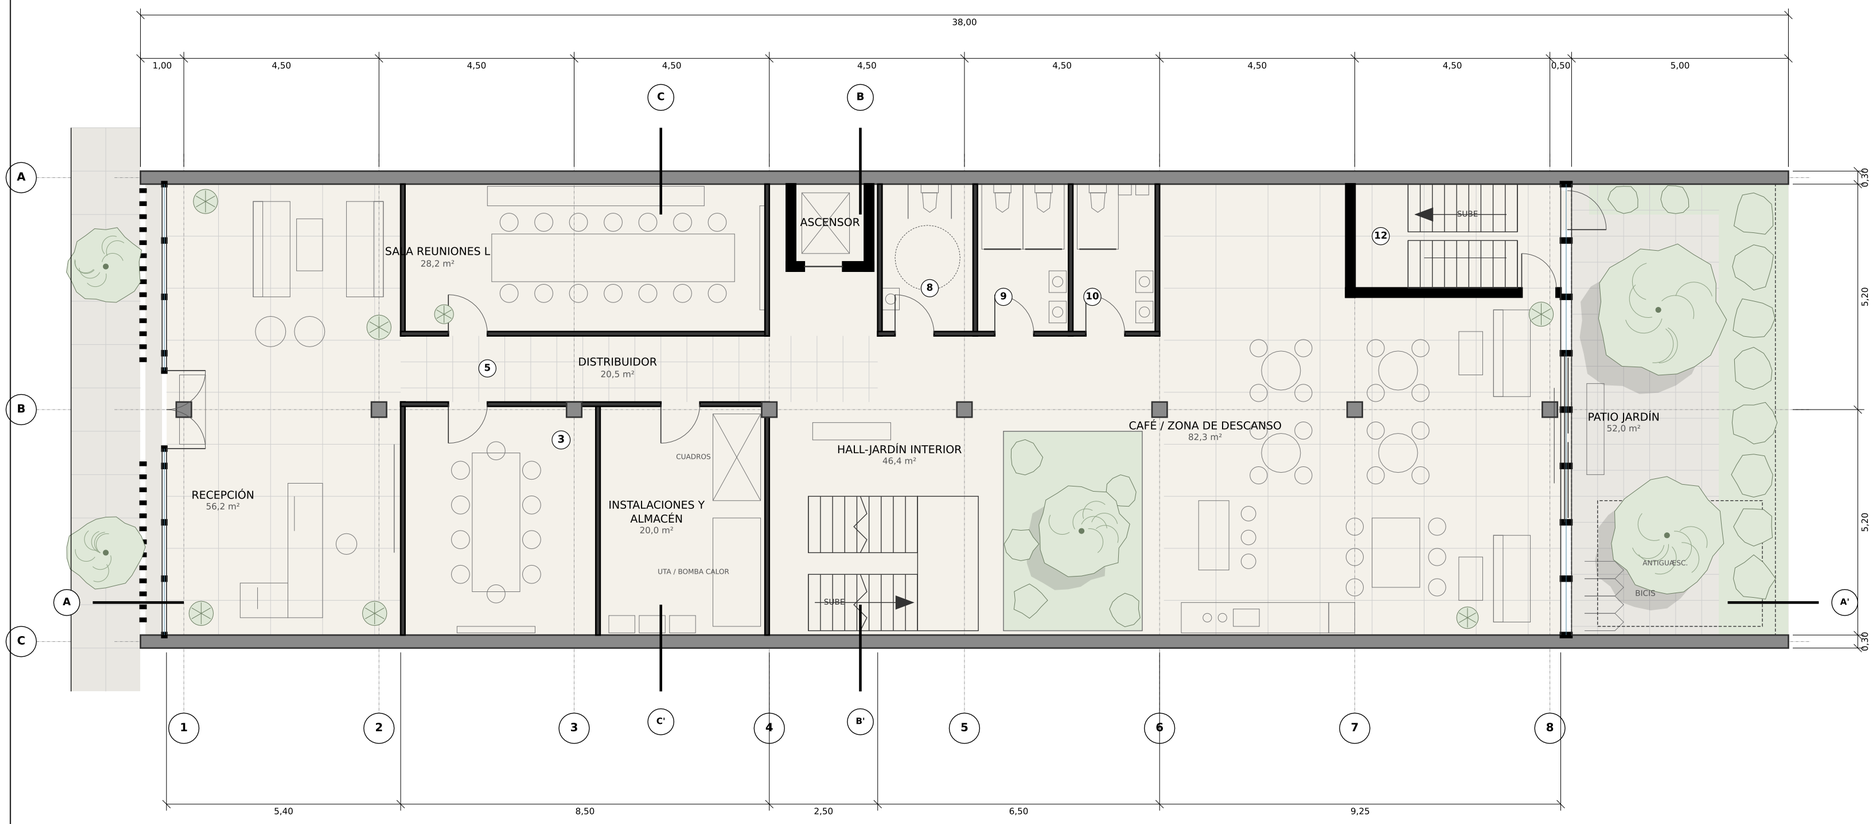


PLANTA BAJA

E 1:100

0 1 2 5 m

N

±0,00

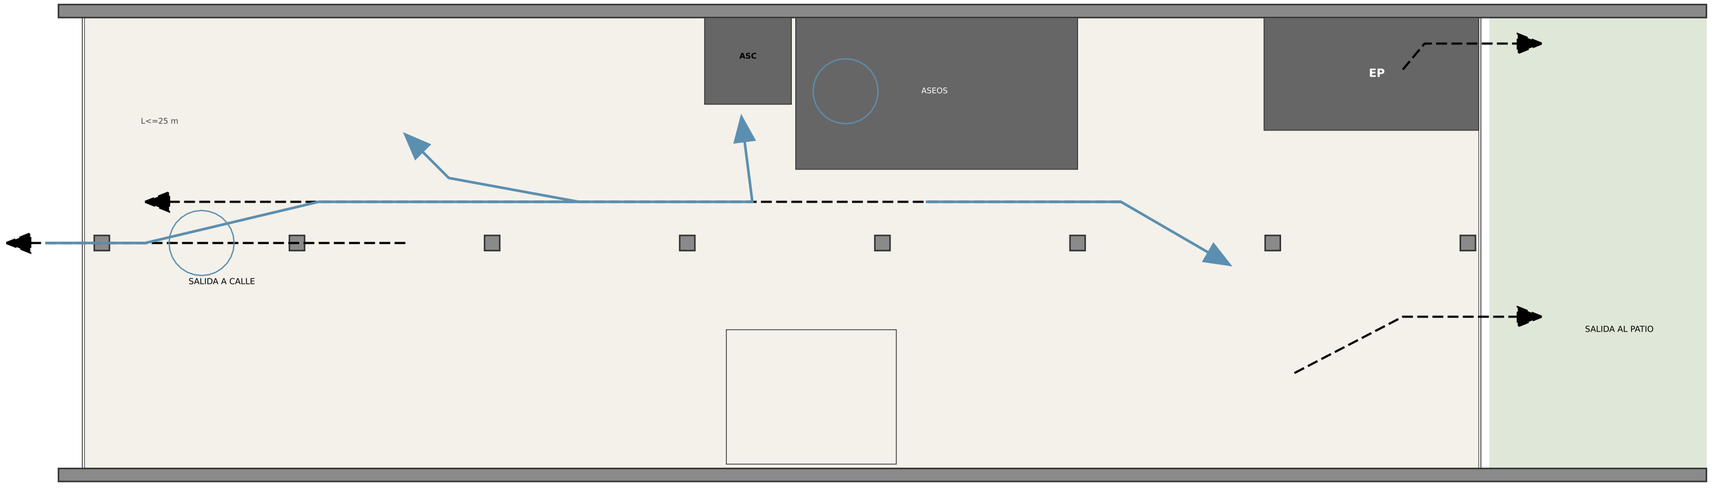

ESQUEMA DE EVACUACIÓN Y ACCESIBILIDAD — PLANTA BAJA

E 1:100

CUADRO DE ESTANCIAS Y SUPERFICIES ÚTILES

01	RECEPCIÓN	56,2 m²	**06**	HALL-JARDÍN INTERIOR	46,4 m²	**11**	CAFÉ / ZONA DE DESCANSO	82,3 m²
02	SALA REUNIONES L	28,2 m²	**07**	ASCENSOR	2,9 m²	**12**	ESCALERA PROTEGIDA	11,4 m²
03	SALA REUNIONES M	23,2 m²	**08**	ASEO ACCESIBLE	7,1 m²	**13**	PATIO JARDÍN	52,0 m²
04	INSTALACIONES Y ALMACÉN	20,0 m²	**09**	ASEOS MUJERES	7,1 m²			
05	DISTRIBUIDOR	20,5 m²	**10**	ASEOS HOMBRES	6,5 m²			

CASO_009 · PROPUESTA C

Planta Baja

Renovación integral de edificio de oficinas

ESCALA

1:100

LÁMINA

P01

Anteproyecto