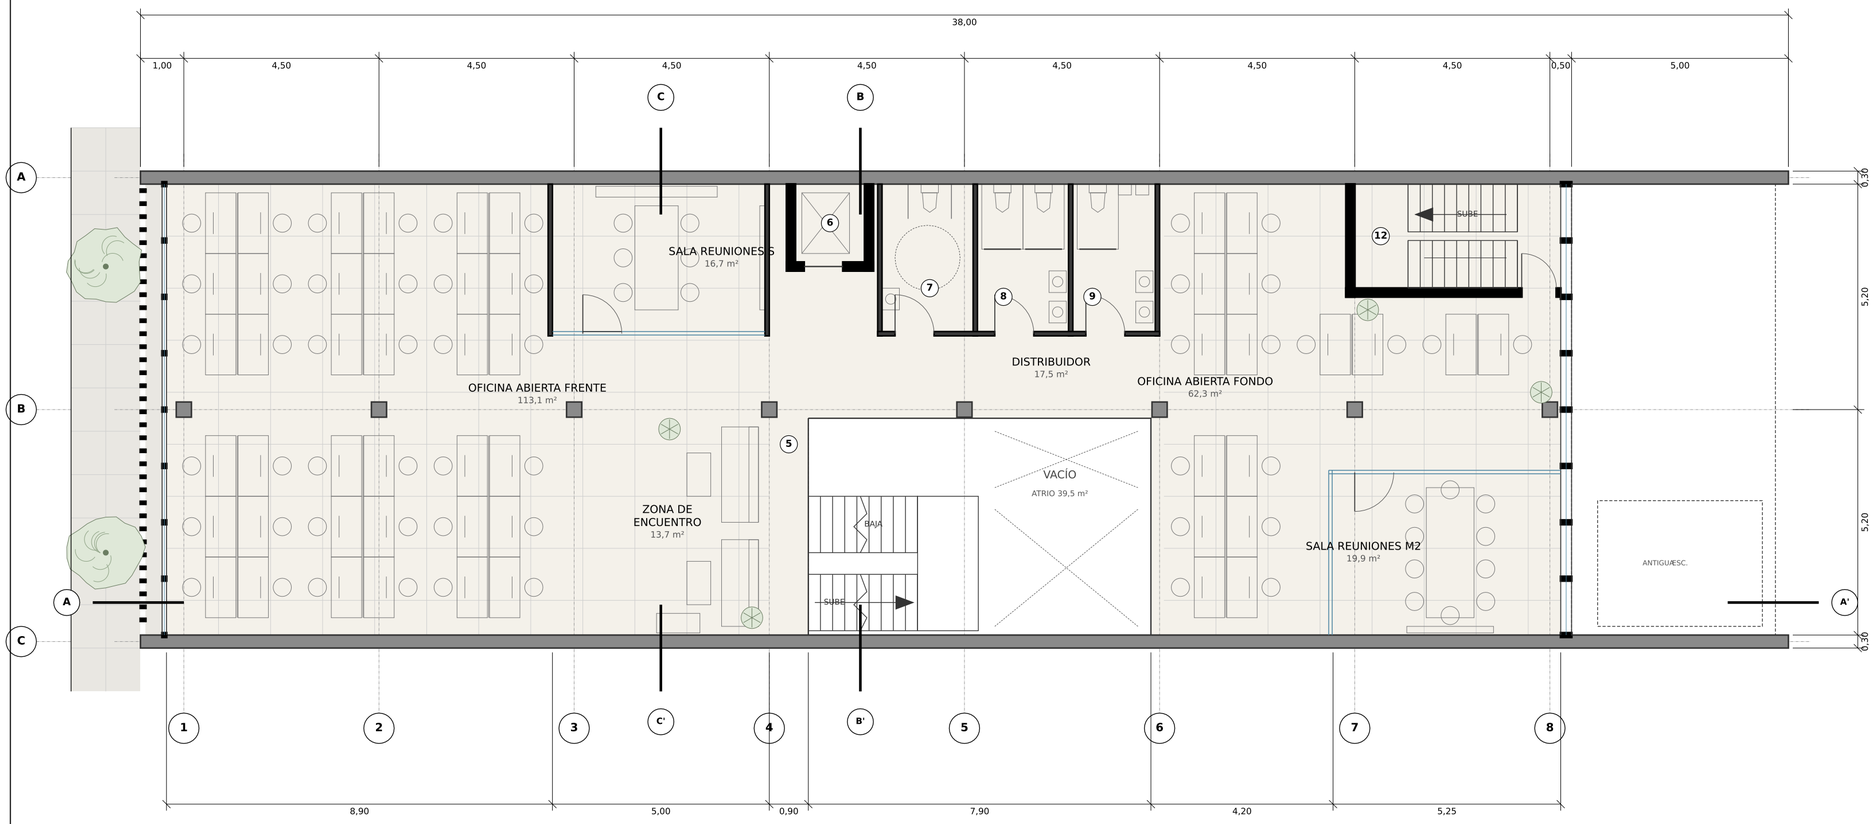


PLANTA SEGUNDA

LEYENDA

- Obra nueva (muros, núcleos, fachada)
- Existente que se conserva
- Existente que se demuele
- Tabique nuevo

ESQUEMA DE EVACUACIÓN Y ACCESIBILIDAD

- Recorrido de evacuación
- Itinerario accesible (Ø 1,50 giro)

EP escalera protegida (EI 120)

ASC ascensor accesible 1,10 × 1,40

Ancho mín. de paso 1,20 m

Atrio con control de humos en lucernario


PLANTA SEGUNDA

E 1:100

0 1 2 5 m

N

+7.20

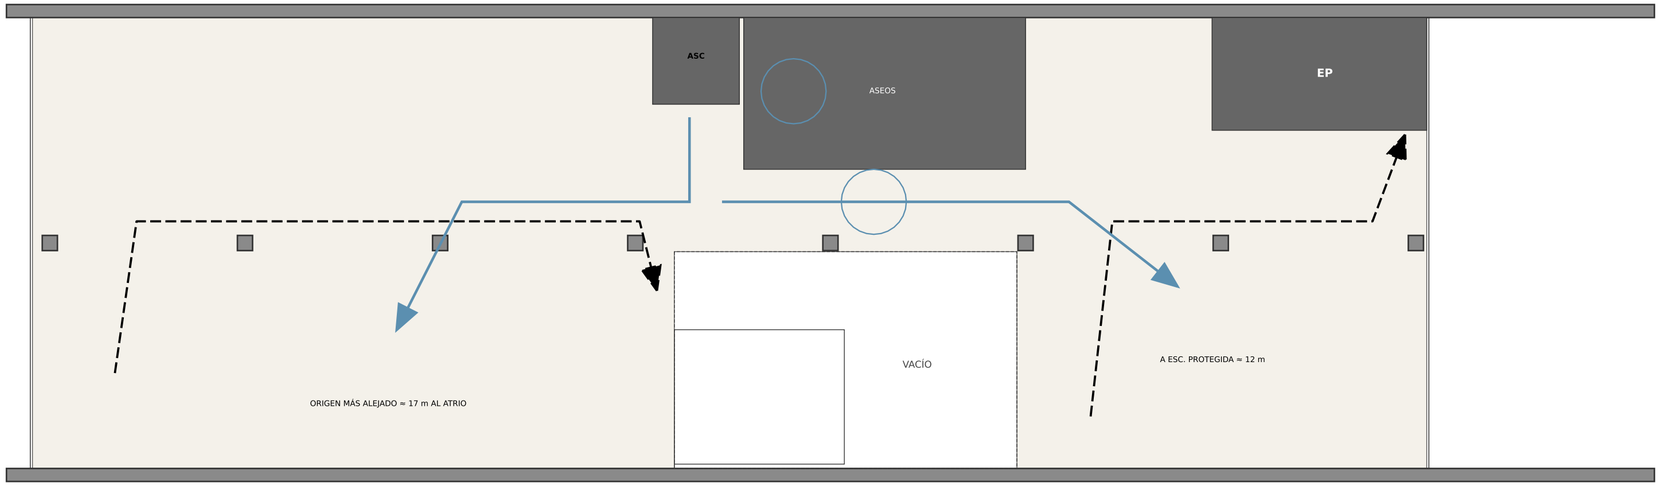

ESQUEMA DE EVACUACIÓN Y ACCESIBILIDAD — PLANTA SEGUNDA

E 1:100

CUADRO DE ESTANCIAS Y SUPERFICIES ÚTILES

01	OFICINA ABIERTA FRENTE	113,1 m²	**06**	ASCENSOR	2,9 m²	**11**	SALA REUNIONES M2	19,9 m²
02	SALA REUNIONES S	16,7 m²	**07**	ASEO ACCESIBLE	7,1 m²	**12**	ESCALERA PROTEGIDA	11,4 m²
03	ZONA DE ENCUENTRO	13,7 m²	**08**	ASEOS MUJERES	7,1 m²	**13**	VACÍO (ATRIO)	39,5 m²
04	DISTRIBUIDOR	17,5 m²	**09**	ASEOS HOMBRES	6,5 m²			
05	RELLANO ESCALERA	4,7 m²	**10**	OFICINA ABIERTA FONDO	62,3 m²			

CASO_009 · PROPUESTA C

Planta Segunda

Renovación integral de edificio de oficinas

ESCALA

1:100

LÁMINA

P03

Anteproyecto