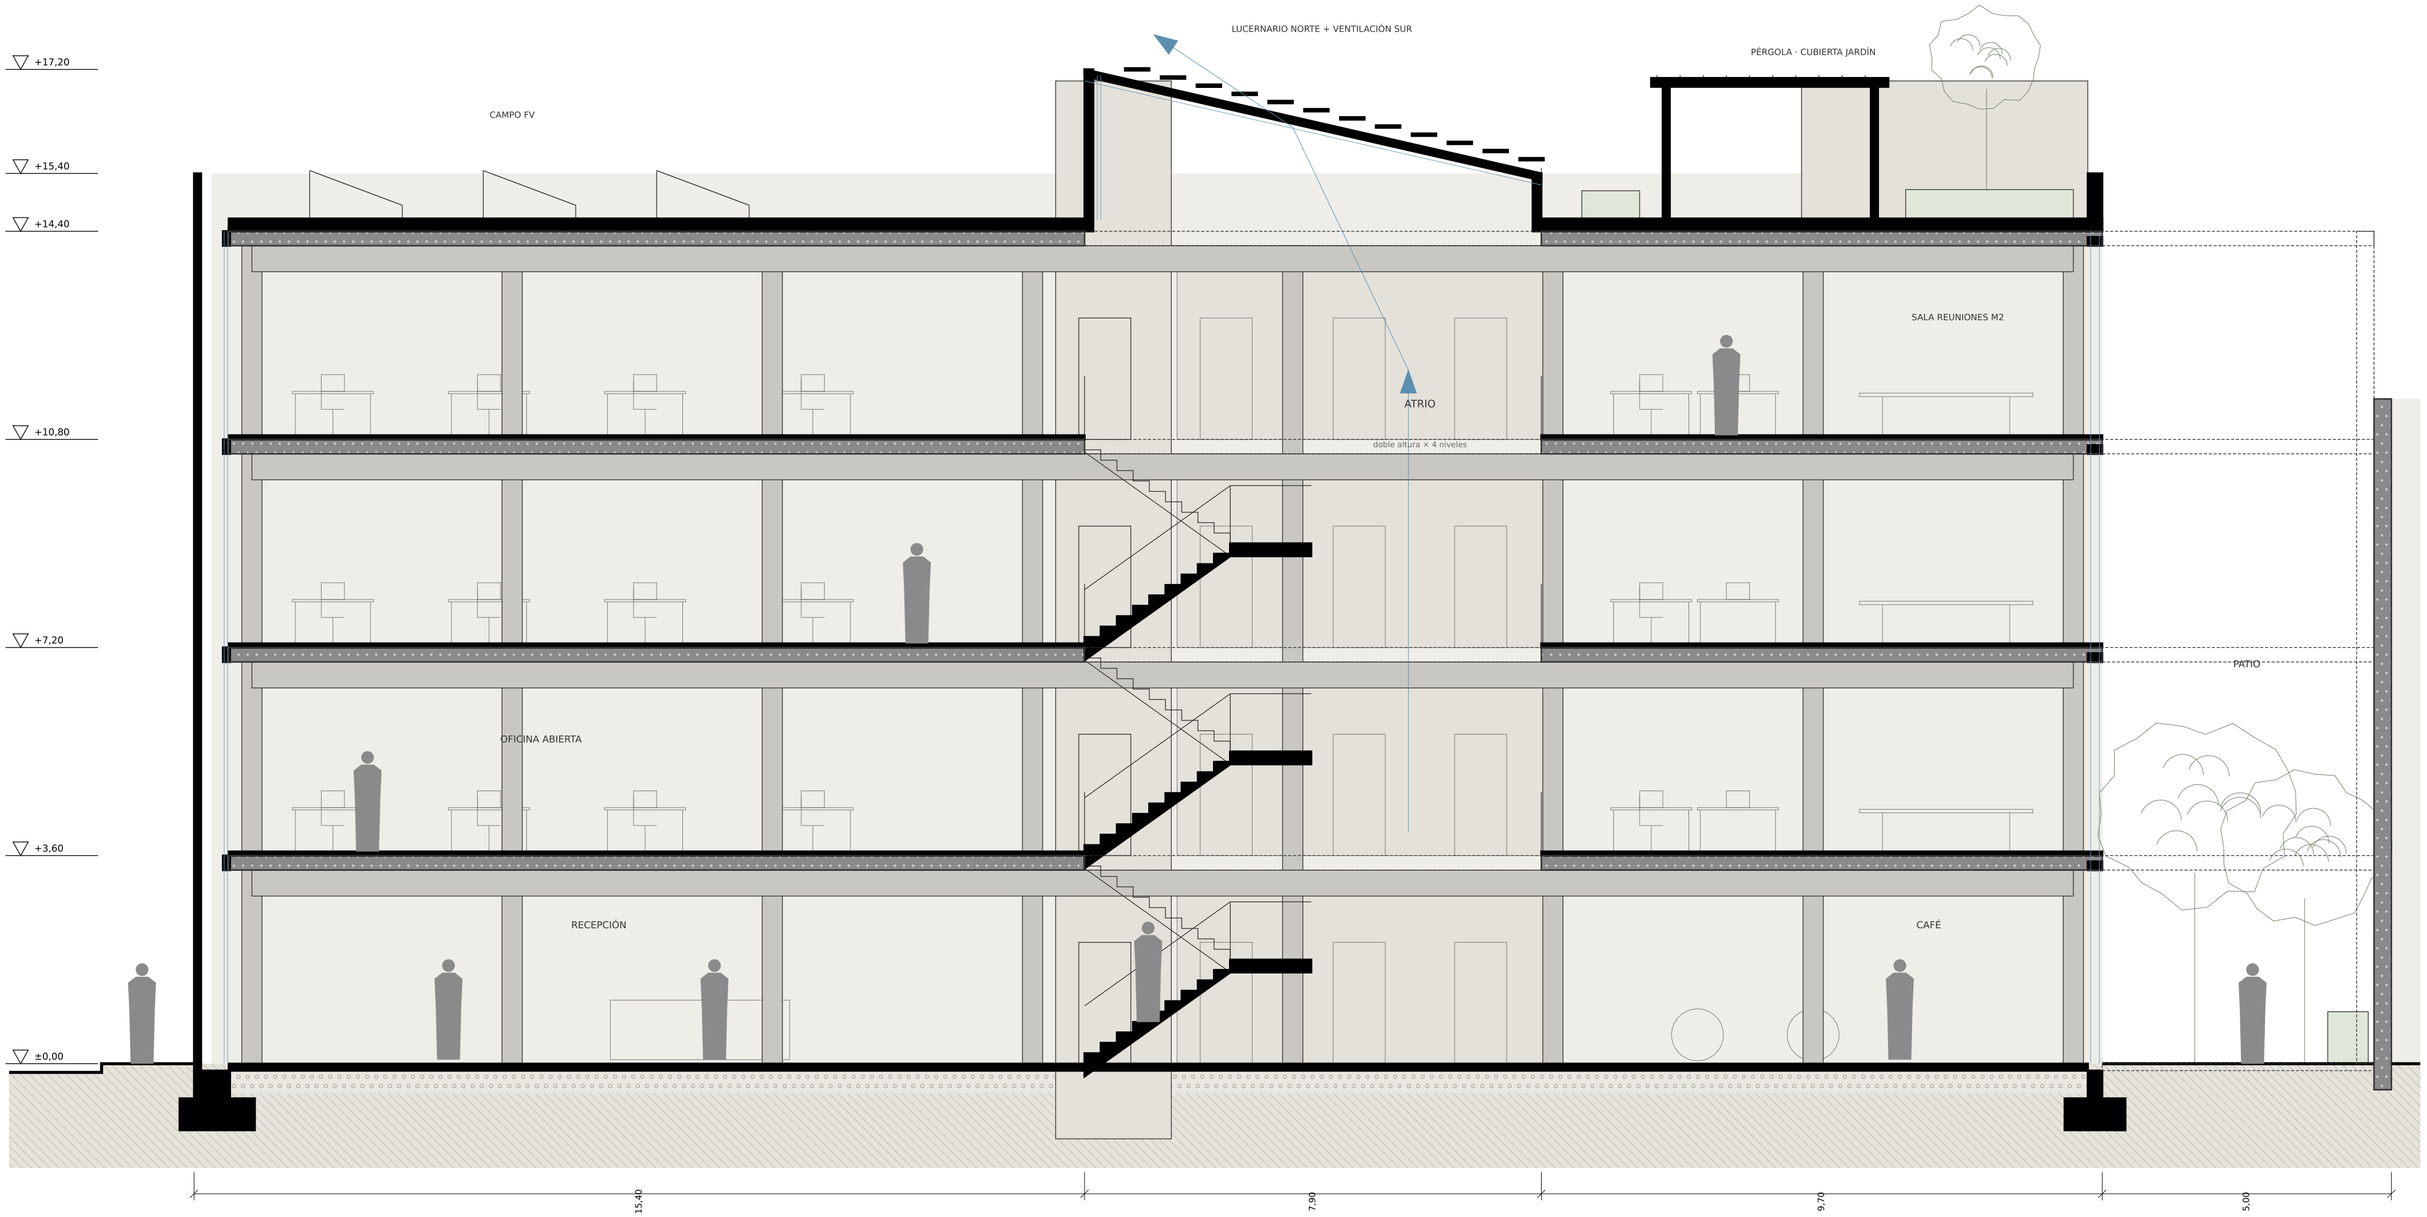


SECCIÓN LONGITUDINAL A-A'

E 1:75

0 1 2 5 10 m

LEYENDA

- Cortado: obra nueva
- Cortado: existente que se conserva
- Existente que se demuele
- Terreno natural
- Vidrio / lucernario
- Visto en proyección (núcleos)
- Ventilación natural (efecto chimenea)

NOTAS

· Corte por el plano x = 9,95 m (pata A de la escalera del atrio), mirando al oeste.

· Forjados existentes (viguetas + bovedilla 25 cm) conservados en cuerpo frontal y trasero.

· El hueco del atrio (7,90 × 5,00 m) sustituye al forjado demolido; escalera de acero y madera.

· Lucernario inclinado al norte con lamas fijas y banda practicable al sur (extracción de aire caliente).

· Cubierta: campo fotovoltaico al frente y terraza-jardín con pérgola al fondo.

· Pantalla de lamas verticales de madera tratada ante el muro cortina (ver D01).

CASO_009 · PROPUESTA C

Sección longitudinal A-A'

Renovación integral de edificio de oficinas

ESCALA

1:75

LÁMINA

S01

Anteproyecto