



SECCIÓN TRANSVERSAL B-B'

E 1:75

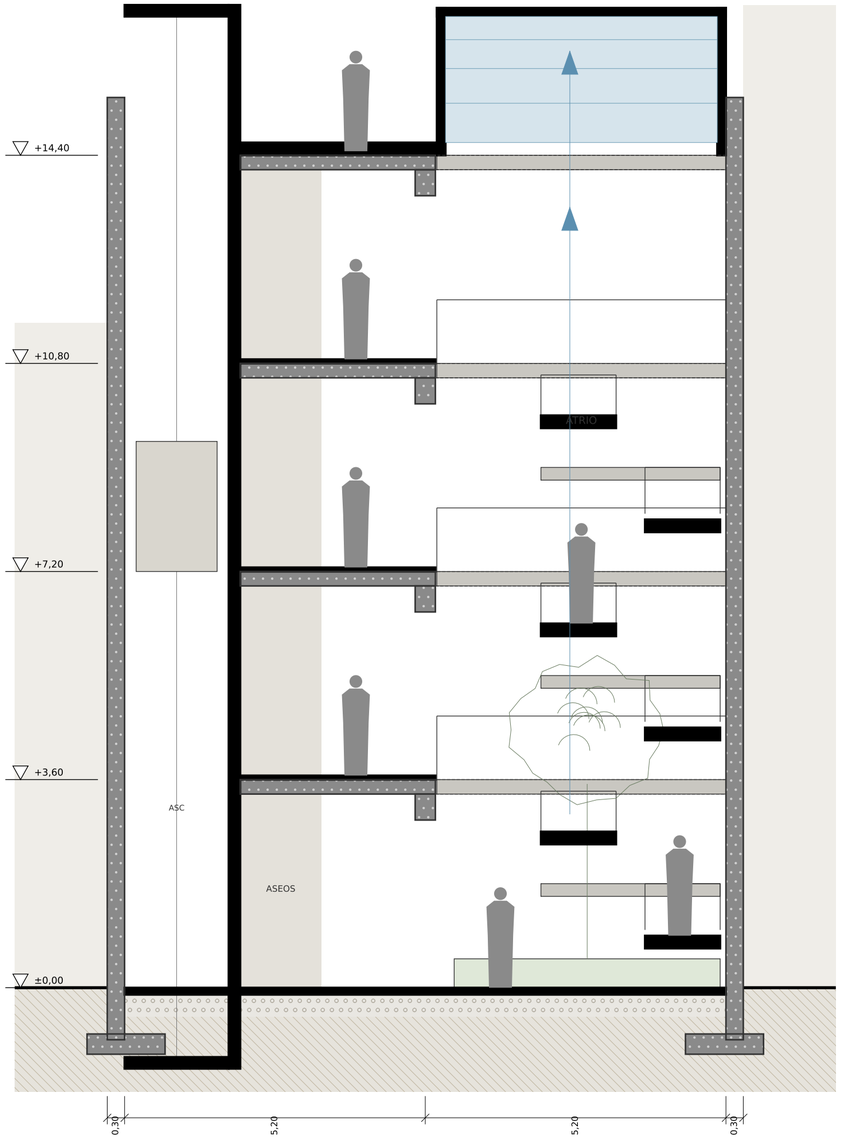

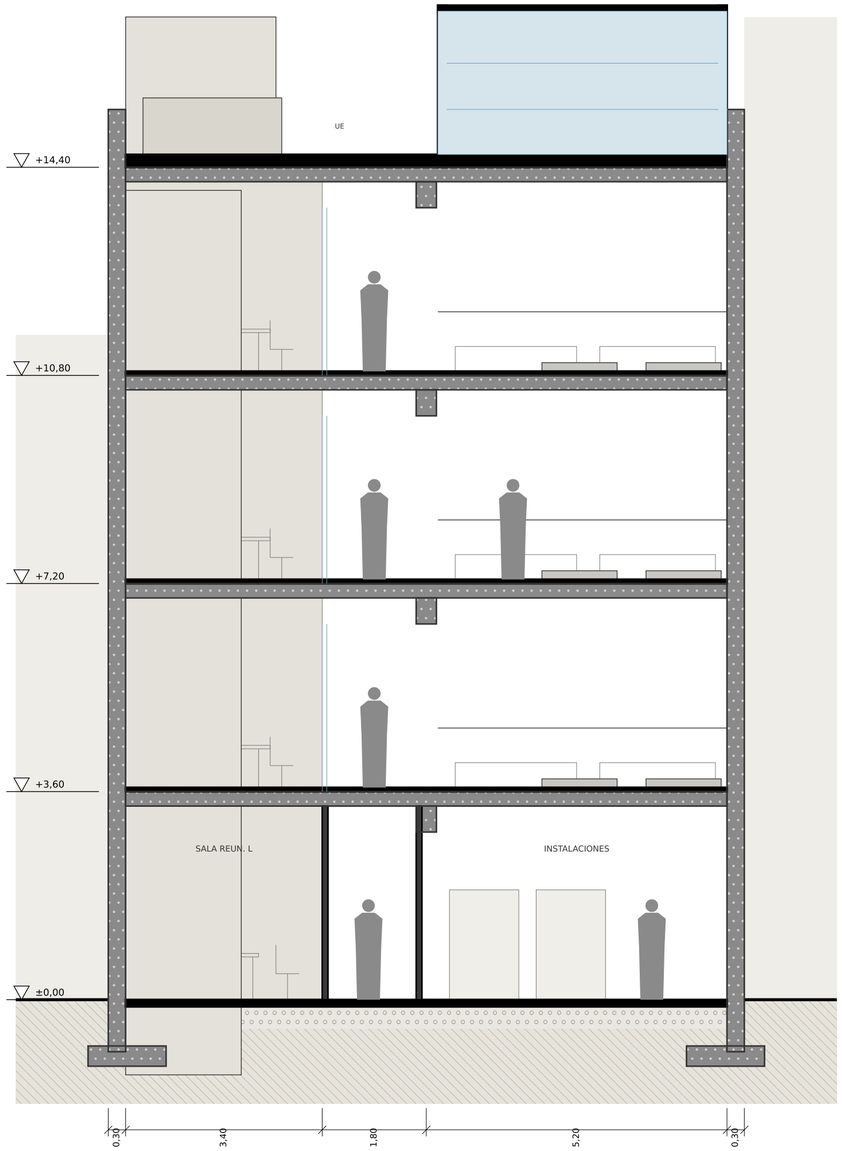


SECCIÓN TRANSVERSAL C-C'

E 1:75

LEYENDA

- Cortado: obra nueva
- Cortado: existente que se conserva
- Existente que se demuele
- Terreno natural
- Vidrio / lucernario
- Visto en proyección (núcleos)
- Ventilación natural (efecto chimenea)

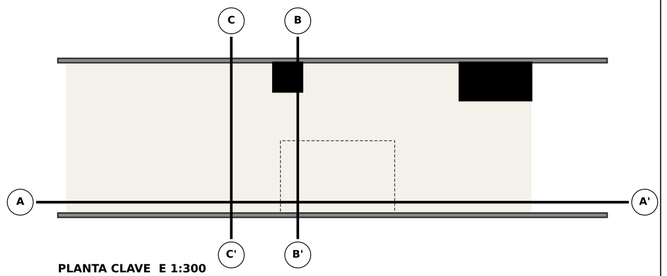

PLANTA CLAVE E 1:300

CUADRO DE NIVELES Y ALTURAS

Cota calle / PB	±0,00
Planta primera	+3,60
Planta segunda	+7,20
Planta tercera	+10,80
Cubierta transitable	+14,40
Antepecho / lamas	+15,40
Lucernario (cumbrera)	+17,20
Casetones ascensor y escalera	+17,00
Altura libre interior	2,80 m
Canto de forjado existente	0,25 m

CASO_009 · PROPUESTA C

Secciones transversales B-B' y C-C'

Renovación integral de edificio de oficinas

ESCALA

1:75

LÁMINA

S02

Anteproyecto