
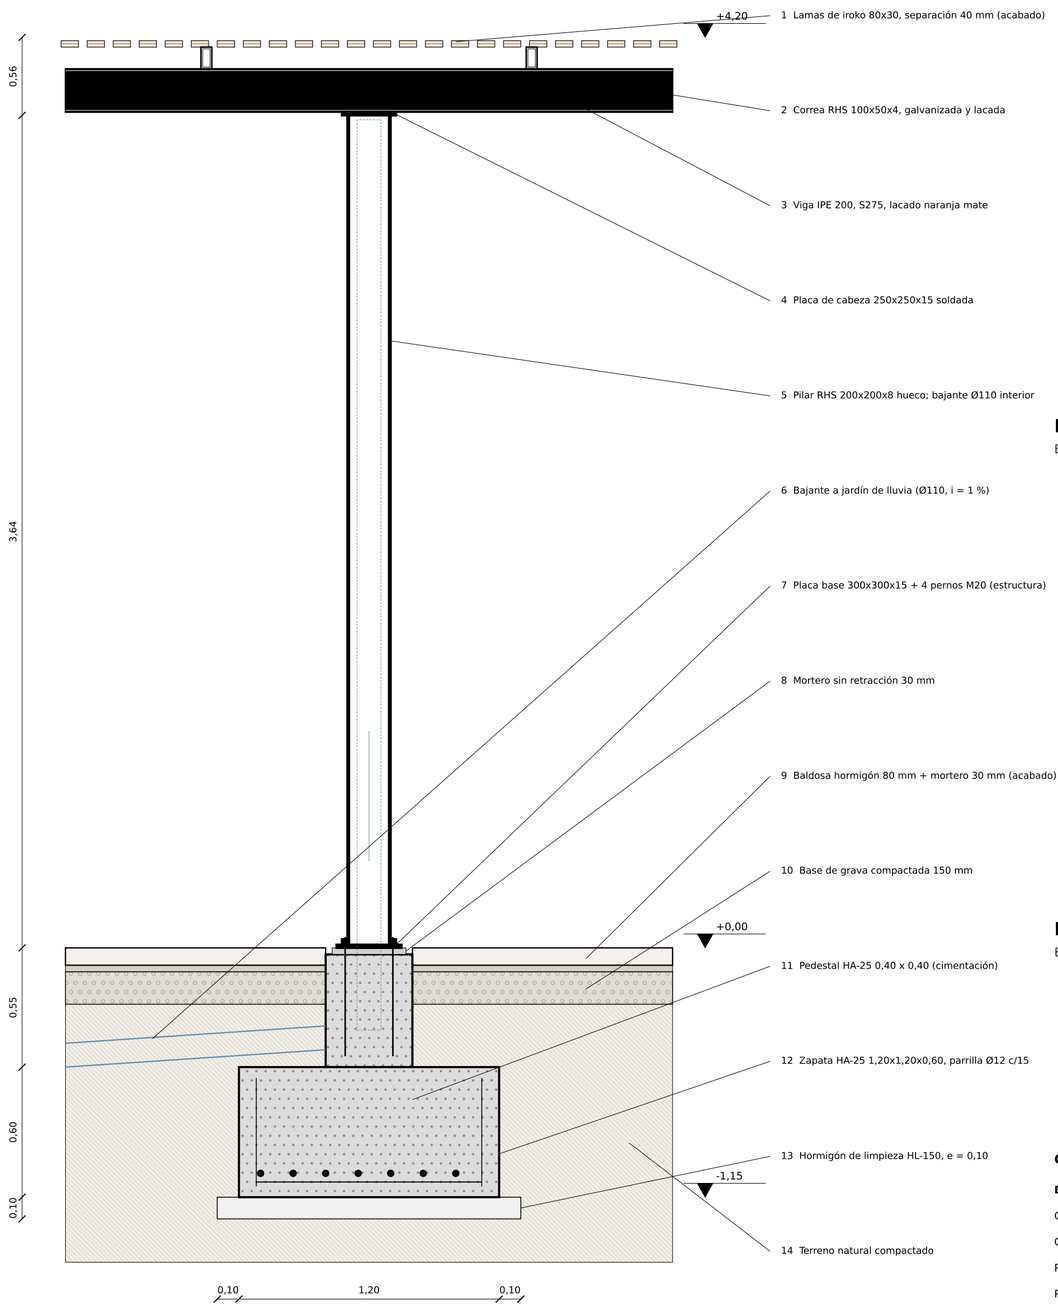



F1 · PILAR DE PÉRGOLA: CIMENTACIÓN, PAVIMENTO Y CUBIERTA

E 1:20 · fragmento de la cimentación a la cubierta (módulo tipo, cota de lamas +4,20)

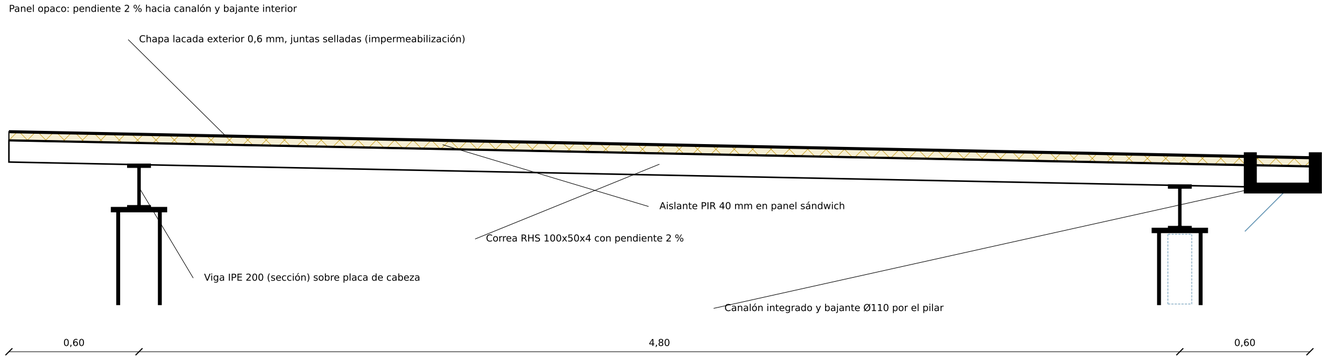

F2 · CUBIERTA CON PANEL OPACO · CORTE TRANSVERSAL

E 1:20 · capas: acabado, aislante, estructura; recogida de pluviales

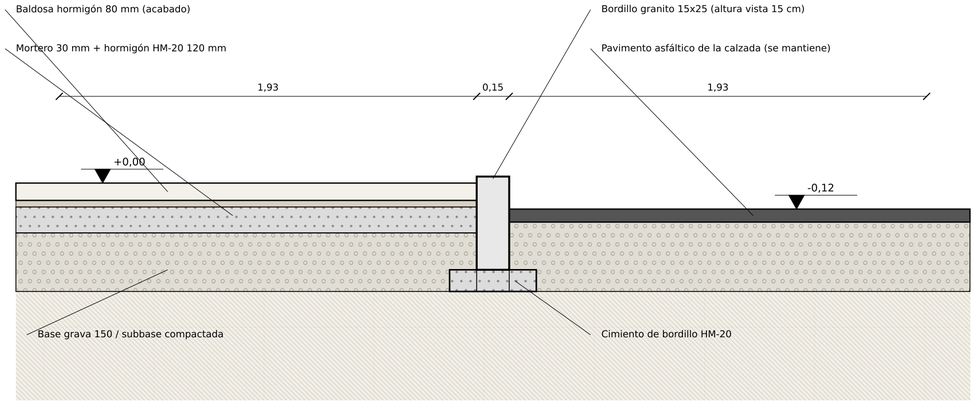

F3 · ENCUENTRO DEL PAVIMENTO DE LA PLAZA CON LA CALZADA

E 1:20 · se mantiene la sección de la calzada perimetral

CUADRO DE CAPAS Y MATERIALES

Elemento	Capas (de arriba abajo)
Cubierta de lamas	Lamas iroko 80x30 (acabado) · correa RHS 100x50x4 · viga IPE 200 (estructura) · pilar RHS 200x200x8
Cubierta de panel opaco	Chapa lacada 0,6 (impermeabilización) · aislante PIR 40 · chapa interior · correa · viga · canalón
Pavimento de estancia	Baldosa hormigón 80 · mortero 30 · base grava 150 · terreno compactado
Pavimento de juegos	Caucho SBR continuo 60 (amortiguador) · base drenante grava 150 · terreno
Cimentación de pilar	Zapata HA-25 1,20x1,20x0,60 · pedestal 0,40 · limpieza 0,10 · terreno firme (>=150 kPa)
Jardín de lluvia	Vegetación · sustrato 0,40 · geotextil · grava 0,45 · tubo dren Ø110 · rebosadero
Carpintería	No hay cerramientos ni carpintería: espacio abierto; sólo barandilla de pasarela (acero 1,10 m)

CASO_010 · PROPUESTA A Detalle constructivo: pilar de pérgola, cubierta y pavimento	Plano **D01**	
Anteproyecto · Dos plazas de barrio	Escala 1:20	Lámina D01