

PLANTA PLAZA 1 · NIVEL 0


E 1:200 · módulo 1:50 · detalle 1:100

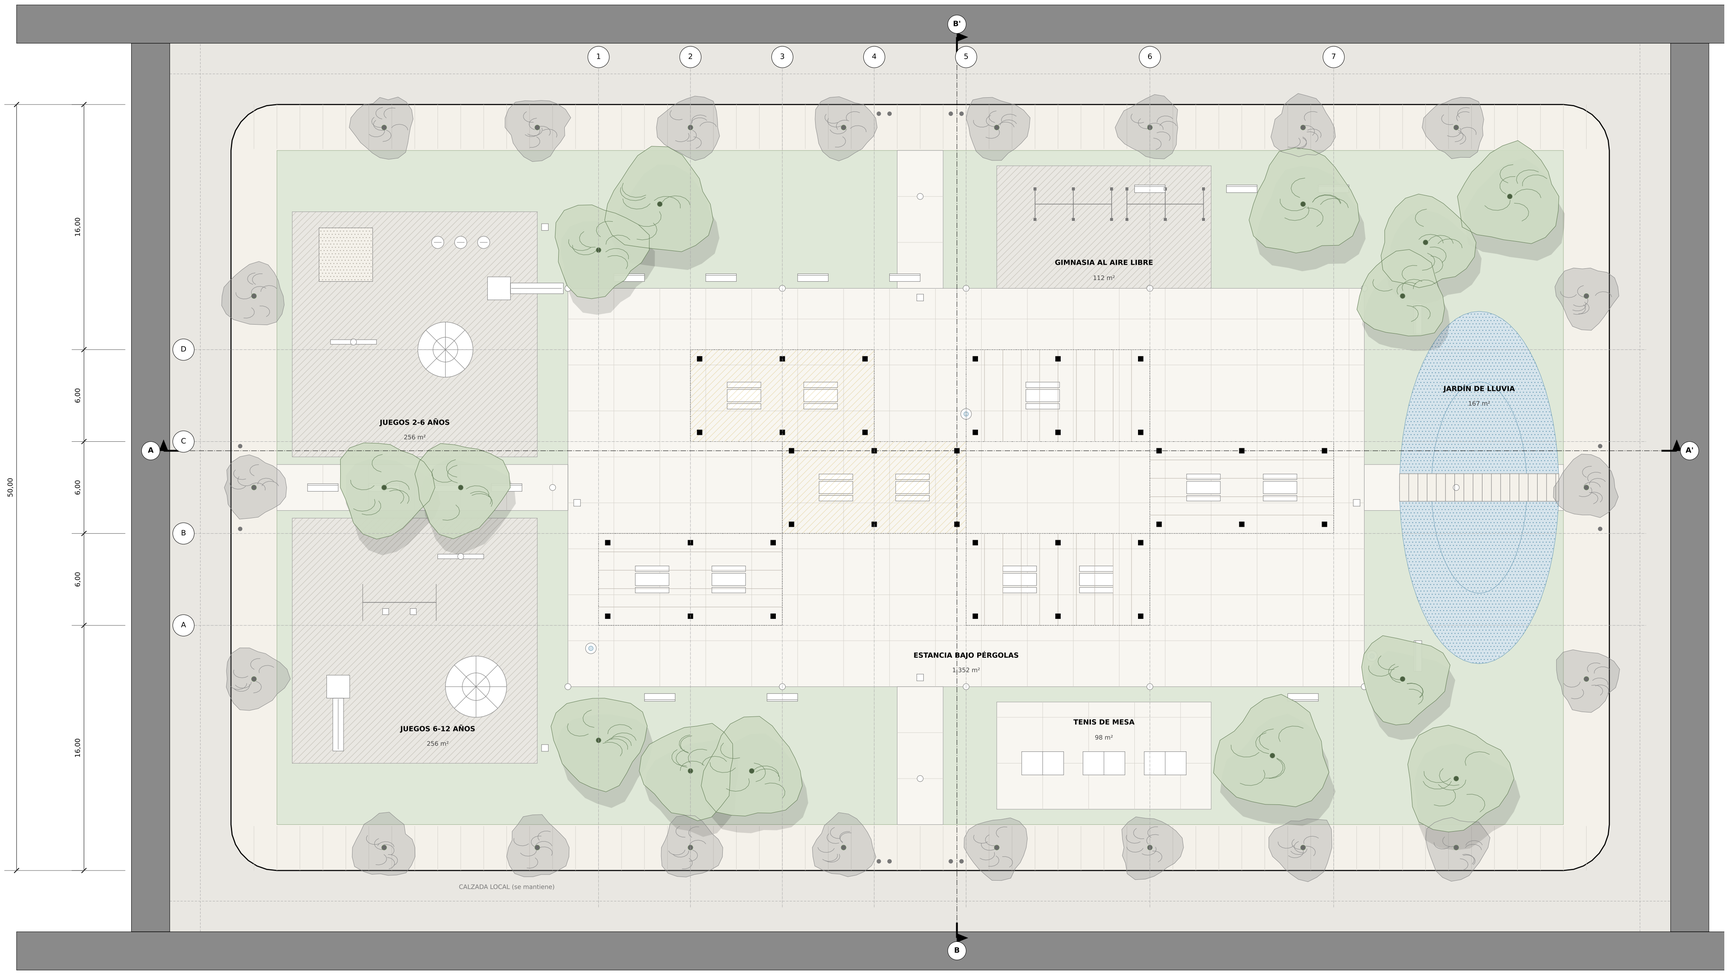

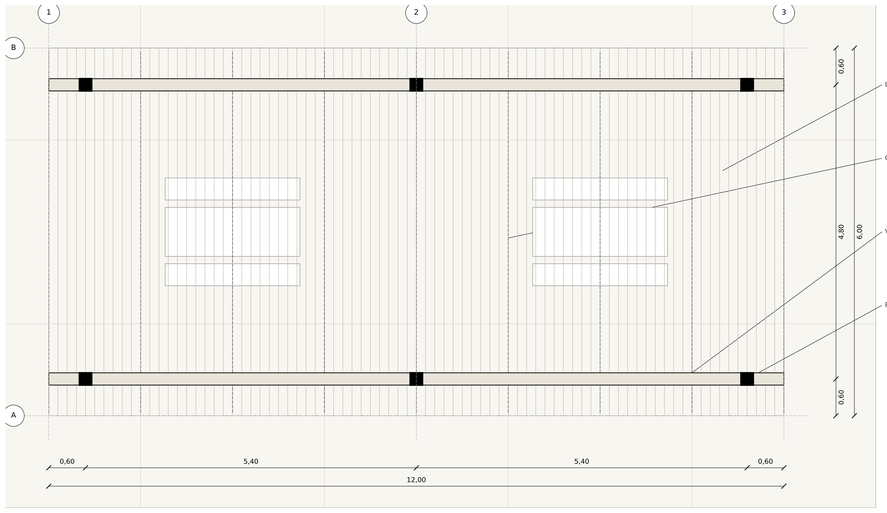

MÓDULO TIPO DE PÉRGOLA 12 x 6 m

E 1:50 · estructura de acero, retícula de ejes 1-3 / A-B

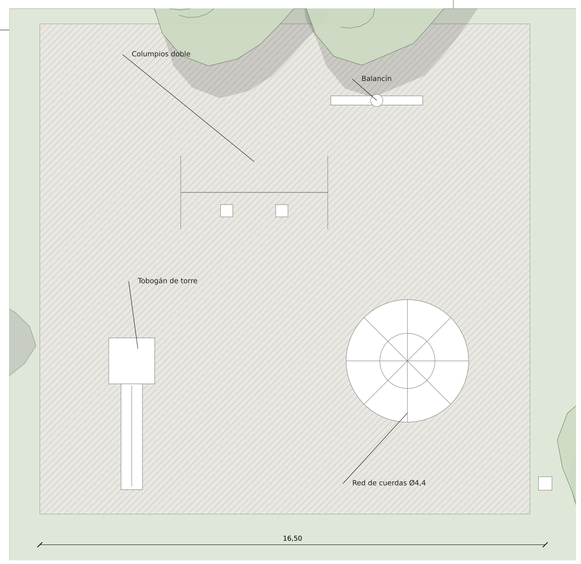

ZONA DE JUEGOS 6-12 AÑOS

E 1:100 · pavimento amortiguador continuo y bancos de vigilancia

CUADRO DE SUPERFICIES · PLAZA 1

Estancia bajo pérgolas	1.352 m²
Juegos 2-6 años	256 m²
Juegos 6-12 años	256 m²
Gimnasia al aire libre	112 m²
Tenis de mesa	98 m²
Jardín de lluvia	167 m²
Pasarela de madera	21 m²
Pradera	1.315 m²
Recorridos de acceso (3 m)	118 m²
Acera perimetral conservada y renovada	804 m²
TOTAL PARCELA (intervención)	**4.500 m²**

Superficie cubierta por pérgolas: 432 m² (10 % de la parcela)

Arbolado: 22 ejemplares existentes conservados + 14 nuevos

Pérgolas: 6 cubiertas distintas (alturas 3,4-4,6 m)

LEYENDA

- Pradera / césped
- Pavimento duro (hormigón pulido, juntas 3 m)
- Juegos: pavimento amortiguador continuo
- Pavimento deportivo
- Jardín de lluvia (cota -0,45)
- Pérgola con lamas (proyección, discontinuo)
- Pérgola con panel opaco (recogida de pluviales)
- Arbolado existente que se conserva
- Fachada de manzana colindante (existente)
- Pilar de pérgola RHS 200x200x8 (nuevo)
- Luminaria / bolardo (gris relleno) / fuente

Orientación supuesta: norte arriba; sol de mediodía al norte (hemisferio sur).

Terreno llano (≤0,5 %). Cotas en metros. Ejes de pérgolas: 1-n / A-n.

CASO_010 · PROPUESTA A Planta de Plaza 1 · nivel 0 (calle)	Plano **P01**	
Anteproyecto · Dos plazas de barrio	Escala 1:200	Lámina P01