
PLANTA PLAZA 2 · NIVEL 0

E 1:200 · módulo 1:50 · detalle 1:100

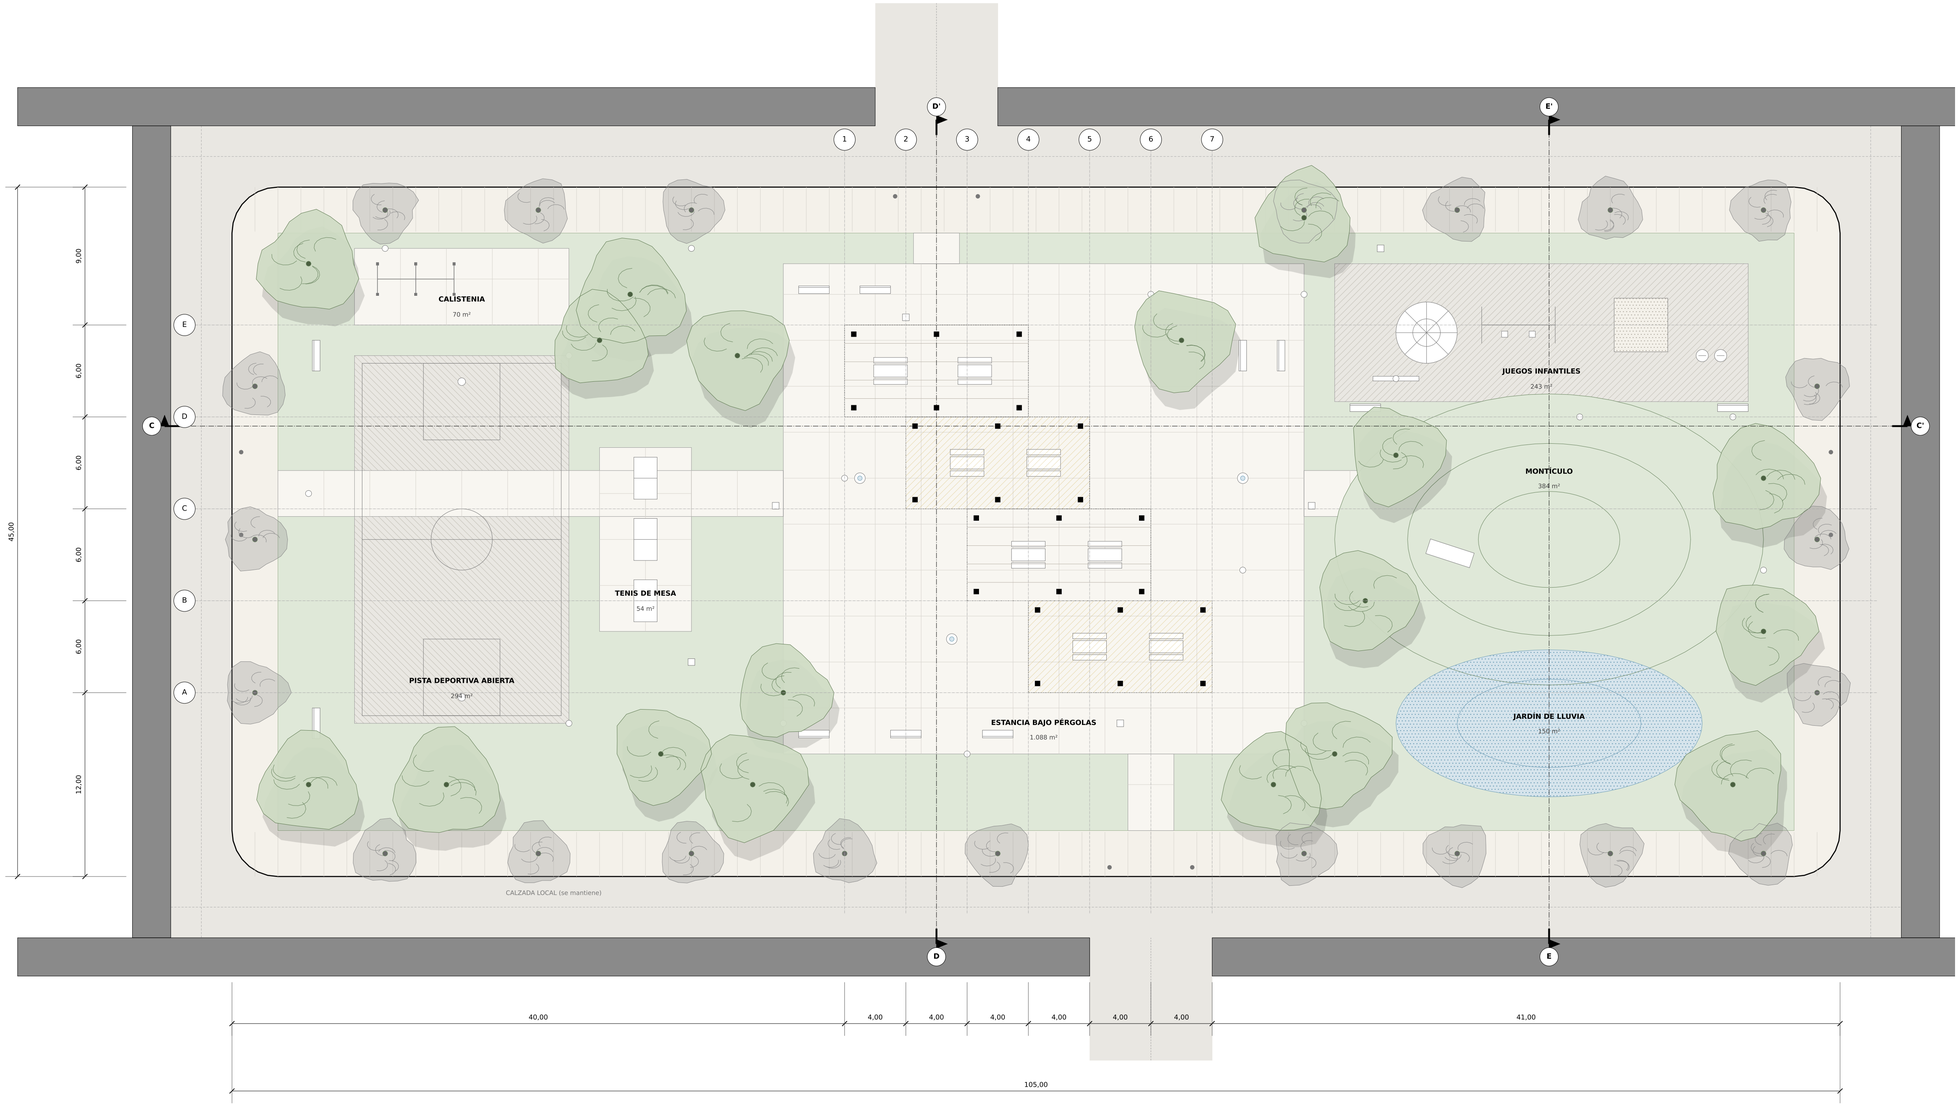

CUADRO DE SUPERFICIES · PLAZA 2

Estancia bajo pérgolas	1.088 m²
Tenis de mesa	54 m²
Pista deportiva abierta	294 m²
Calistenia	70 m²
Montículo	384 m²
Juegos infantiles	243 m²
Jardín de lluvia	150 m²
Pradera	1.439 m²
Recorridos de acceso (3 m)	138 m²
Acera perimetral conservada y renovada	864 m²
TOTAL PARCELA (intervención)	**4.725 m²**


Superficie cubierta por pérgolas: 288 m² (6 % de la parcela)

Arbolado: 22 ejemplares existentes conservados + 18 nuevos

Pérgolas: 4 cubiertas distintas (alturas 3,4-4,2 m)


LEYENDA

- Pradera / césped
- Pavimento duro (hormigón pulido, juntas 3 m)
- Juegos: pavimento amortiguador continuo
- Pavimento deportivo
- Jardín de lluvia (cota -0,45)
- Pérgola con lamas (proyección, discontinuo)
- Pérgola con panel opaco (recogida de pluviales)
- Arbolado existente que se conserva
- Fachada de manzana colindante (existente)
- Pilar de pérgola RHS 200x200x8 (nuevo)
- Luminaria / bolardo (gris relleno) / fuente

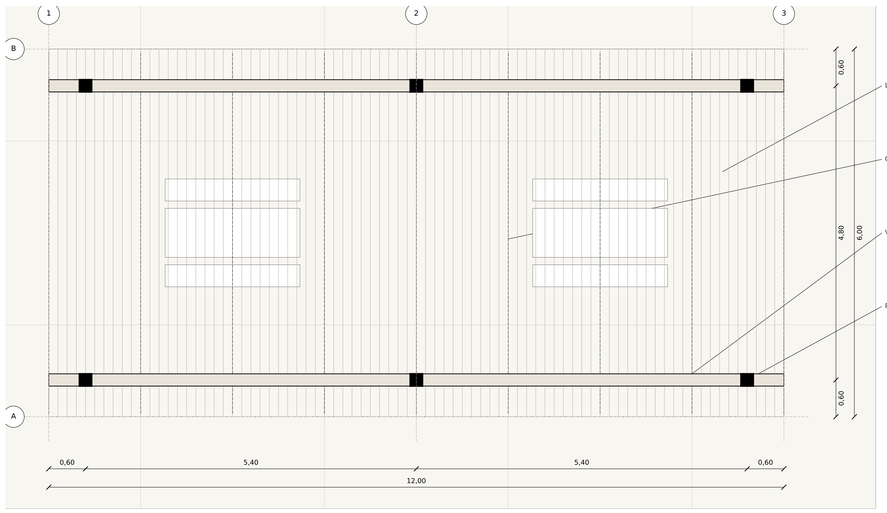

MÓDULO TIPO DE PÉRGOLA 12 x 6 m

E 1:50 · estructura de acero, retícula de ejes 1-3 / A-B

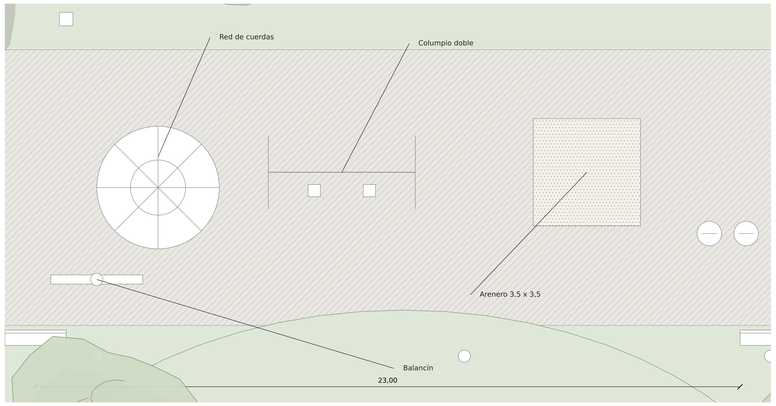

ZONA DE JUEGOS INFANTILES

E 1:100 · pavimento amortiguador continuo

Orientación supuesta: norte arriba; sol de mediodía al norte (hemisferio sur).

Terreno llano (≤0,5 %). Cotas en metros. Ejes de pérgolas: 1-n / A-n.

CASO_010 · PROPUESTA A Planta de Plaza 2 · nivel 0 (calle)	Plano **P02**	
Anteproyecto · Dos plazas de barrio	Escala 1:200	Lámina P02