



SECCIÓN LONGITUDINAL A-A' · PLAZA 1


E 1:200 · corte por el eje de pilares de pérgola; en proyección, mobiliario, juegos y arbolado

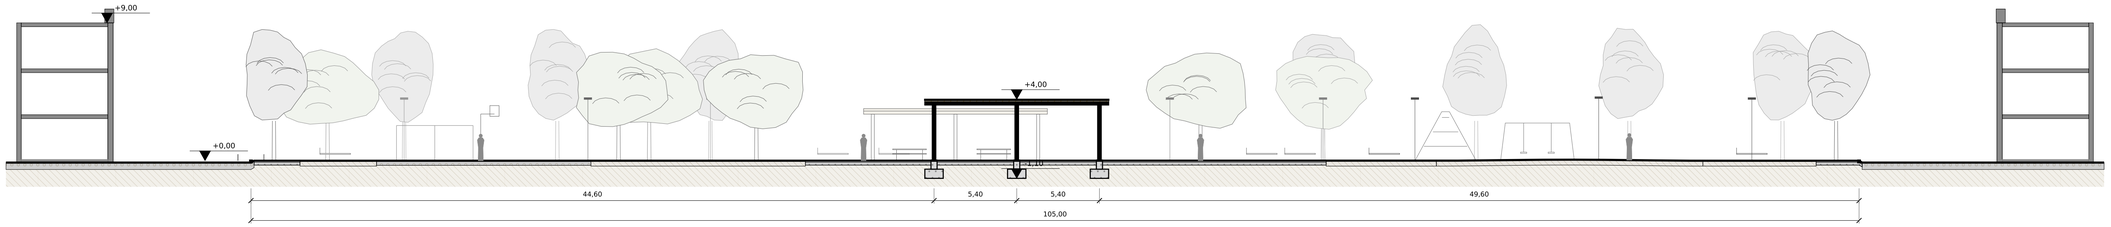

SECCIÓN LONGITUDINAL C-C' · PLAZA 2

E 1:200 · corte por el eje de pilares de pérgola; en proyección, mobiliario, juegos y arbolado

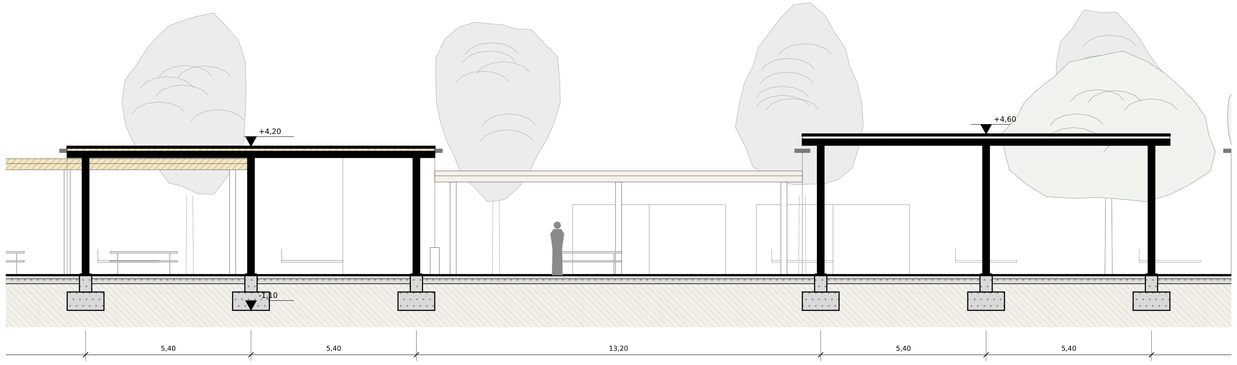

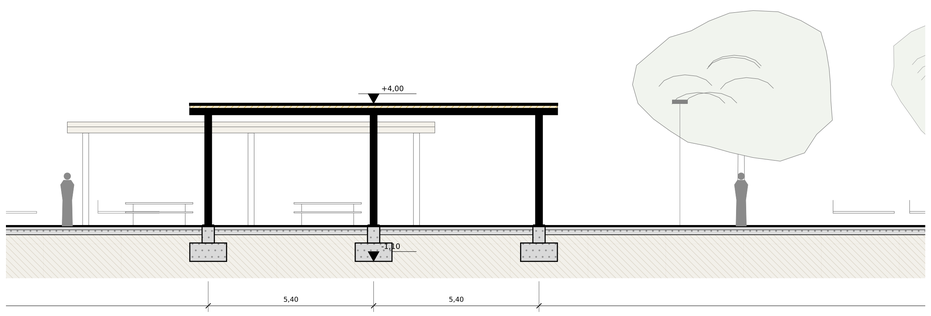


AMPLIACIÓN A-A' · ZONA DE PÉRGOLAS (PLAZA 1)

E 1:100

AMPLIACIÓN C-C' · ESCALERA DE PÉRGOLAS (PLAZA 2)

E 1:100

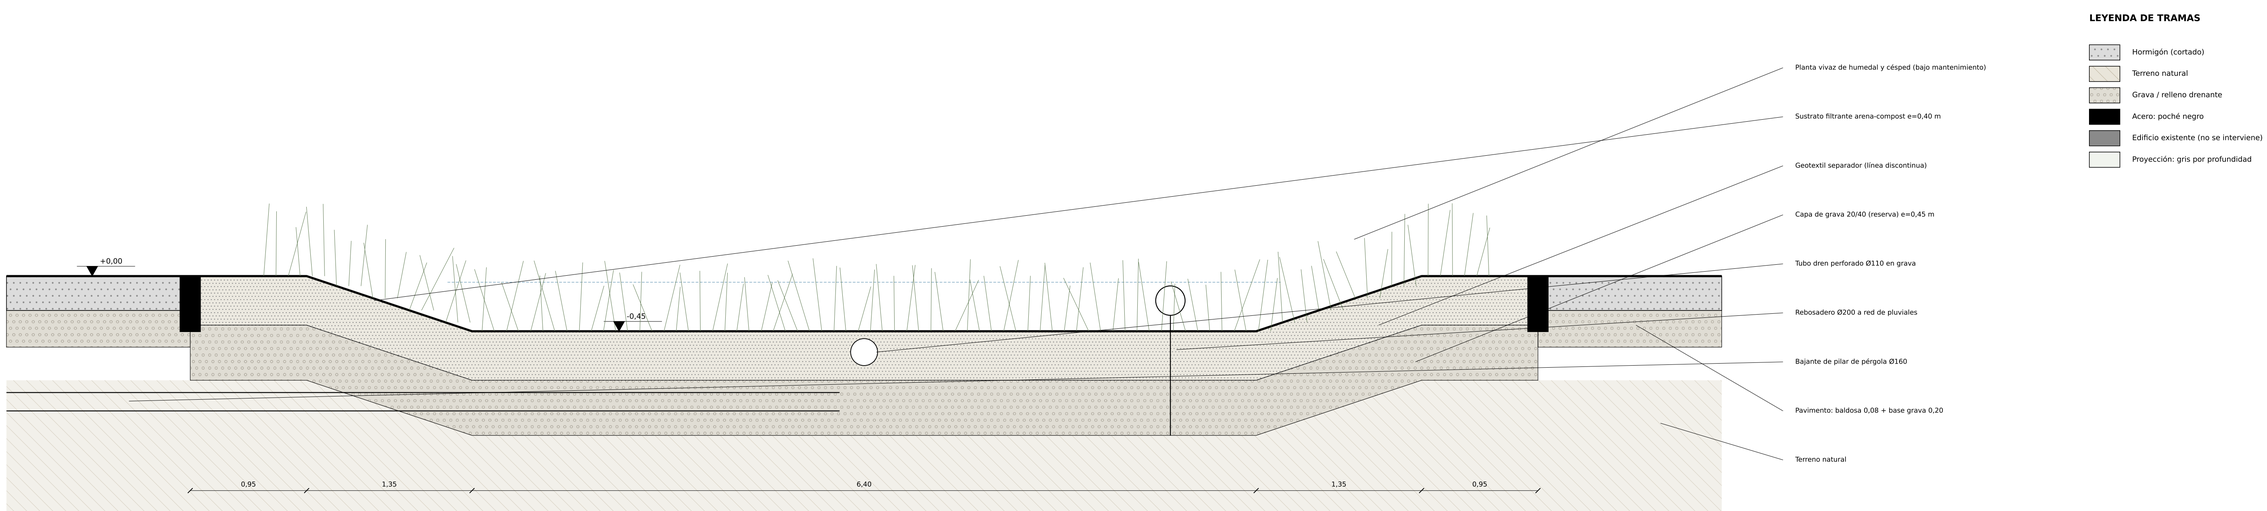

DETALLE JARDÍN DE LLUVIA · SECCIÓN

E 1:25 · retención y laminación de pluviales de pérgolas y pavimentos

CASO_010 · PROPUESTA A Secciones longitudinales A-A' (Plaza 1) y C-C' (Plaza 2)	Plano **S01**	
Anteproyecto · Dos plazas de barrio	Escala 1:200 · 1:100 · 1:25	Lámina S01