


PLAZA 2 · PLANTA GENERAL
E 1:200

0 1 2 5 10 20 m

CUADRO DE SUPERFICIES

1	Juegos 3-12 años (caucho)	400,0 m²
2	Calistenia y juego juvenil	224,0 m²
3	Pista de bochas / petanca	108,0 m²
4	Mesas de ping-pong bajo techo	128,0 m²
5	Prado arbolado O (pícnic)	1355,0 m²
	(incluye 1 · juegos en el prado O)	
6	Prado E	428,5 m²
7	Banda diagonal: sala bajo techos	540,0 m²
8	Plataformas, paseos y aceras interiores	1110,4 m²
	SUPERFICIE PLAZA 2	4694,0 m²
	Techos-pérgola (9 ud.)	378,0 m²
	Árboles nuevos / a mantener (ud.)	36

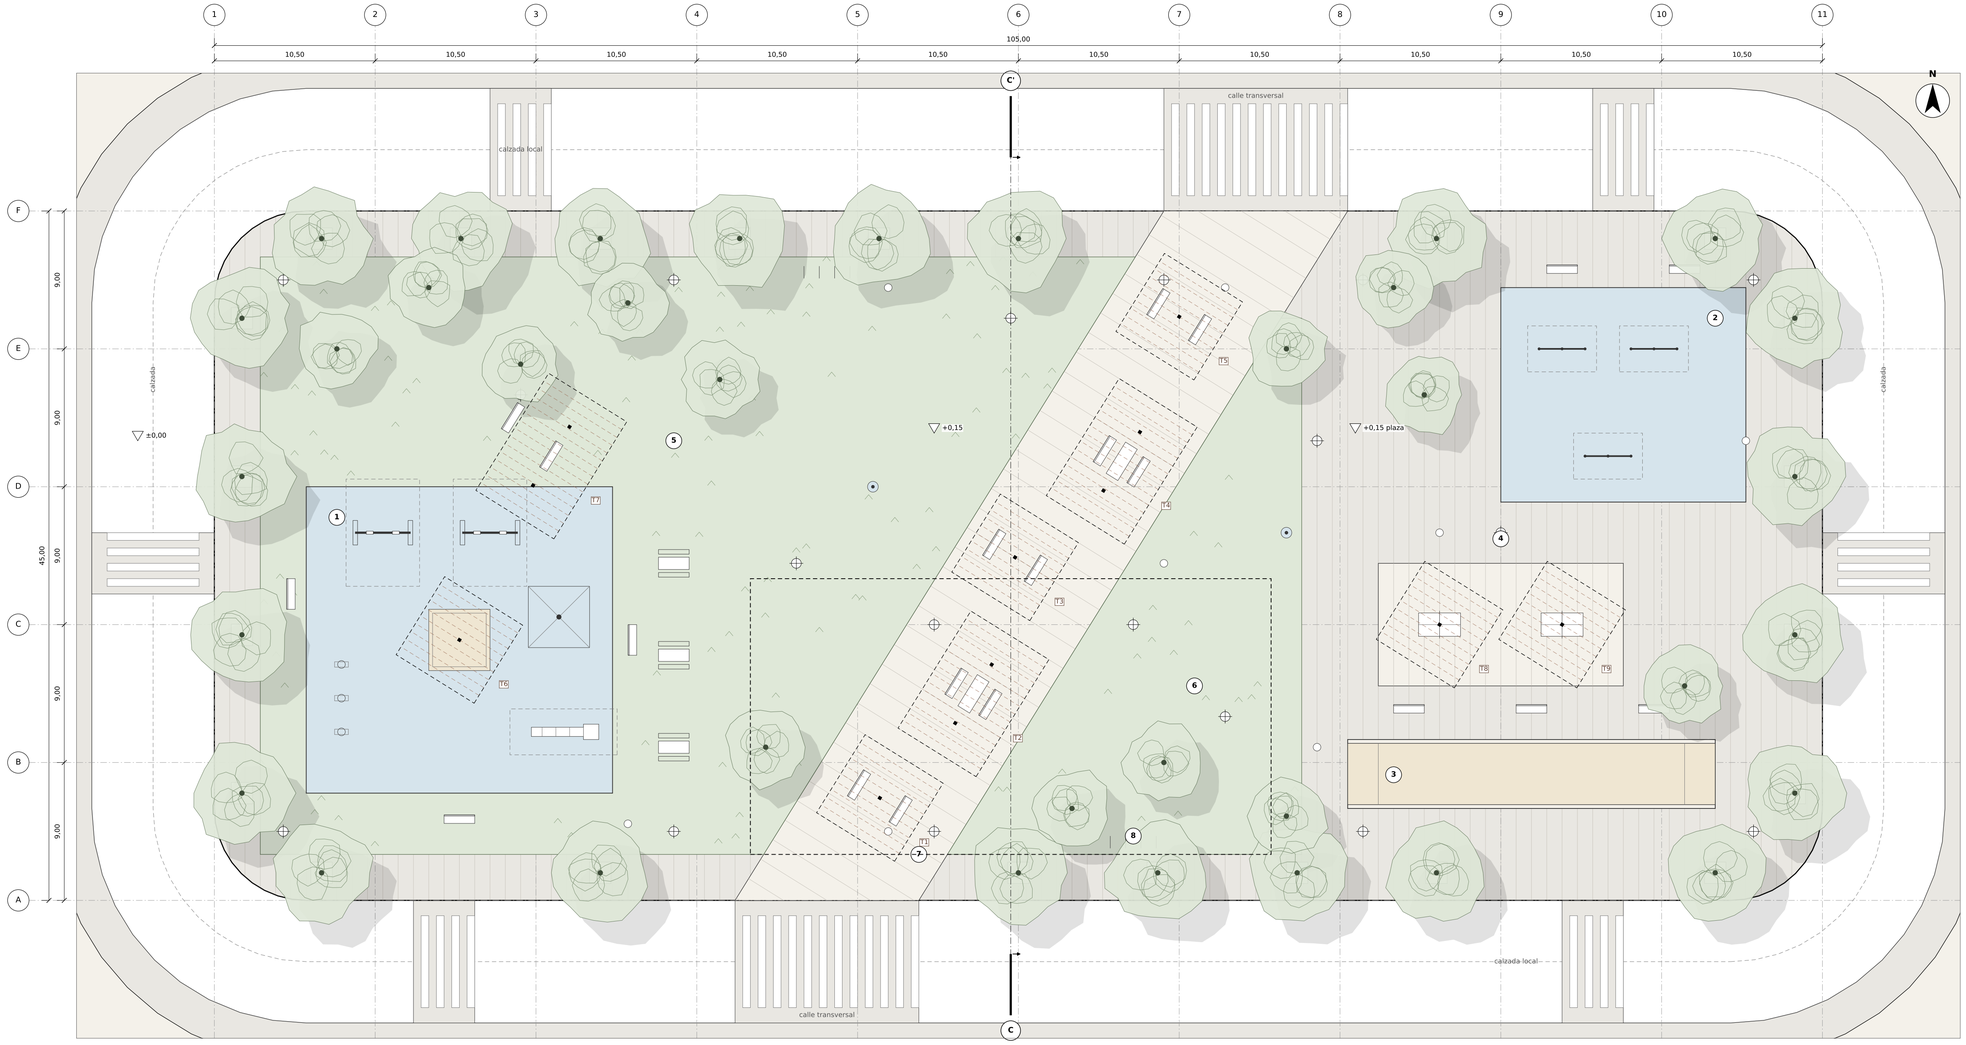

AMPLIACIÓN · BANDA DIAGONAL Y TECHOS T1-T2
E 1:100

0 1 2 5 m

LEYENDA

- Pavimento de hormigón fratasado en bandas (despiece 1,0 m)
- Pavimento de piezas / pista / banda de estancia
- Pradera de bajo riego y arbustivas
- Caucho continuo de seguridad (juegos)
- Techo-pérgola en proyección (lamas sobre plano de corte)
- Pilar metálico cortado
- Báculo de iluminación LED 4,5-6 m
- Árbol (copa, alcorque y sombra a 45°)

TECHOS-PÉRGOLA

T1 6 x 6 m h 3,40 m	tipo A
T2 9 x 6 m h 4,20 m	tipo B
T3 6 x 6 m h 4,80 m	tipo A
T4 9 x 6 m h 3,80 m	tipo B
T5 6 x 6 m h 4,40 m	tipo A
T6 6 x 6 m h 3,40 m	tipo A
T7 9 x 6 m h 4,00 m	tipo B
T8 6 x 6 m h 3,60 m	tipo A
T9 6 x 6 m h 4,20 m	tipo A

CASO_010 · PROPUESTA C	ESCALA	LÁMINA Anteproyecto
Plaza 2 · Planta general y ampliación	**E 1:200 / 1:100**	**P02**