
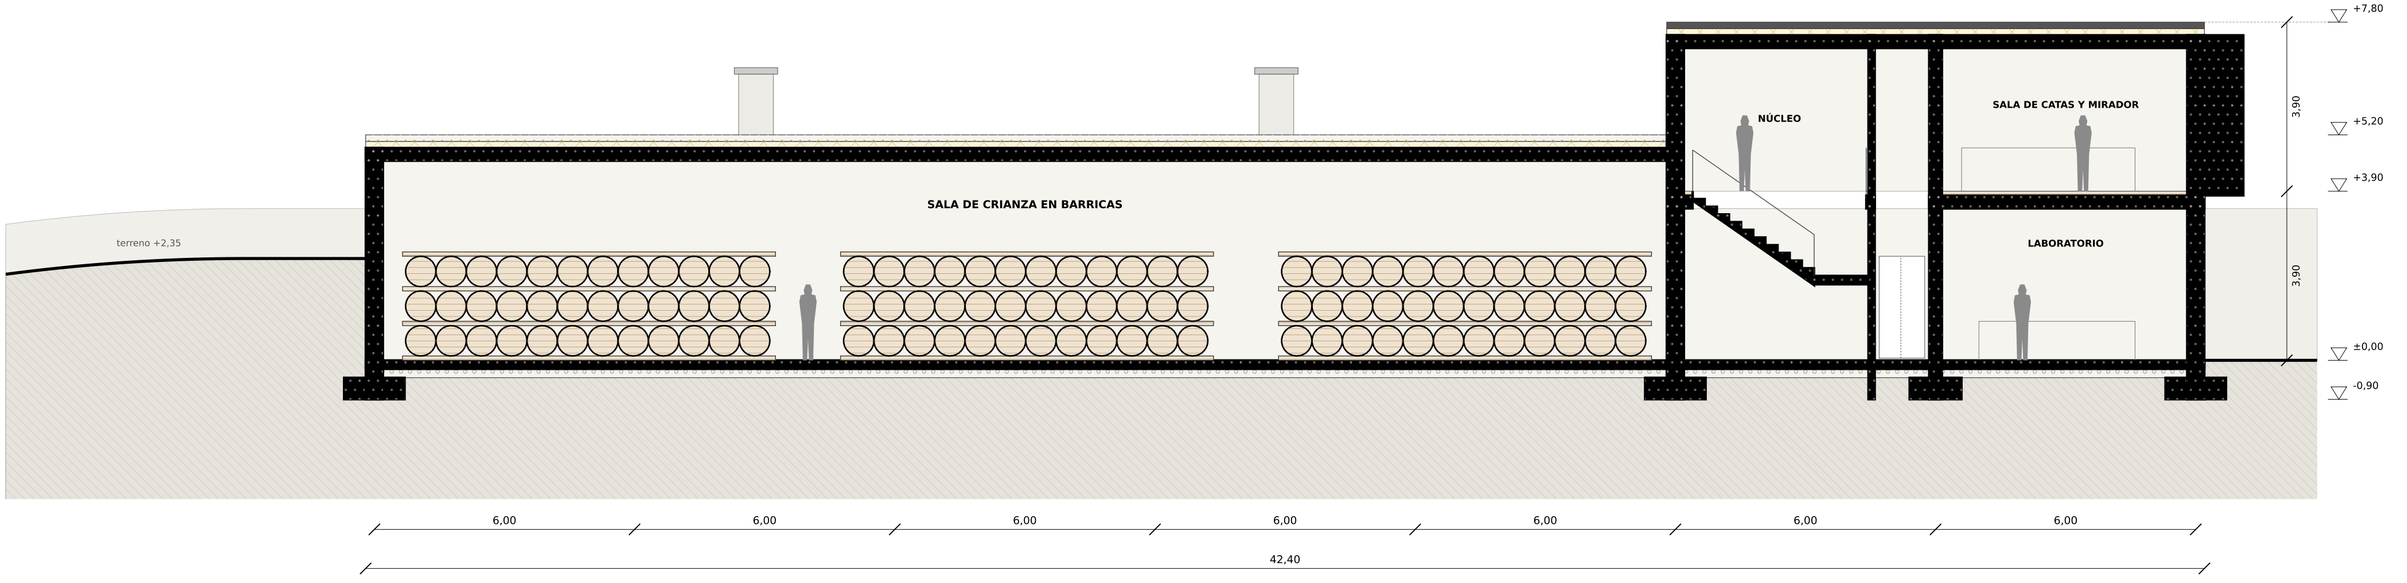


SECCIÓN LONGITUDINAL A-A'

E 1:100

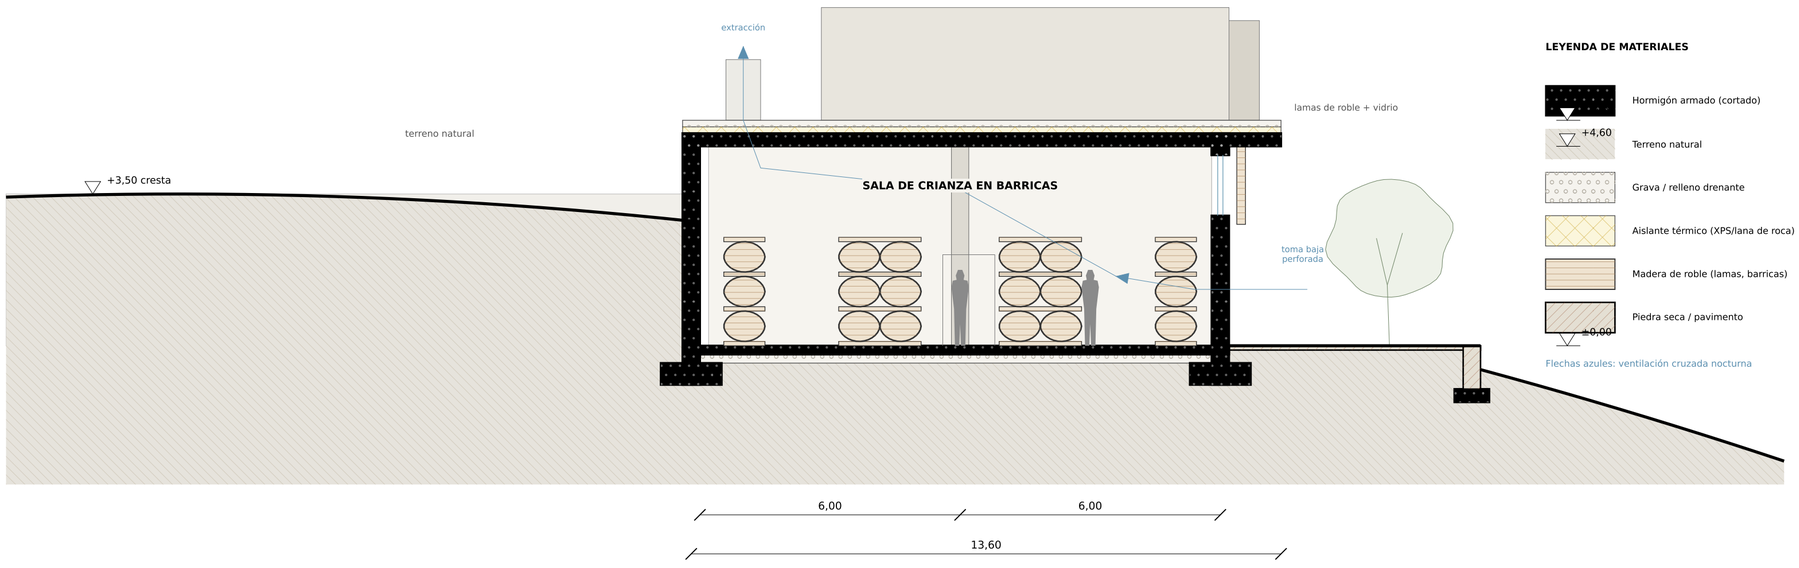

LEYENDA DE MATERIALES

- Hormigón armado (cortado)
- Terreno natural (+4,60)
- Grava / relleno drenante
- Aislante térmico (XPS/lana de roca)
- Madera de roble (lamas, barricas)
- Piedra seca / pavimento (±0,00)

Flechas azules: ventilación cruzada nocturna

SECCIÓN TRANSVERSAL B-B'

E 1:100

CASO_011 · PROPUESTA A	**E 1:100** **S01**
Secciones longitudinal A-A' y transversal B-B'	Anteproyecto