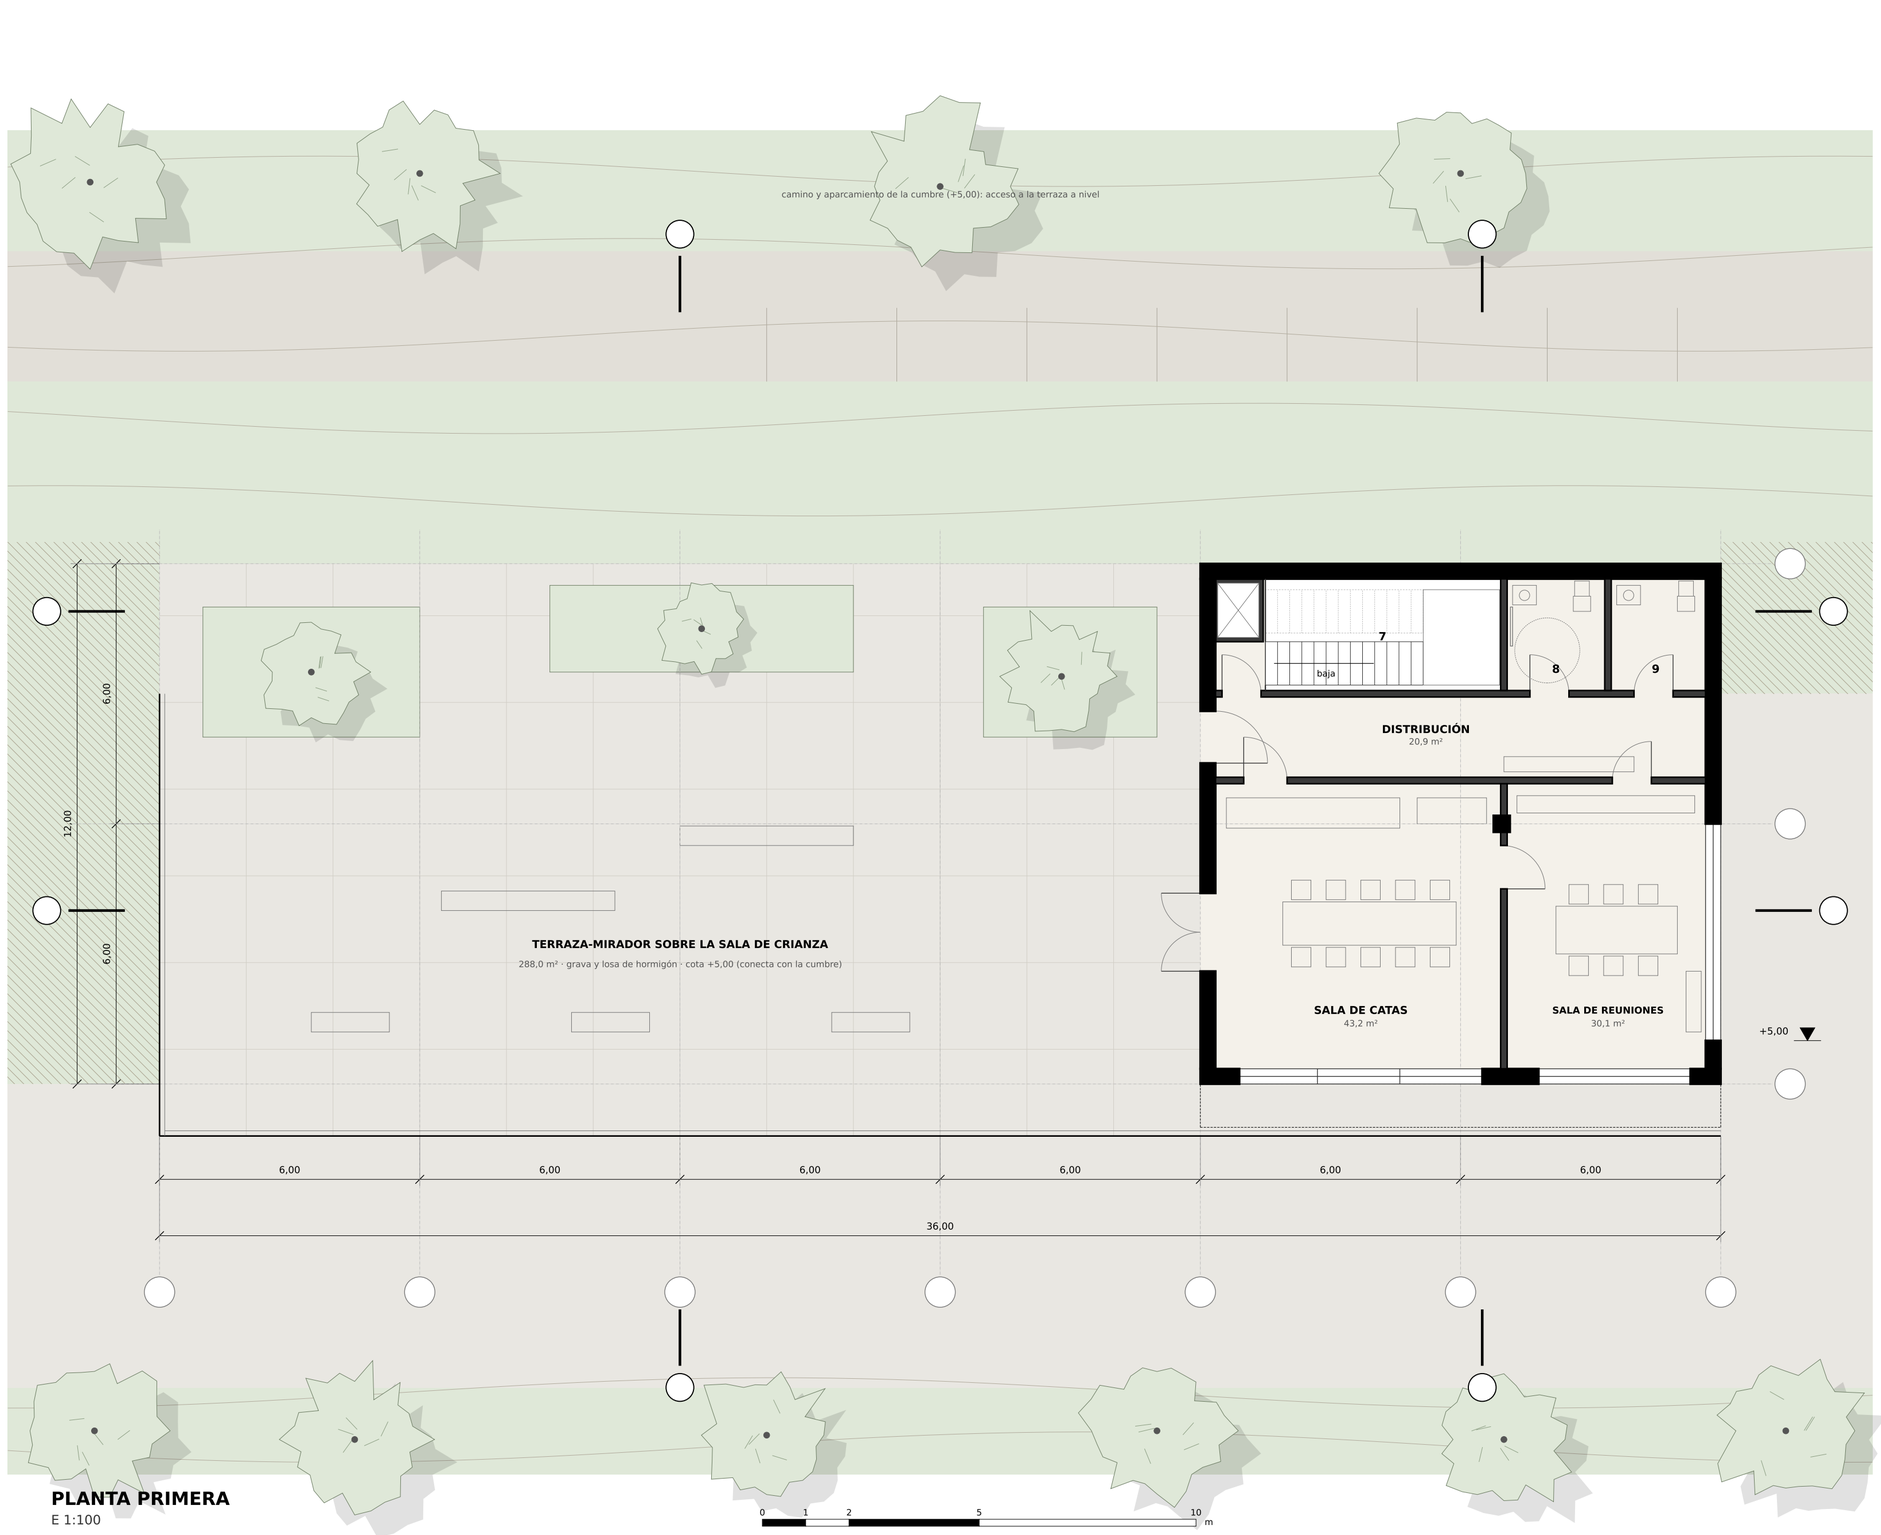


PLANTA PRIMERA
E 1:100

N

CUADRO DE SUPERFICIES · P. PRIMERA

1 Sala de catas	43,2 m²
2 Sala de reuniones	30,1 m²
4 Distribución	20,9 m²
7 Escalera y ascensor	16,9 m²
8 Aseo adaptado	5,8 m²
9 Aseo	5,6 m²
Superficie útil planta primera	122,5 m²

DATOS

Construida planta primera	144,0 m²
Construida total (P0+P1)	576,0 m²
Terraza cubierta transitable	288,0 m²

Muro estructural / obra nueva
Tabique
Por encima del plano de corte
Vegetación / terreno
Pavimento exterior

CASO_011 · PROPUESTA B Sala de crianza en barricas	**Lámina P02**	
Planta primera (cota +5,00)	Escala 1:100	Anteproyecto DIN A2