
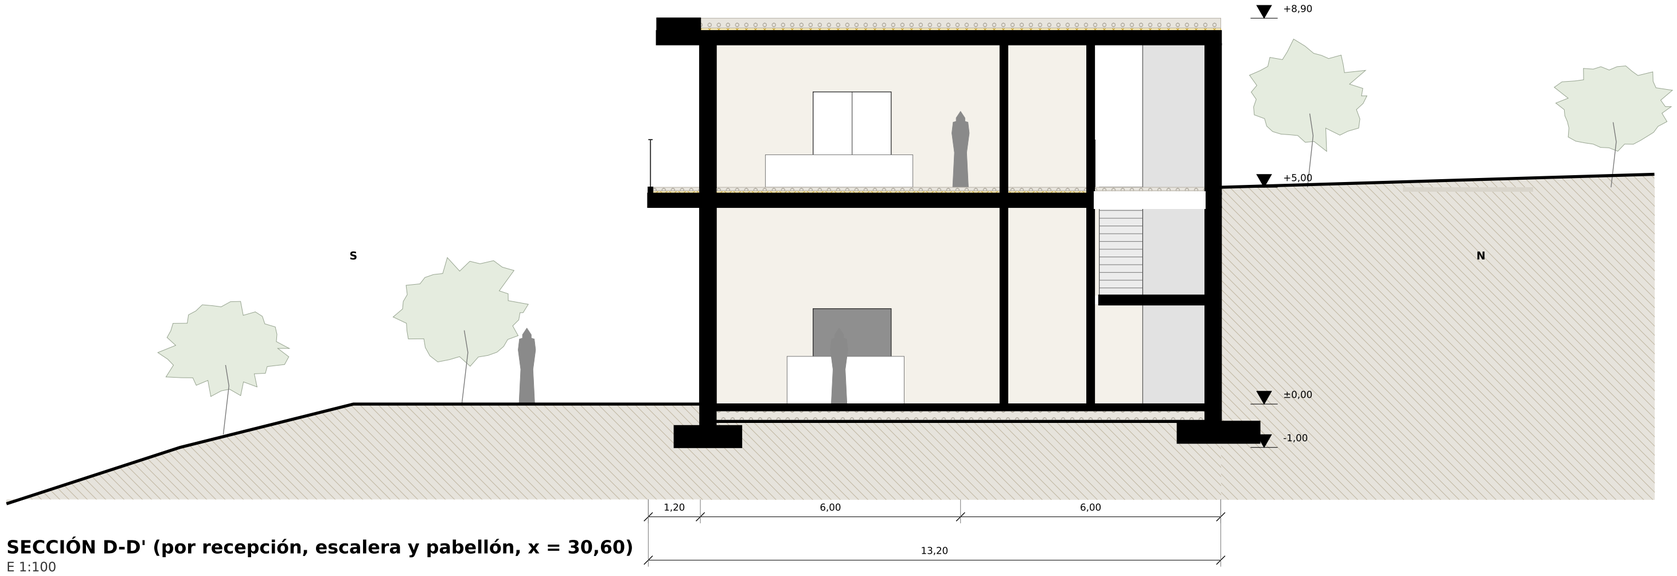


SECCIÓN D-D' (por recepción, escalera y pabellón, x = 30,60)
E 1:100

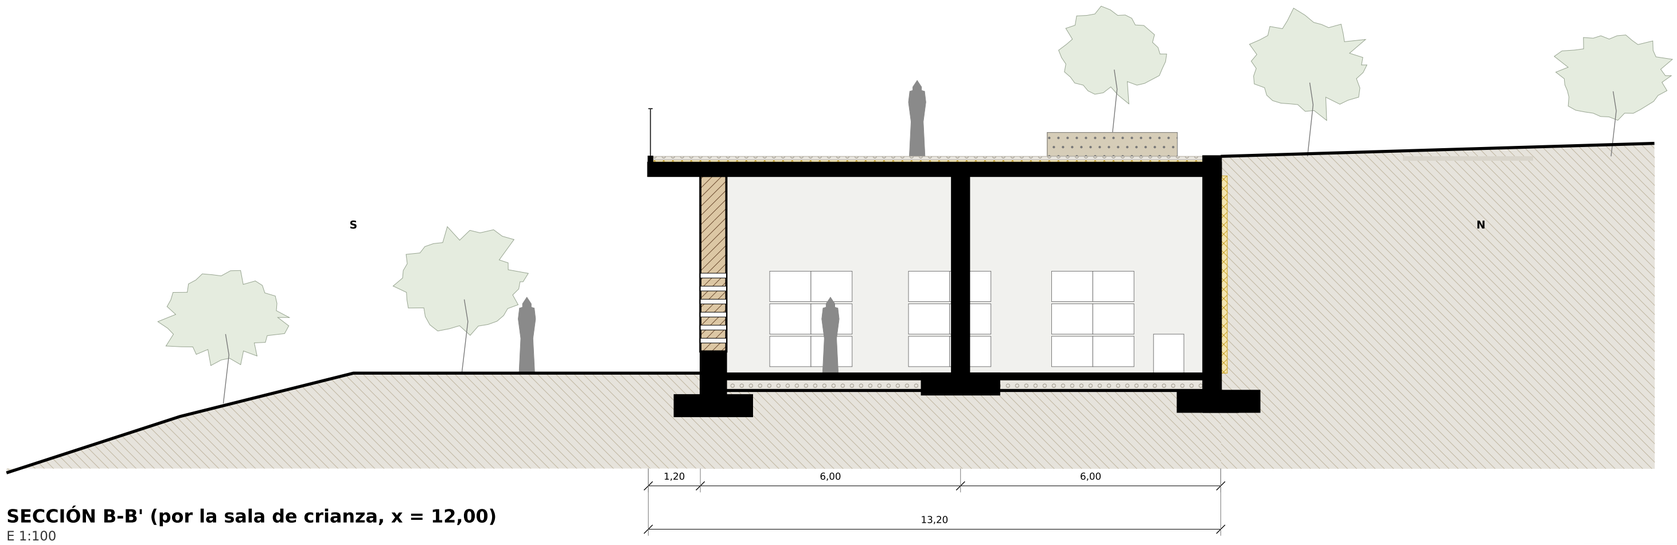

SECCIÓN B-B' (por la sala de crianza, x = 12,00)
E 1:100

MATERIALES

- Hormigón armado
- Tapial (tierra apisonada)
- Aislante térmico
- Grava / relleno
- Terreno natural
- Vidrio

0 1 2 5 10 m

CASO_011 · PROPUESTA B Sala de crianza en barricas	**Lámina S02**	
Secciones transversales B-B' y D-D'	Escala 1:100	Anteproyecto DIN A2