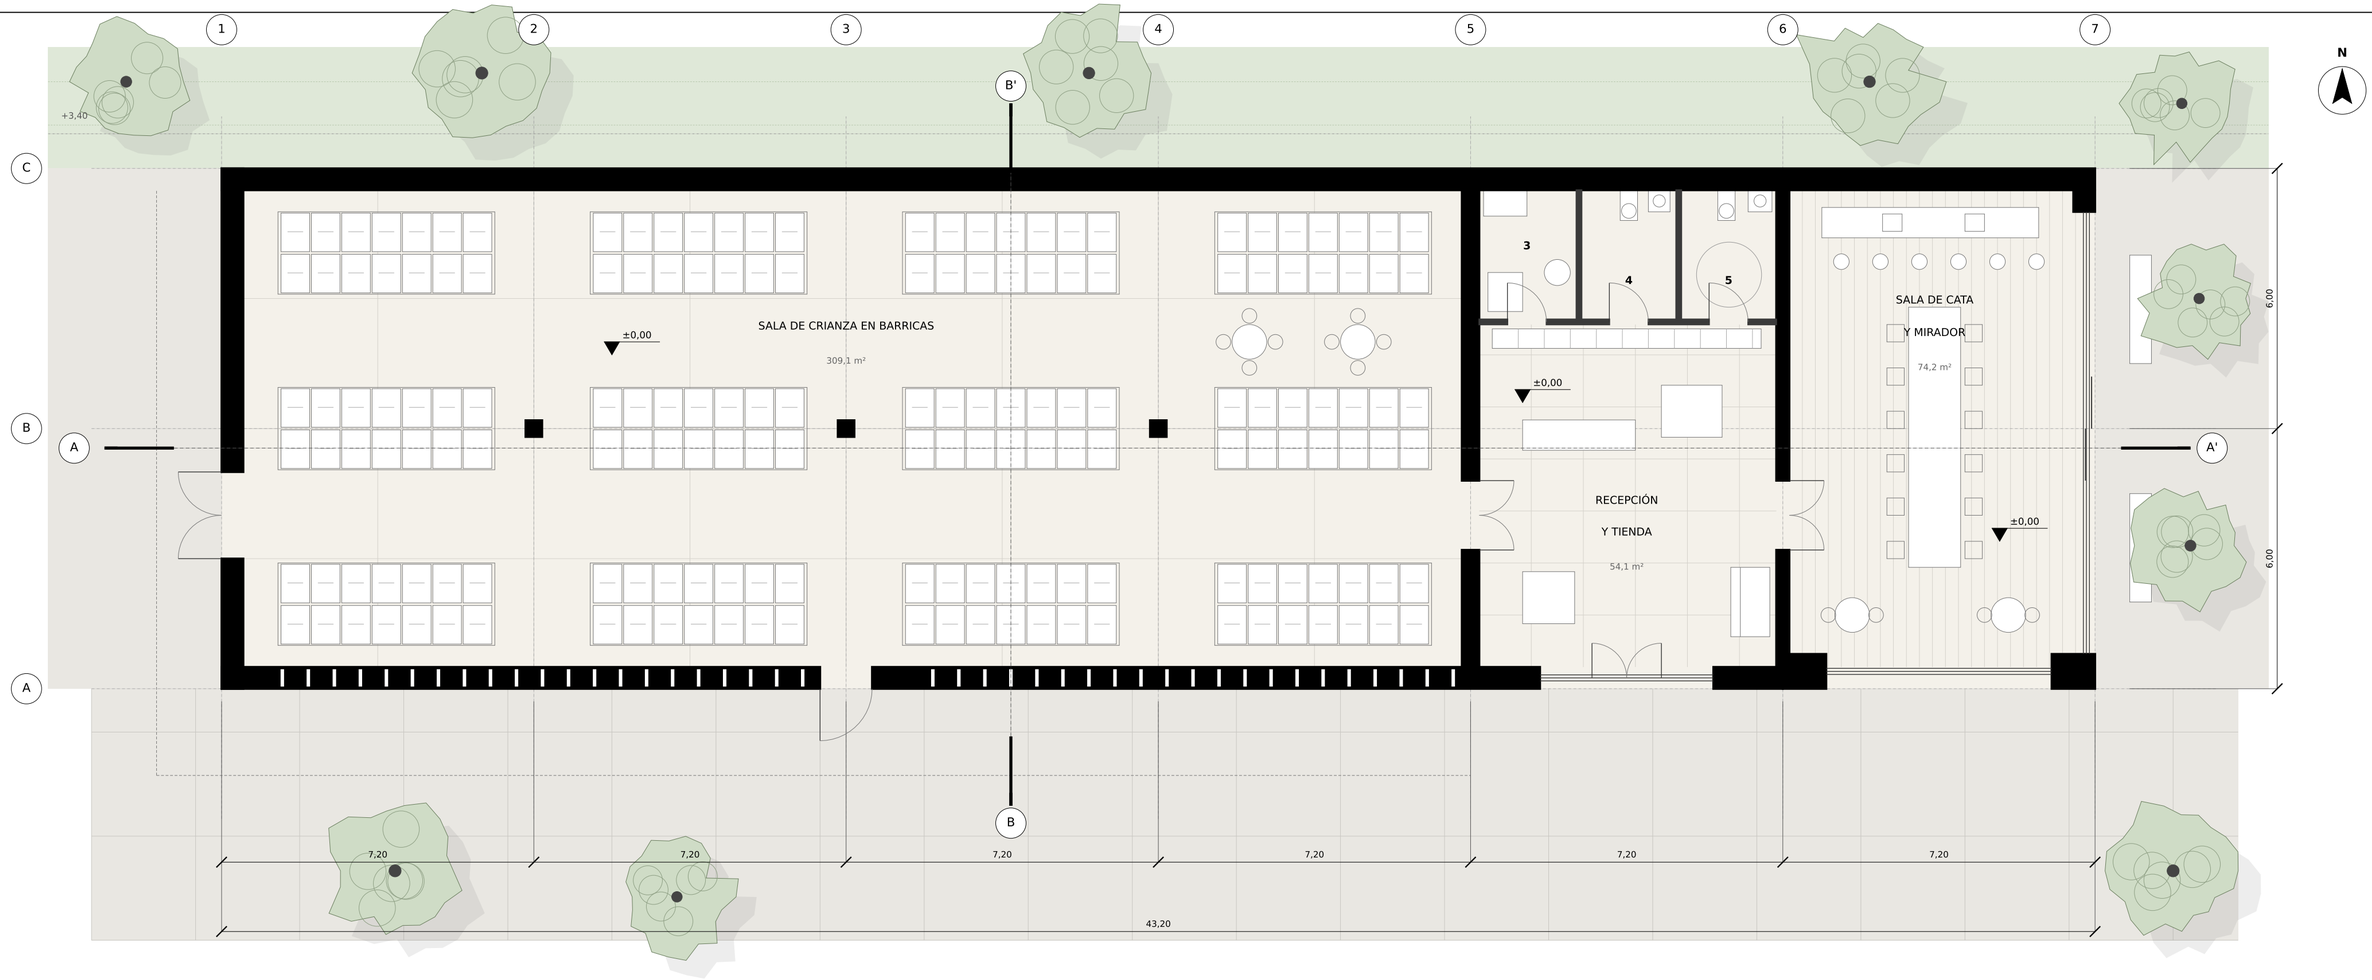


PLANTA BAJA

E 1:100

LEYENDA

- Muro de tierra / hormigón (cortado)
- Tabique
- Mobiliario / barricas
- Cubierta y lamas sobre el corte

A-A' / B-B': líneas de sección (S01, S02)


Puntos blancos en el muro sur: tubos de ventilación

Cota ±0,00 = solera de la sala de crianza

CUADRO DE SUPERFICIES ÚTILES

1	Sala de Crianza en Barricas	309,1 m²
2	Recepción y Tienda	54,1 m²
3	Cuarto Técnico	6,7 m²
4	Aseo	6,5 m²
5	Aseo Adapt.	6,5 m²
6	Sala de Cata y Mirador	74,2 m²
Superficie útil		**457,2 m²**
Superficie construida (ejes)		**518,4 m²**

Barricas de 225 l: 168 por nivel x 3 = 504 ud.

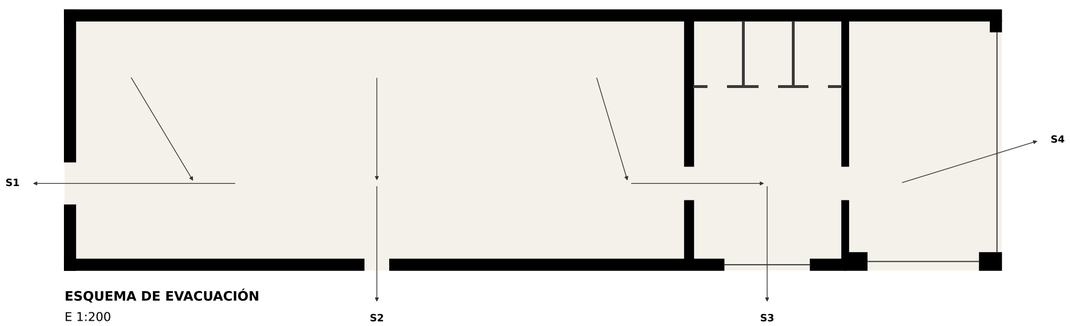

ESQUEMA DE EVACUACIÓN

E 1:200

S1-S4: salidas al exterior (planta única, sin escaleras). Recorrido a salida ≈ 12 m (< 25 m).

Ocupación: sala 1 pers./40 m² + cata 1/2 m² ≈ 45 pers.; anchos ≥ 1,0 m.

CASO_011 · PROPUESTA C	**P01**
Planta baja (nivel ±0,00)	E 1:100 · Anteproyecto