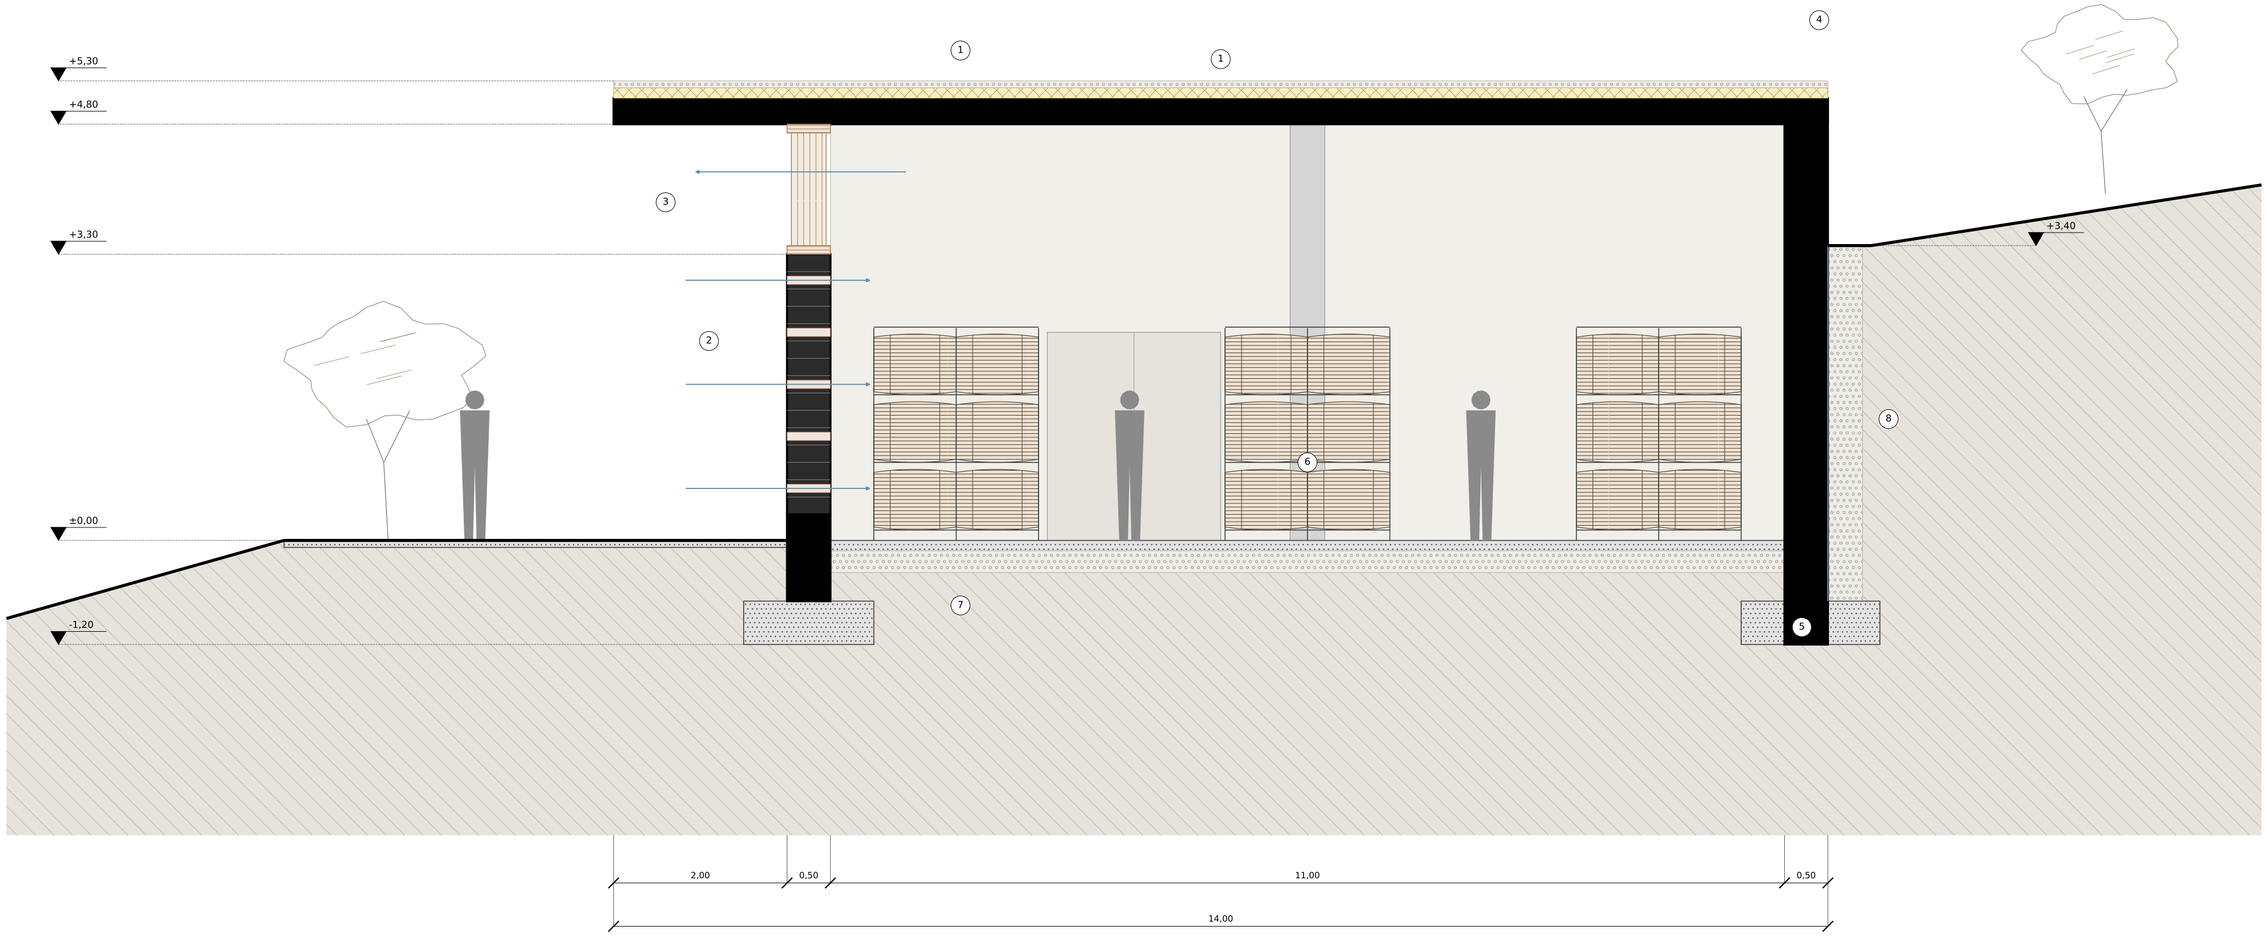



## SECCIÓN TRANSVERSAL B-B'

E 1:50

0 1 2 5 10 m

### LEYENDA

1 Cubierta invertida: grava 8 cm · XPS 12 cm · lámina EPDM · losa maciza de hormigón 30 cm (vuelo 2,00 m)

2 Muro de tierra apisonada estabilizada, e = 50 cm, sobre zócalo de hormigón; tubos cerámicos Ø 10 cm cada 60 cm

3 Celosía de lamas verticales de madera de iroko (clerestorio) con malla antiinsectos; salida de aire caliente

4 Muro de contención de hormigón armado e = 50 cm, lámina drenante, grava y tubo dren; tierra hasta +3,40

5 Zapata corrida 1,50 x 0,50 m (σadm 0,20 MPa supuesta); cota de cimentación -1,20

6 Barricas de roble de 225 l en bastidor de acero, 3 alturas (máx. 2,45 m) · pasillos de 2,15 m

7 Solera: hormigón pulido 12 cm + grava 25 cm sobre terreno · 8 Aljibe/ drenaje perimetral en el trasdós

Flechas azules: ventilación cruzada nocturna (entrada baja por tubos cerámicos, salida alta por lamas).

| | |
|---|---|
| **CASO_011 · PROPUESTA C** | **S02** |
| Sección transversal B-B' | E 1:50 · Anteproyecto |