


ALZADO SUR

E 1:100

0 1 2 5 10 m

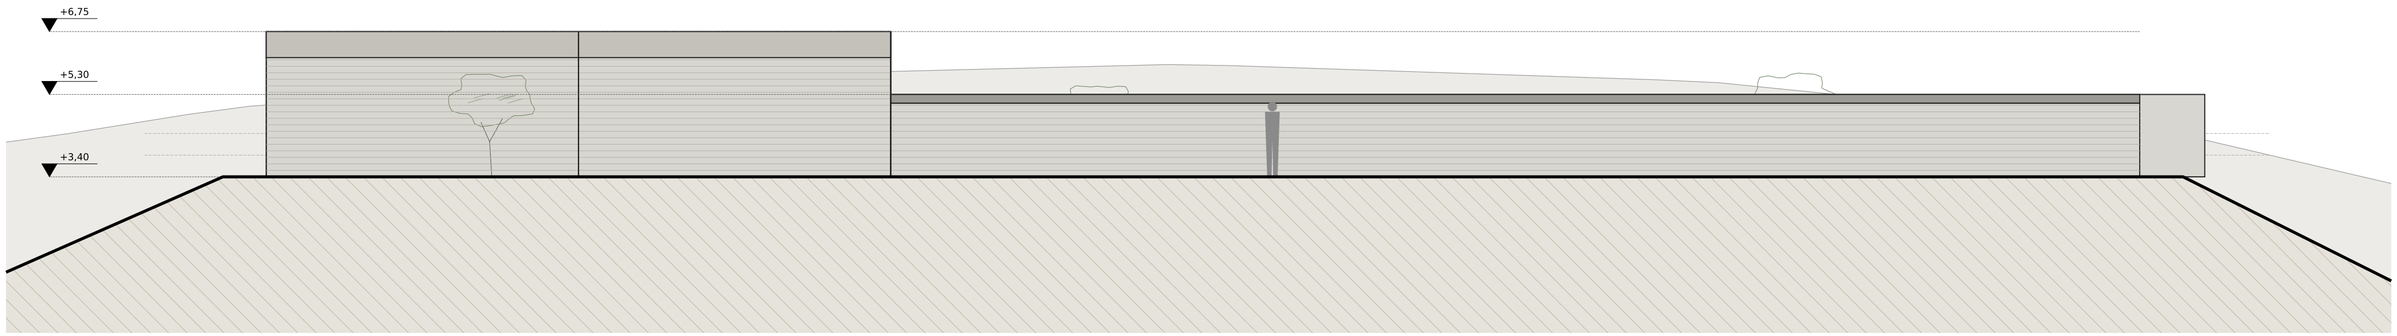

ALZADO NORTE

E 1:100

MATERIALES DE FACHADA

- Tierra apisonada estabilizada, e = 50 cm, capas de 20 cm; tubos cerámicos Ø 10 cm (celosía de ventilación)
- Lamas verticales de iroko 4 x 12 cm cada 30 cm en clerestorio (sólo 2 bandas de 6 m)
- Hormigón visto con encofrado de tabla de 15 cm (pabellones, marcos y peto)
- Vidrio doble bajo emisivo con carpintería de acero en perfil delgado
- Acero oxidado / pavonado: puertas de servicio y emergencia

Sombras arrojadas a mediodía de verano (altura solar ≈ 70°): el vuelo de 2,00 m protege el muro sur hasta ≈ +1,30.

CASO_011 · PROPUESTA C	S03
Alzados sur y norte	E 1:100 · Anteproyecto