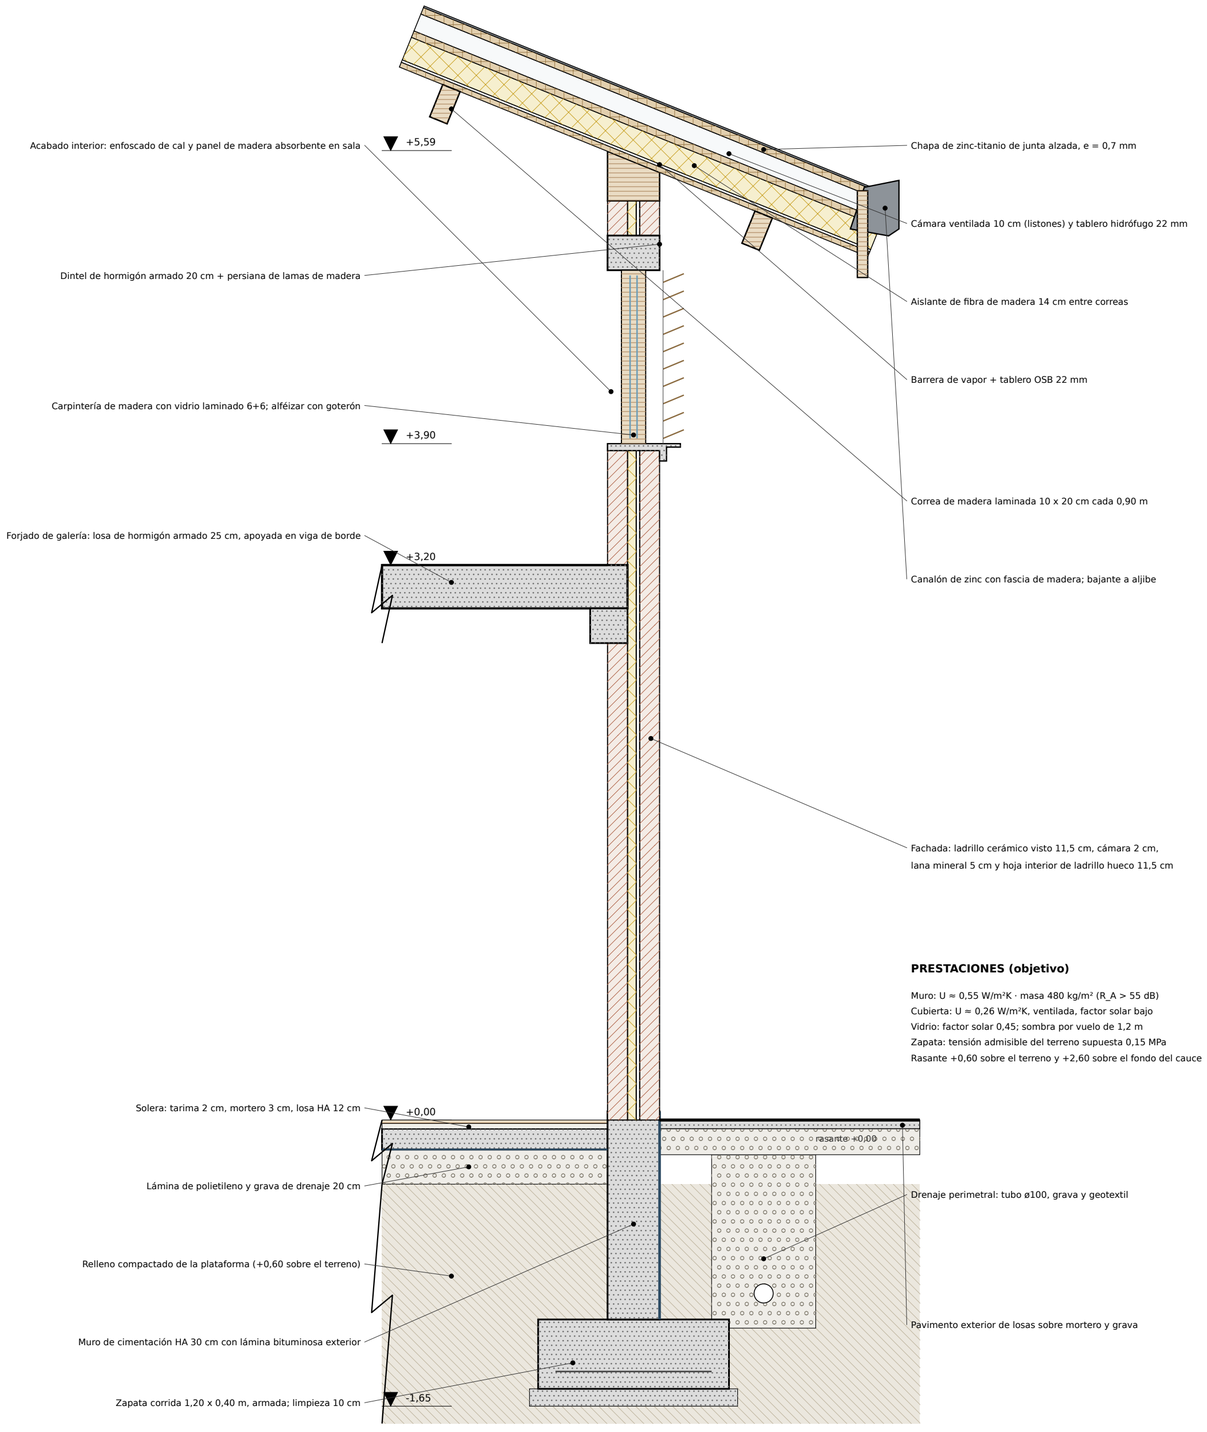


PRESTACIONES (objetivo)

Muro: U ≈ 0,55 W/m²K · masa 480 kg/m² (R_A > 55 dB)
Cubierta: U ≈ 0,26 W/m²K, ventilada, factor solar bajo
Vidrio: factor solar 0,45; sombra por vuelo de 1,2 m
Zapata: tensión admisible del terreno supuesta 0,15 MPa
Rasante +0,60 sobre el terreno y +2,60 sobre el fondo del cauce

SECCIÓN CONSTRUCTIVA · MURO ESTE DE LA SALA (EJE D)

E 1:25

Del cimiento a la cubierta, por A-A' (y = 27,00). Dimensiones en metros; capas rotuladas de exterior a interior.

CASO_012 · PROPUESTA A Anteproyecto	LÁMINA
SECCIÓN CONSTRUCTIVA · MURO ESTE DE LA SALA Escala 1:25	**D01**