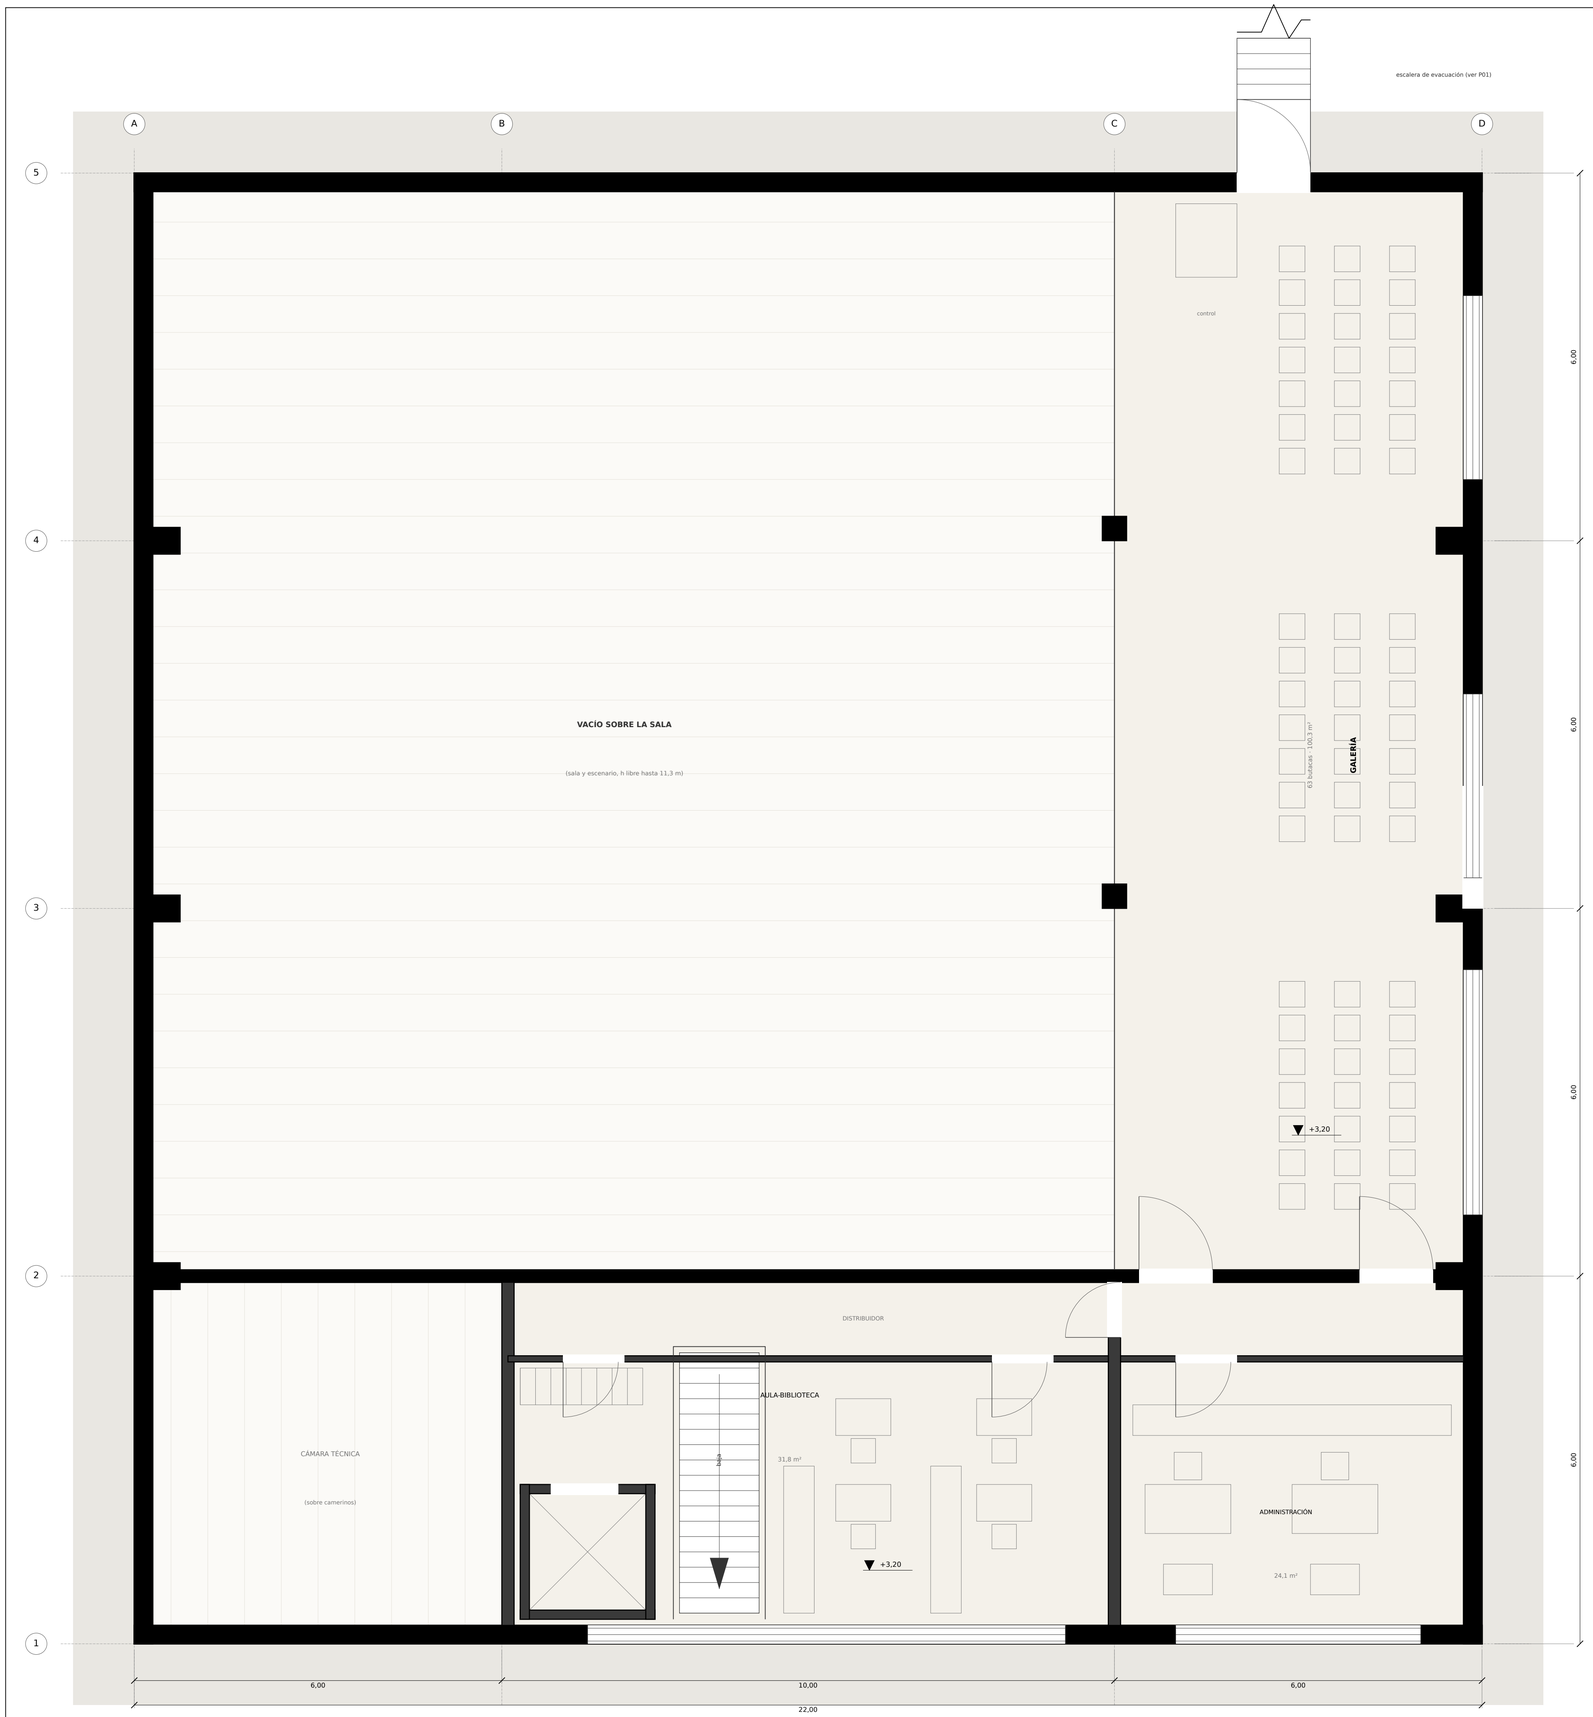

PLANTA PRIMERA (BLOQUE A)
E 1:50

N

0 1 2 5 10 m

CUADRO DE SUPERFICIES ÚTILES · PLANTA PRIMERA

19	Aula-biblioteca musical	31,8
20	Administración y profesores	24,1
21	Galería de la sala	100,3
	Distribuidor y vestíbulo superior	18,7
	Total útil planta primera	**174,9**

RESUMEN DEL PROYECTO

Superficie útil planta baja	823,3
Superficie útil planta primera	174,9
Total útil cerrado	998,2
Corredor ventilado + veranda (abiertos)	352,9
Superficie construida aprox. (incl. muros y 50 % veranda)	1.330

LEYENDA

- Muro portante de ladrillo (cortado)
- Tabique
- Interior
- Pavimento exterior
- Vegetación / césped
- Agua / jardín de lluvia
- Por encima del plano de corte

La planta primera solo existe en el bloque A (sobre el foyer y la galería).
El bloque B (escuela) es de una planta.
Escalera interior: 18 contrahuellas de 17,8 cm, huella 25 cm.

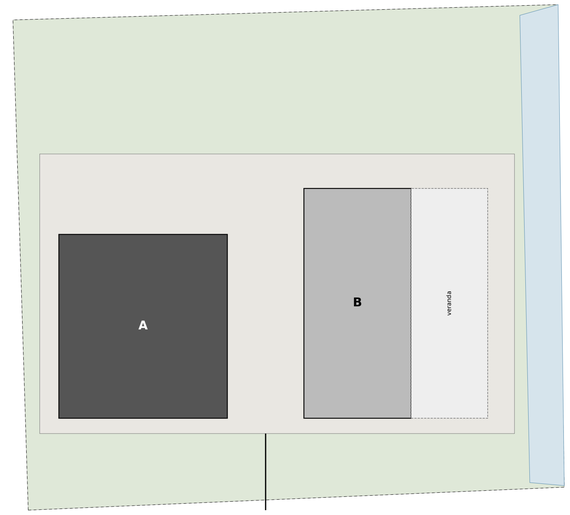

SITUACIÓN DE LA PLANTA PRIMERA (BLOQUE A)
E 1:400

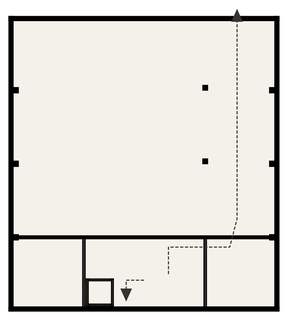

Esquema de evacuación: 2 salidas independientes
1: escalera interior (18 contrahuellas) y ascensor accesible
2: galería, puerta norte y escalera exterior de evacuación
Ocupación planta primera: 63 (galería) + 25 = 88 personas
Recorrido máximo < 25 m. Zona de refugio en la galería.

CASO_012 · PROPUESTA A Anteproyecto	LÁMINA
PLANTA PRIMERA Escala 1:50	**P02**