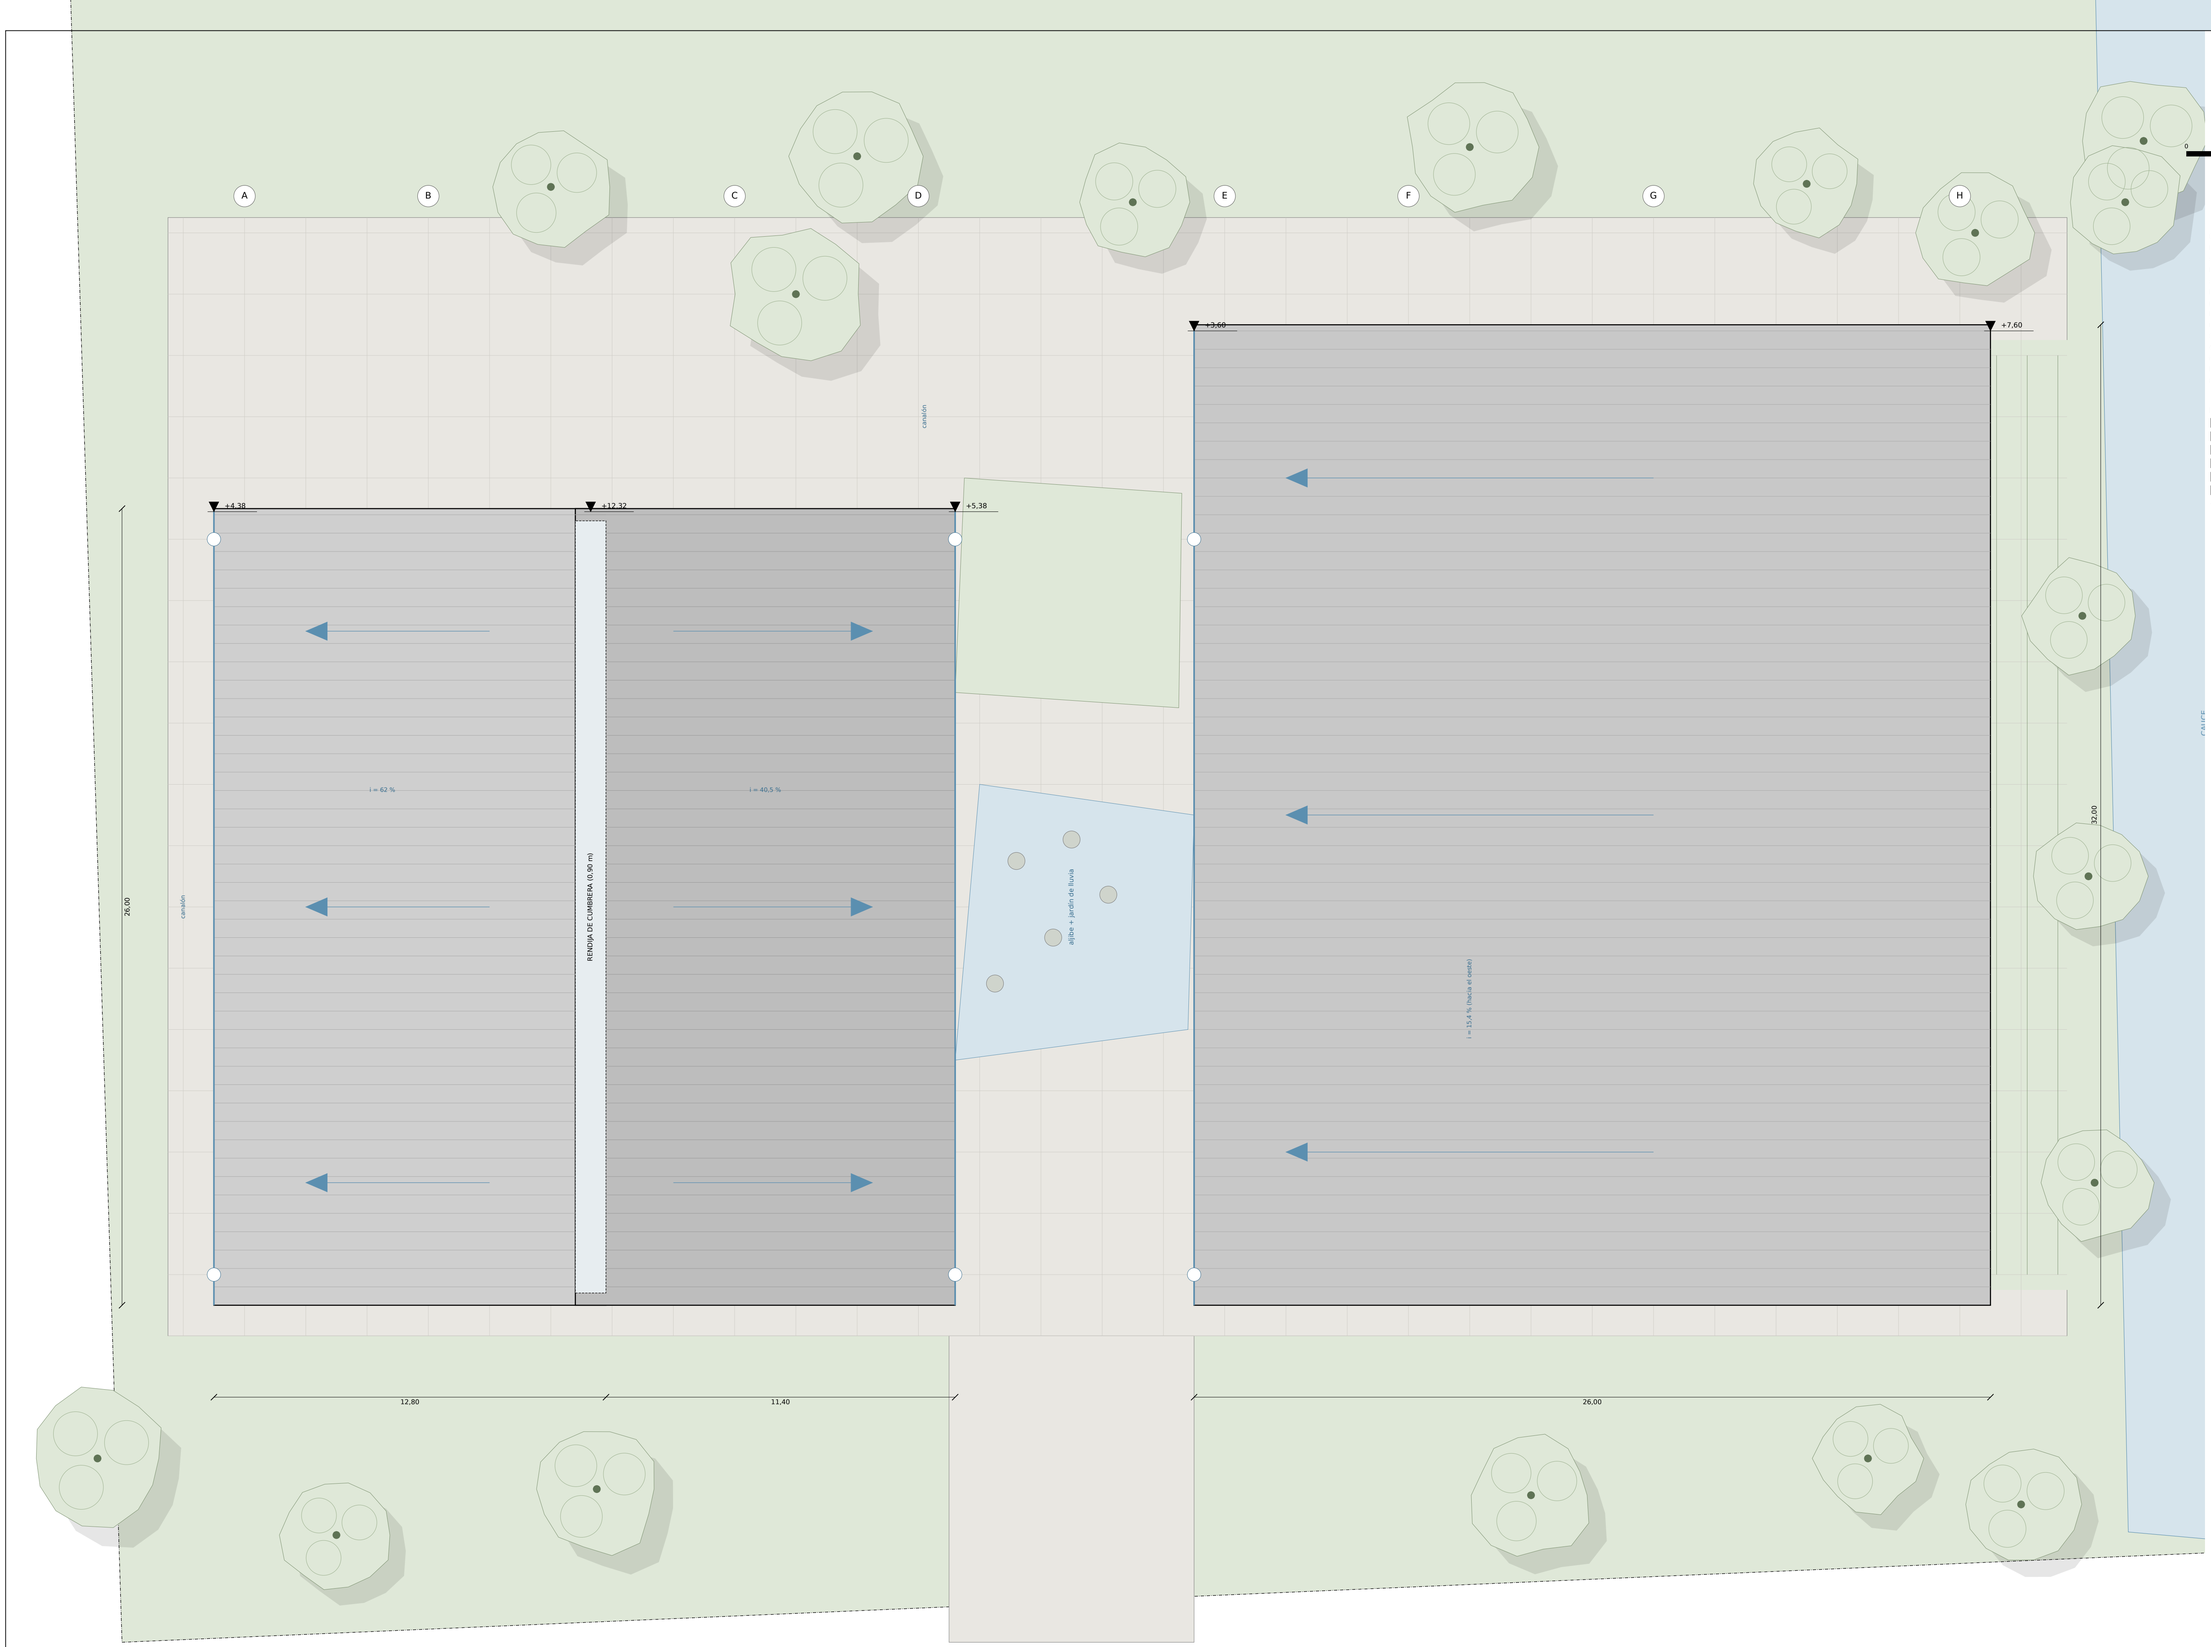


CUBIERTAS

Plano A-oeste: 12,8 x 26,0 m, i = 62 % (31,8°),
cota 4,38 a 12,32 (cumbrera).
Plano A-este: 12,4 x 26,0 m, i = 40,5 %,
cota 10,40 a 5,38.
Rendija de cumbrera: 0,90 m x 23,4 m (21 m²)
protegida bajo el vuelo del plano oeste.
Plano B: 26 x 32 m, i = 15,4 %, sube hacia el cauce
(cota 3,60 a 7,60); vuelo de 1 m en 3 lados.
Chapa de zinc-titanio de junta alzada, cámara
ventilada de 8 cm, aislante de fibra de madera 14 cm,
tablero estructural y correas de madera laminada.
Recogida de pluviales: canalones a patio central
(aljibe de 90 m³ y jardín de lluvia).

LEYENDA

- Muro portante de ladrillo (cortado)
- Tabique
- Interior
- Pavimento exterior
- Vegetación / césped
- Agua / jardín de lluvia
- Por encima del plano de corte

PLANTA DE CUBIERTAS
E 1:100

CASO_012 · PROPUESTA A
Anteproyecto

PLANTA DE CUBIERTAS
Escala 1:100

LÁMINA
P03