

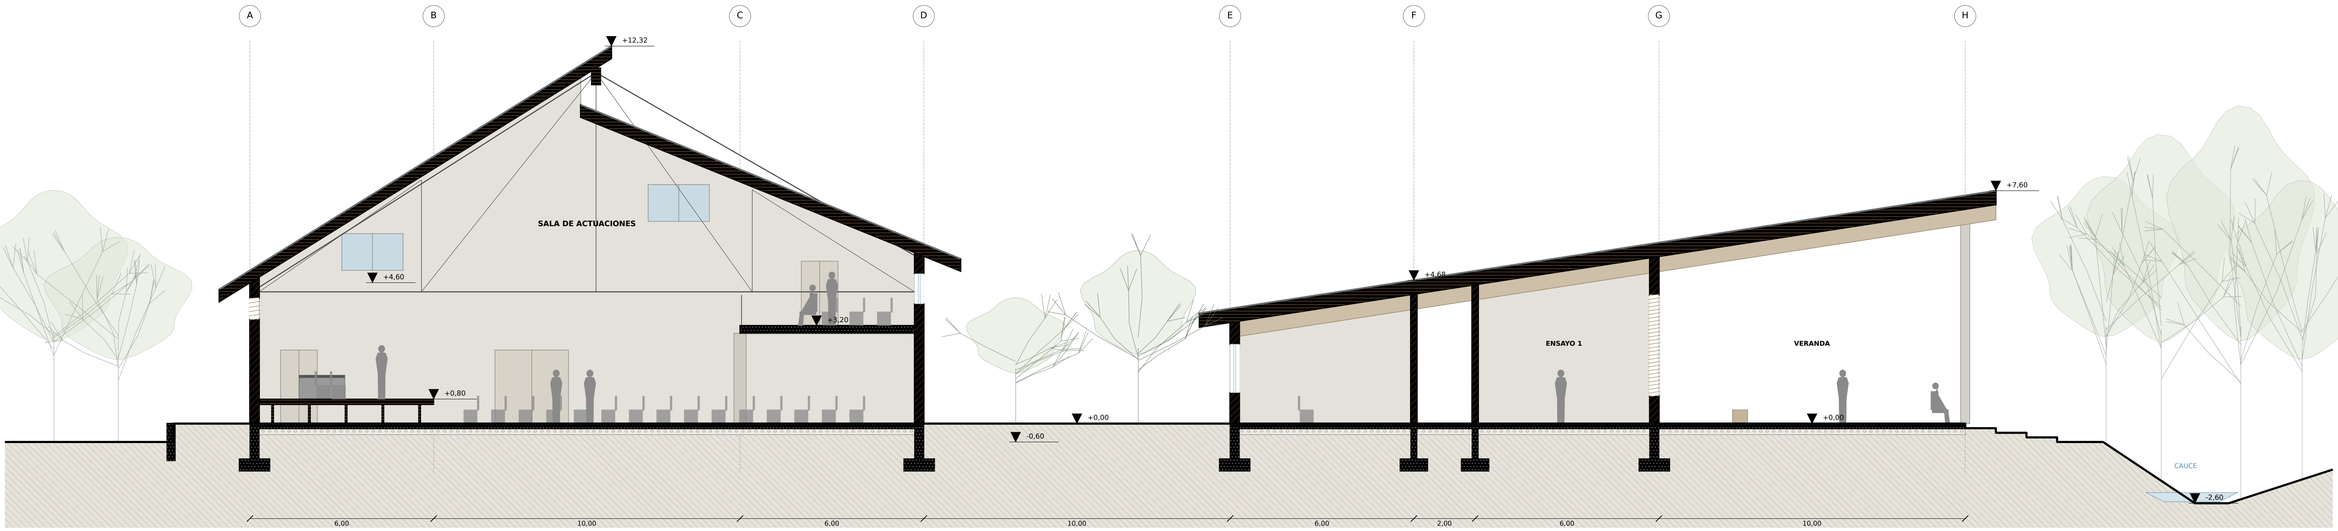


SECCIÓN LONGITUDINAL A-A'
E 1:100

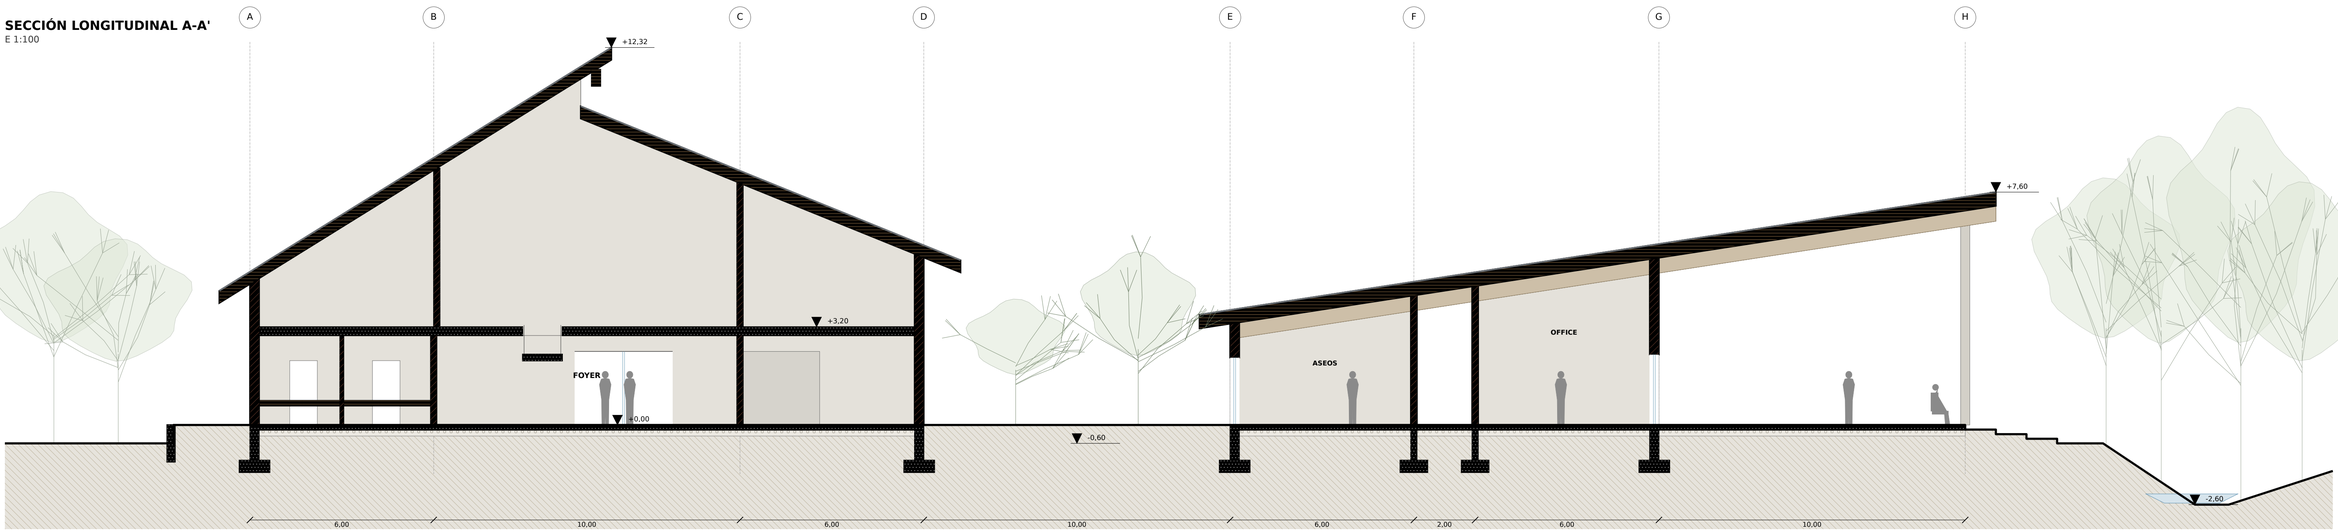

SECCIÓN LONGITUDINAL B-B'
E 1:100

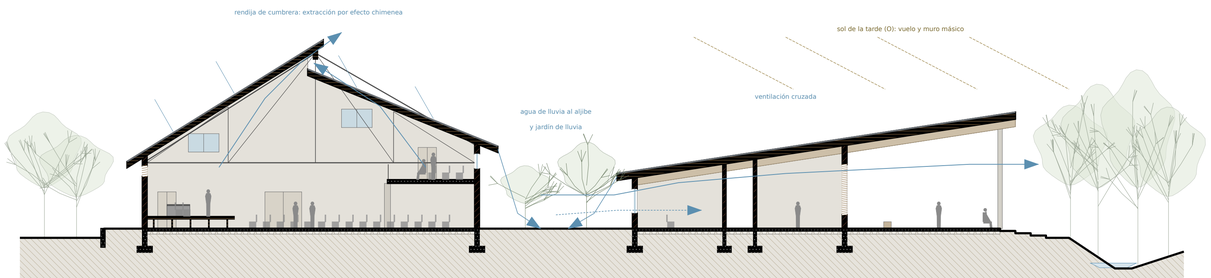

ESQUEMA BIOCLIMÁTICO (SOBRE A-A')
E 1:200

MATERIALES EN SECCIÓN

- Hormigón armado (zapatas, soleras, forjados, pilares)
- Fábrica de ladrillo cerámico visto (muros, tabiques)
- Madera laminada (cerchas, vigas, correas, cubierta y tarima)
- Terreno natural y relleno compactado de la plataforma
- Grava de drenaje bajo solera
- Aislante térmico (ver detalle D01)
- Vidrio / carpintería; lamas de madera practicables en huecos de ensayo

Lo visto en proyección: gris claro; trazo fino. Cotas en metros.

CASO_012 · PROPUESTA A Anteproyecto	LÁMINA
SECCIONES LONGITUDINALES A-A' Y B-B' Escala 1:100	**S01**