
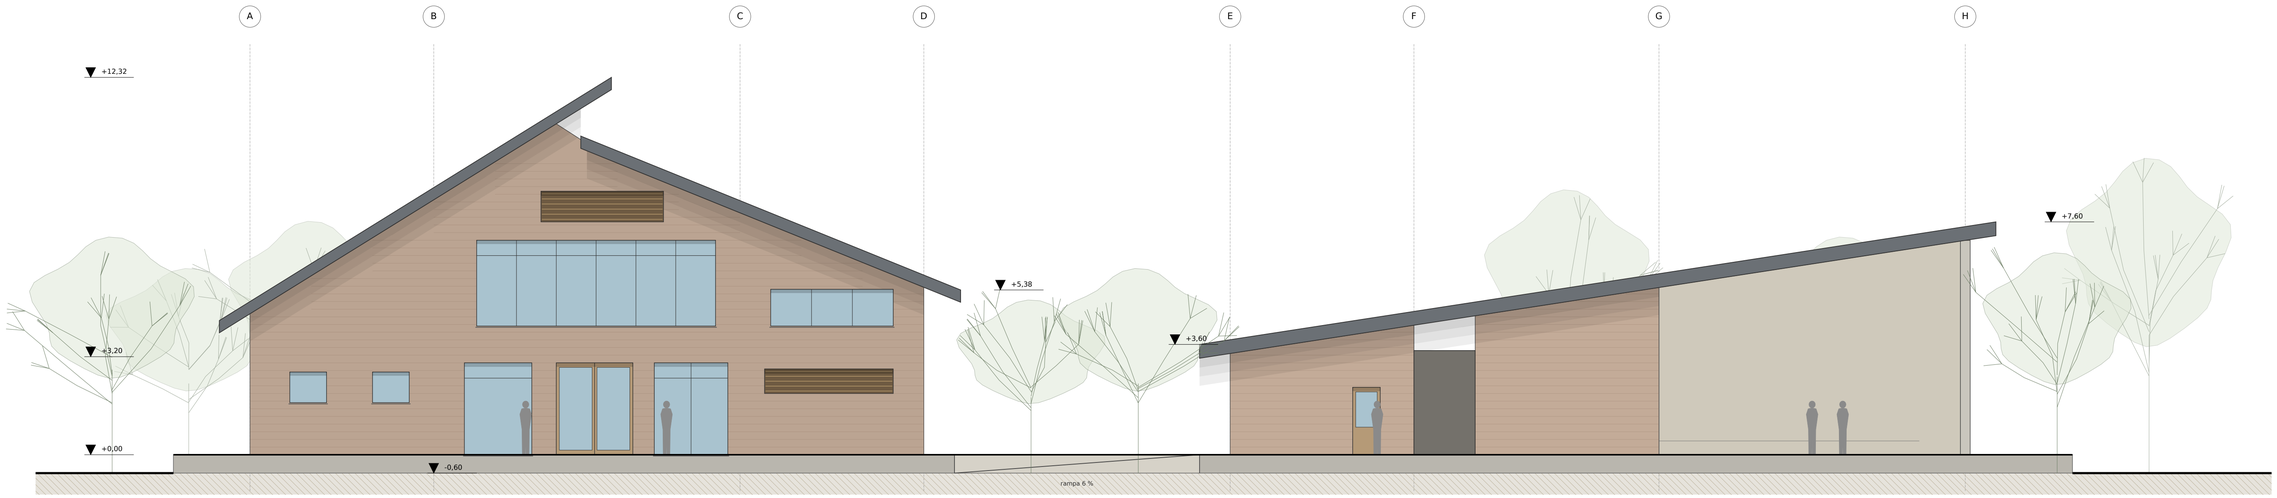


ALZADO SUR (ACCESO DESDE LA CALLE)
E 1:100

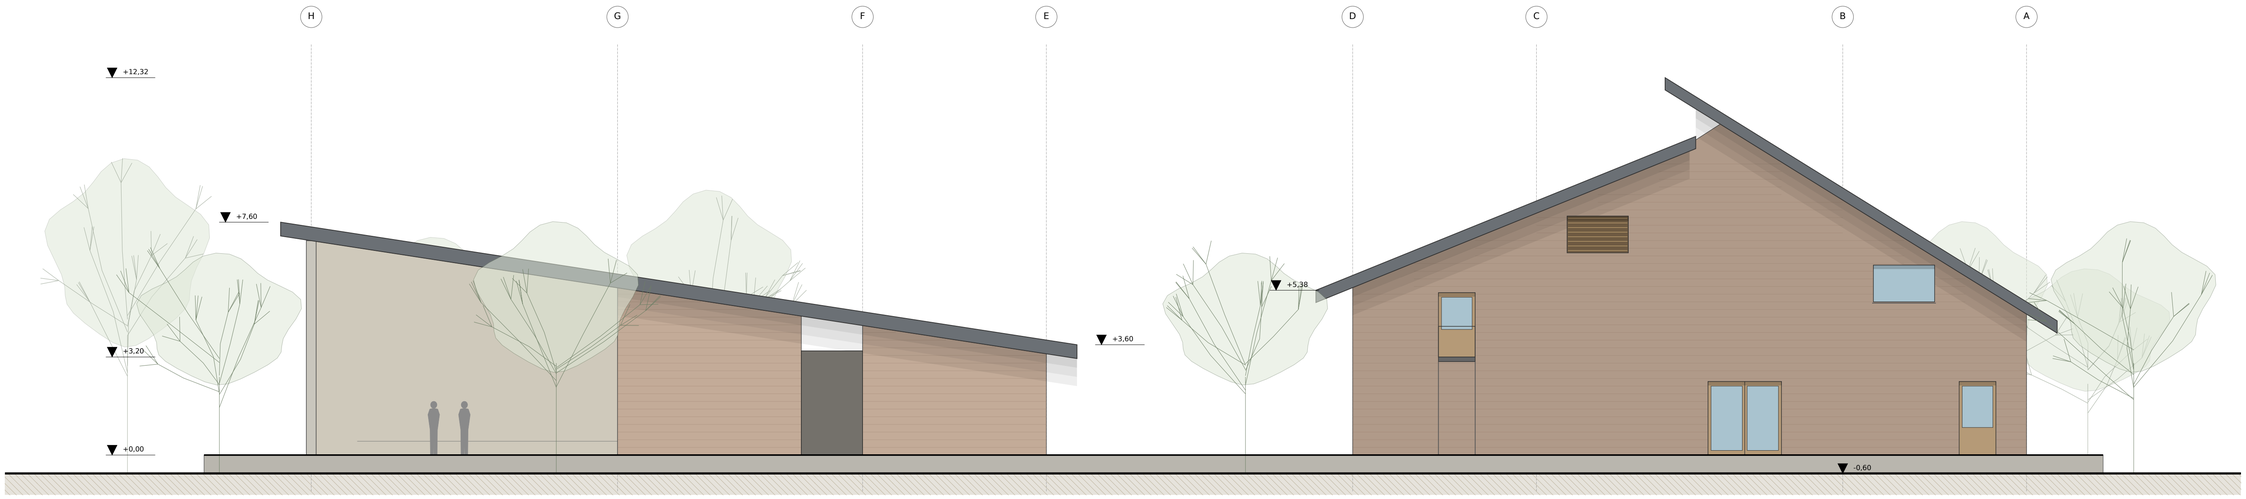

ALZADO NORTE
E 1:100

MATERIALES DE FACHADA

- Ladrillo cerámico visto, tono ocre apagado (muros)
- Chapa de zinc-titanio, junta alzada (cubiertas)
- Madera tratada: lamas practicables, vigas y pilares
- Vidrio laminado con carpintería de madera
- Hormigón visto (zócalo de la plataforma)

CASO_012 · PROPUESTA A
Anteproyecto

LÁMINA

ALZADOS SUR Y NORTE
Escala 1:100

S03