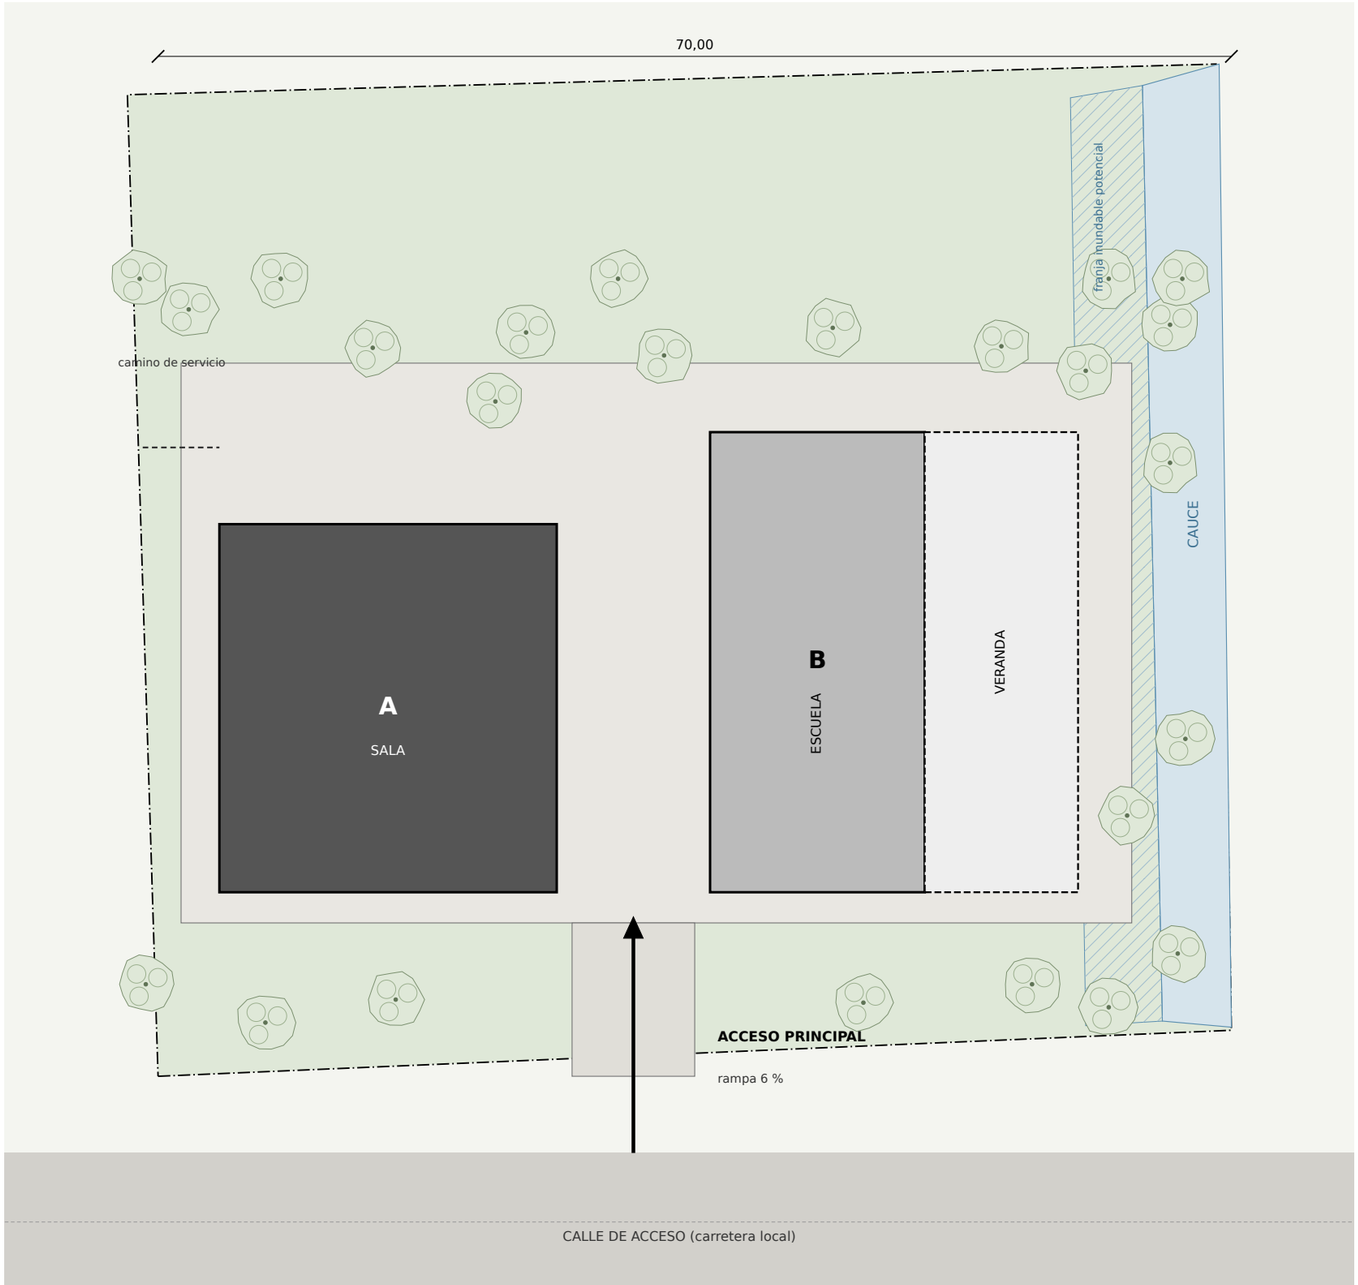

N

LEYENDA

- Parcela (≈ 68 x 63 m, cuadrilátero irregular)
- Cauce y ribera con arbolado
- Plataforma elevada +0,60 sobre el terreno
- A · sala de actuaciones (2 plantas)
- B · escuela de música (1 planta)
- Veranda cubierta, aula abierta al cauce

Orientación: sur a la calle de acceso, este al cauce.
Sala con eje largo norte-sur: muros másicos a este y oeste.
Veranda al este: vistas al cauce, protegida del sol
de la tarde por el muro oeste de la escuela y el vuelo.
Suelo terminado a +0,60 sobre el terreno y 2,60 m sobre
el fondo del cauce; edificios a más de 5 m del agua.

0 1 2 5 10 m

PLANO DE SITUACIÓN

E 1:400

CASO_012 · PROPUESTA A Anteproyecto	LÁMINA
PLANO DE SITUACIÓN Escala 1:400	**U01**