
SECCIÓN CONSTRUCTIVA 1 · MURO SUR DE LA PIEZA B

Cimentación, zócalo, muro de entramado, ventana y alero · E 1:20

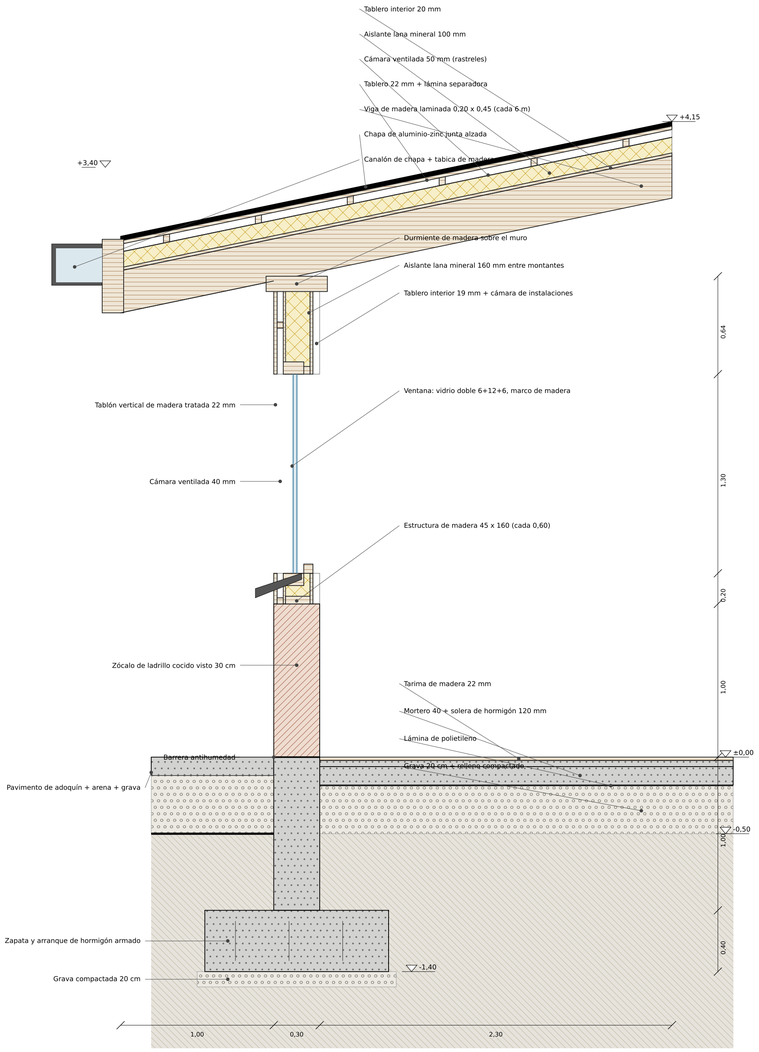


COMPOSICIÓN DE CERRAMIENTOS (de exterior a interior)

Elemento	Capas	Espesor	U aprox. (W/m²K)
Muro de entramado ligero	tablón vertical 22 · cámara ventilada 40 · tablero 15 · lana mineral 160 entre montantes · tablero 19 · cámara de instalaciones 44	0,30 m	0,28
Zócalo	ladrillo cocido visto 300 · barrera antihumedad en arranque · zapata corrida de hormigón armado	0,30 m	1,6
Cubierta ventilada	chapa aluminio-zinc junta alzada · tablero 22 · cámara 50 · lámina transpirable · lana mineral 100 · tablero 20 · viga laminada	0,50 m	0,32
Solera sobre relleno	tarima 22 · mortero 40 · hormigón 120 · lámina PE · grava 200 · relleno compactado (podio +0,50)	0,50 m	—
Lucernario norte	vidrio 6+12+6 en marco de madera · lamas fijas exteriores de madera · babero de chapa	3,3 m libres	2,3


SECCIÓN CONSTRUCTIVA 2 · ENCUENTRO DE CUBIERTAS Y LUCERNARIO NORTE

Cumbrera de la cubierta 1 sobre el arranque de la cubierta 2 · E 1:20

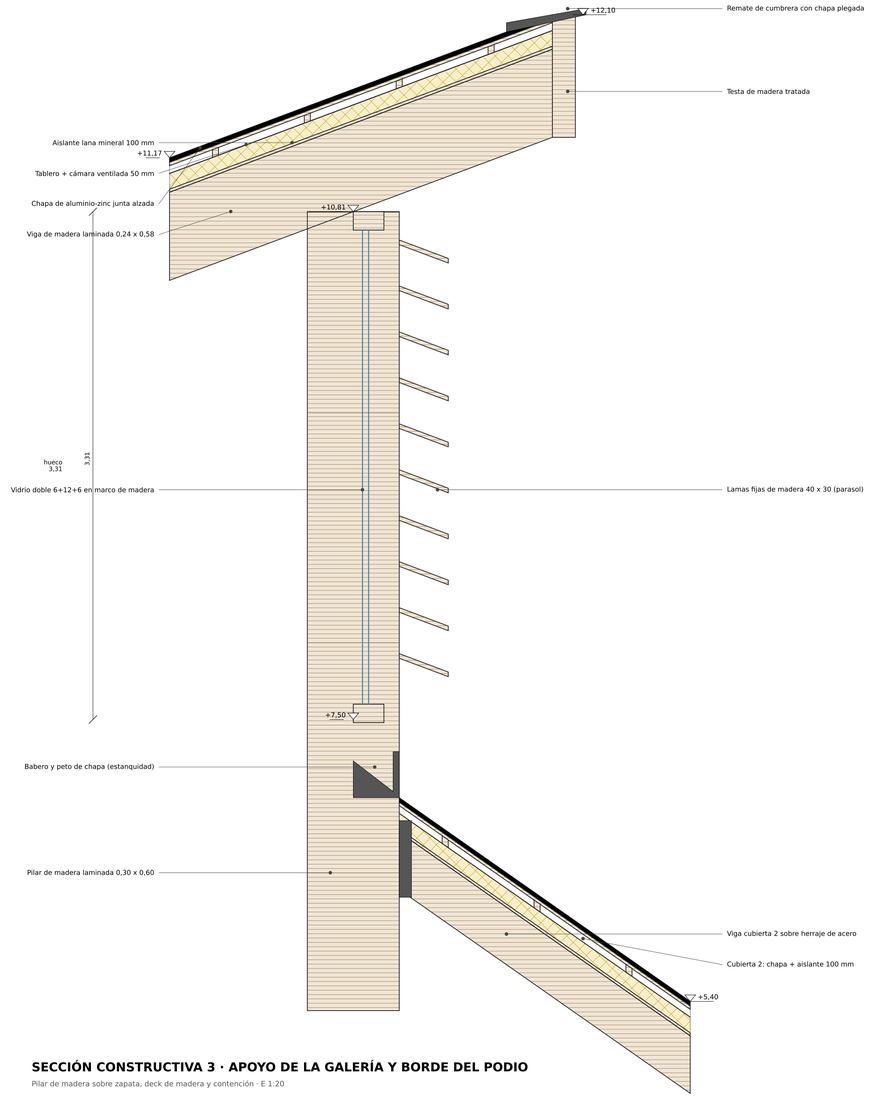

SECCIÓN CONSTRUCTIVA 3 · APOYO DE LA GALERÍA Y BORDE DEL PODIO

Pilar de madera sobre zapata, deck de madera y contención · E 1:20

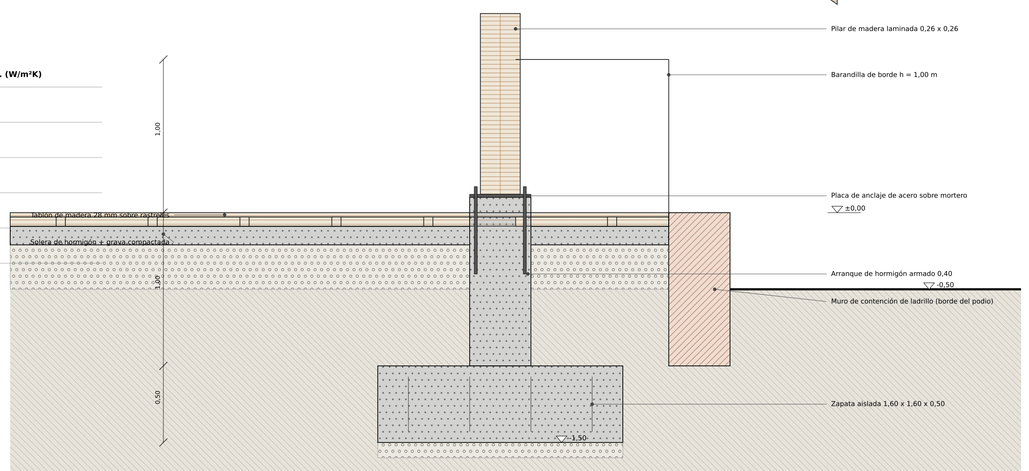

CASO_012 · PROPUESTA B Anteproyecto · Equipamiento comunitario musical		ESCALA **1:20**	LÁMINA **D01**
Detalle constructivo		Anteproyecto	A1 · horizontal