
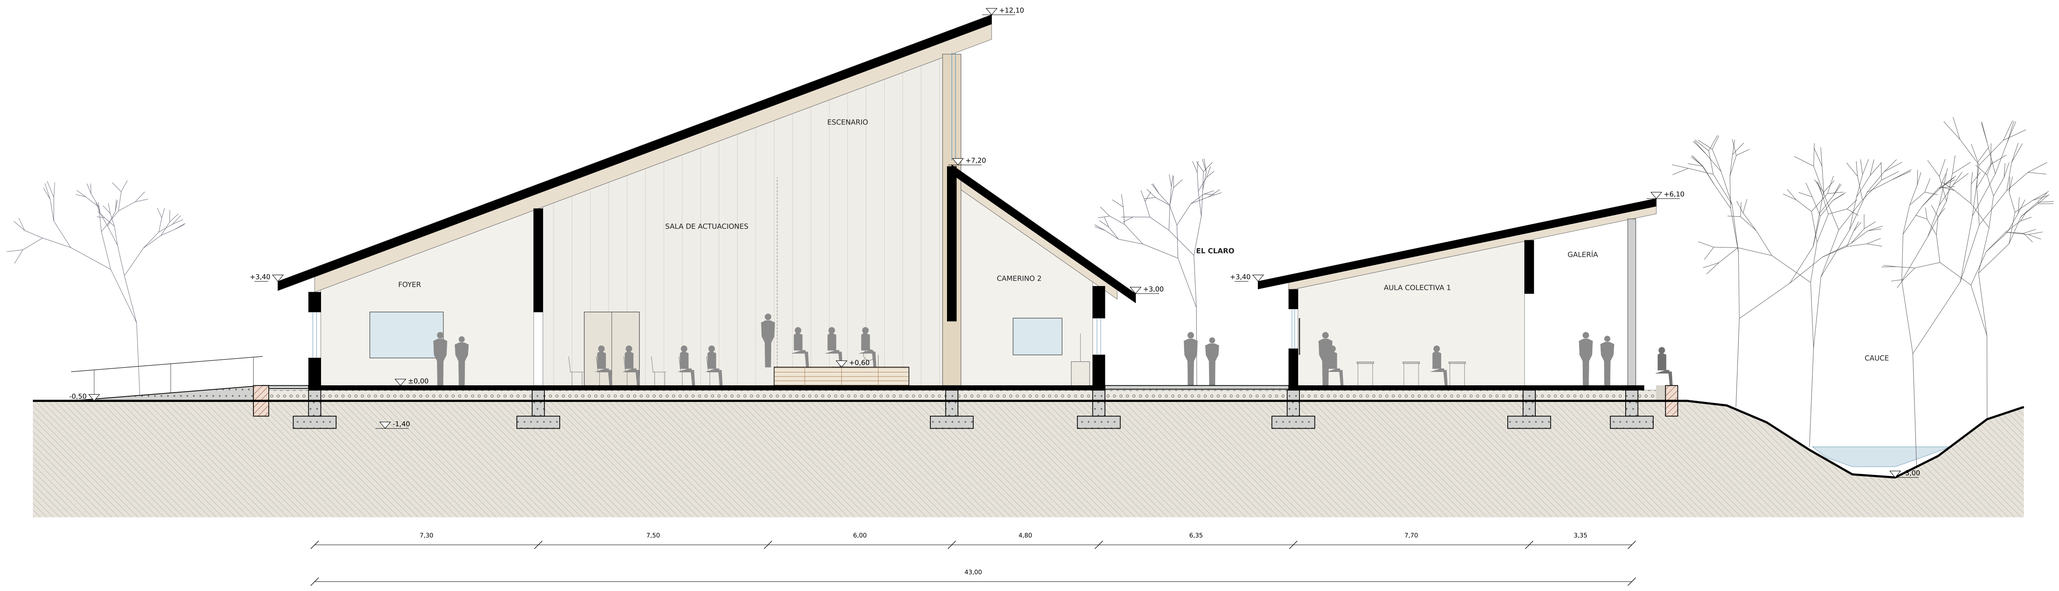


SECCIÓN LONGITUDINAL A-A' E 1:100 corte por x = 25,60, mirando al oeste

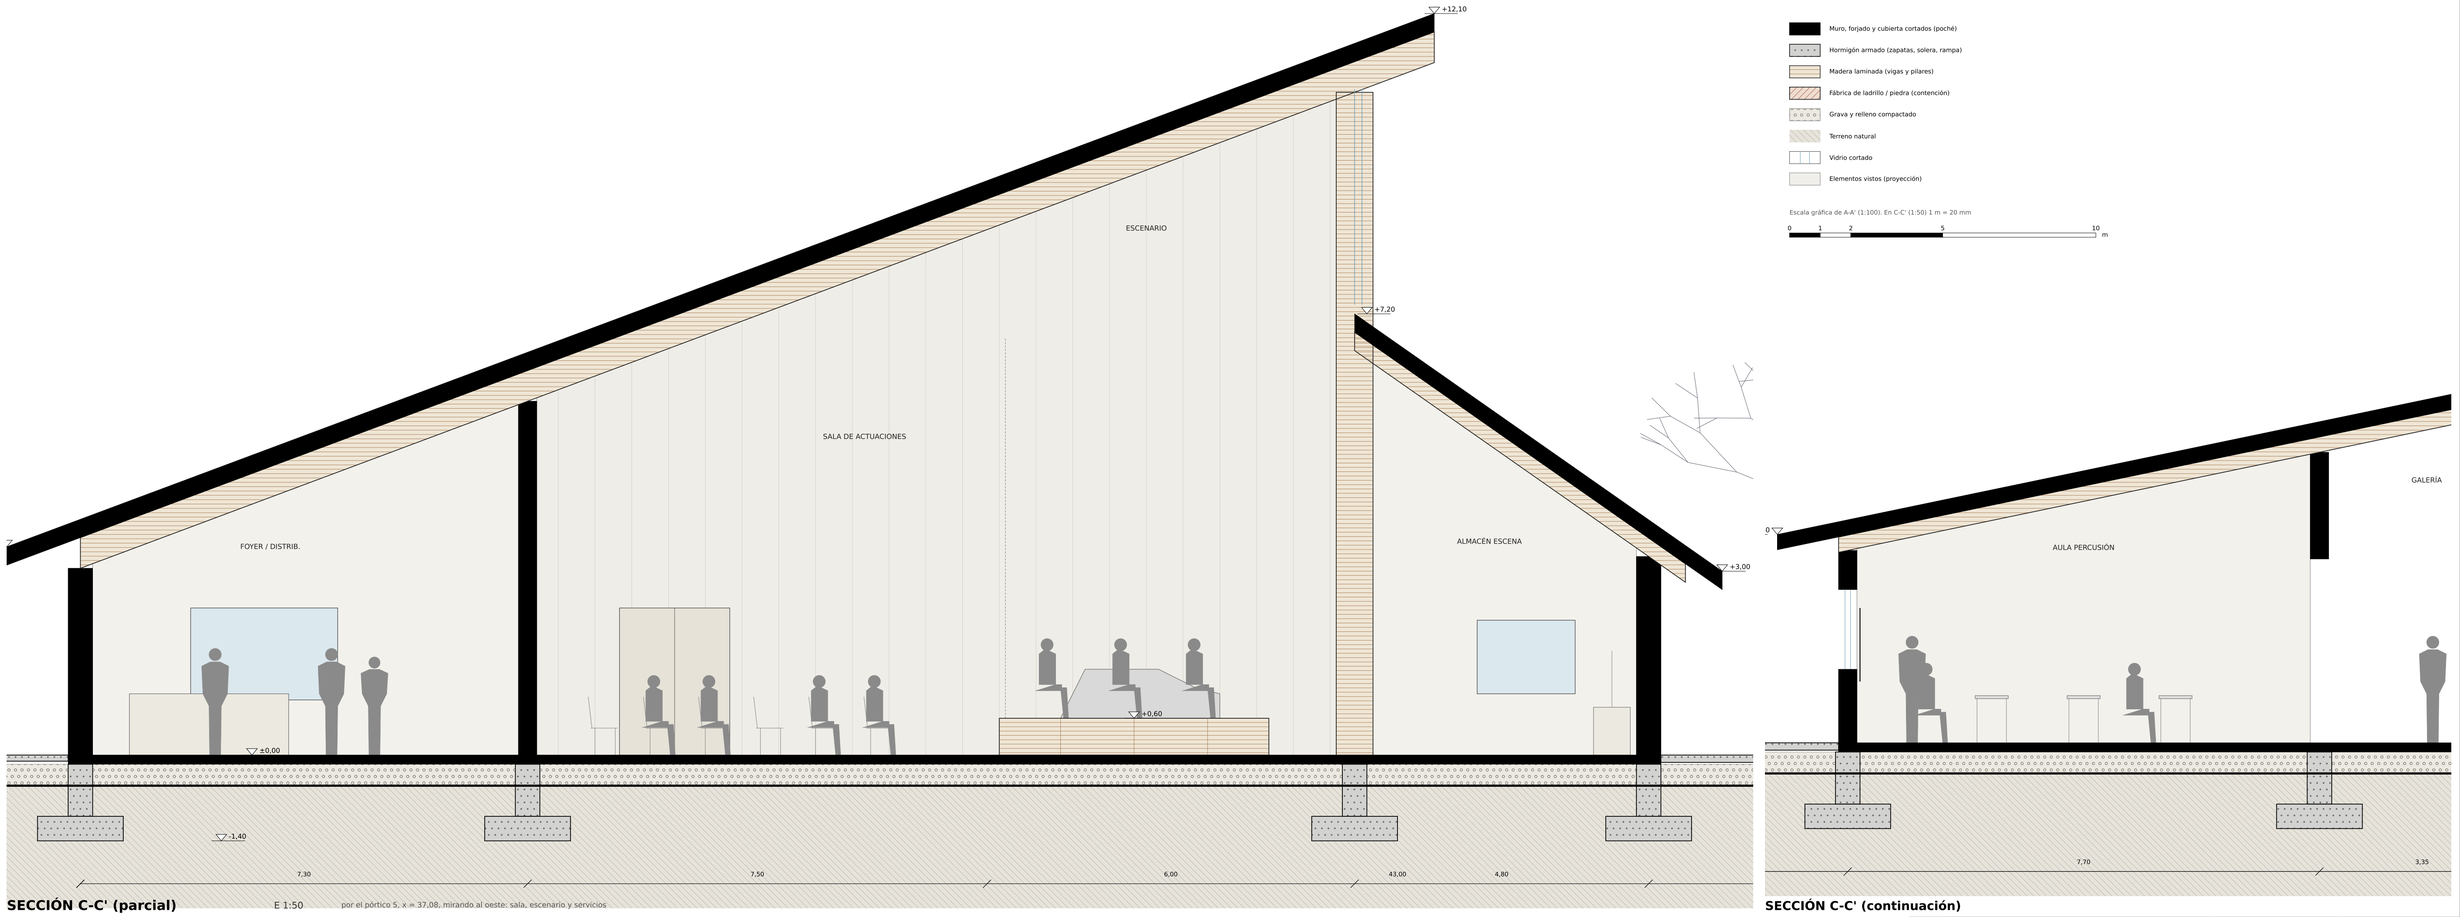

SECCIÓN C-C' (parcial) E 1:50 por el pórtico 5, x = 37,08, mirando al oeste: sala, escenario y servicios

Muro, forjado y cubierta cortados (poché)

Hormigón armado (zapatas, solera, rampa)

Madera laminada (vigas y pilares)

Fábrica de ladrillo / piedra (contención)

Grava y relleno compactado

Terreno natural

Vidrio cortado

Elementos vistos (proyección)

Escala gráfica de A-A' (1:100). En C-C' (1:50) 1 m = 20 mm

0 1 2 5 10 m

SECCIÓN C-C' (continuación) pieza B · E 1:50

CASO_012 · PROPUESTA B Anteproyecto · Equipamiento comunitario musical	ESCALA **1:100**	LÁMINA **S01**
Secciones longitudinales A-A' y C-C'	Anteproyecto	A1 · horizontal