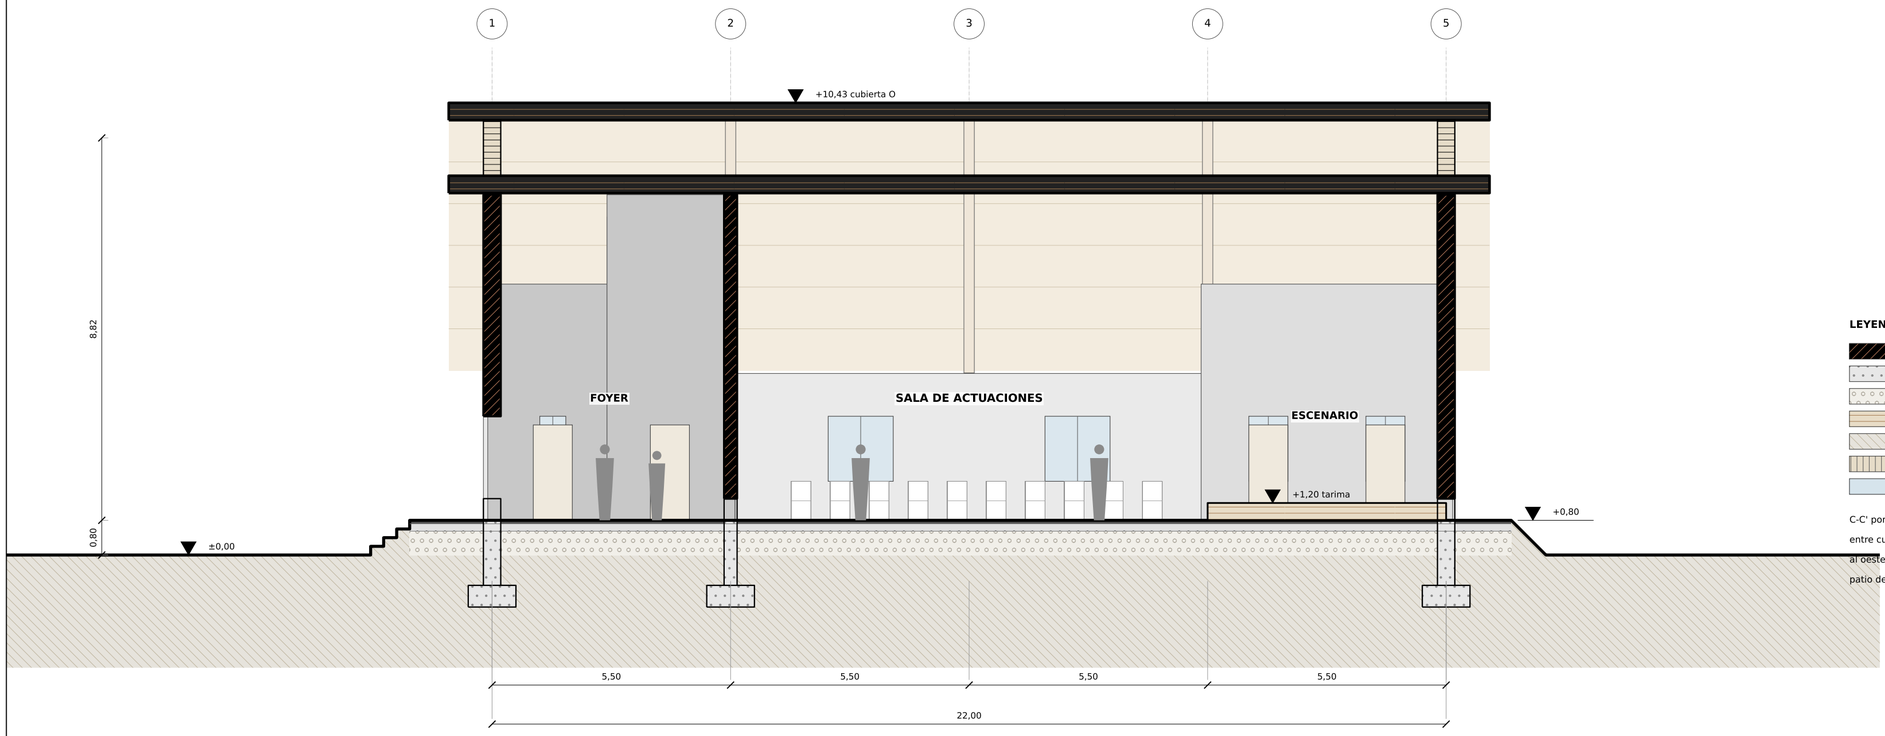



SECCIÓN C-C'

E 1:100

LEYENDA DE MATERIALES EN CORTE

- Muro de bloque de tierra comprimida (BTC) estabilizada, e=40 cm
- Hormigón ciclópeo / armado (zapata y zócalo)
- Relleno compactado de grava (plataforma)
- Madera laminada y tarima; cubierta de cabios sobre cámara ventilada
- Terreno natural
- Lamas de madera (banda de extracción)
- Agua / nivel ordinario del cauce

C-C' por x = 20,00 mirando al oeste: foyer, banda de lamas entre cubiertas y escenario. D-D' por x = 41,00 mirando al oeste: cabina, aula colectiva y sala de ensayo; al fondo, patio de lluvia y fachada este de la sala.

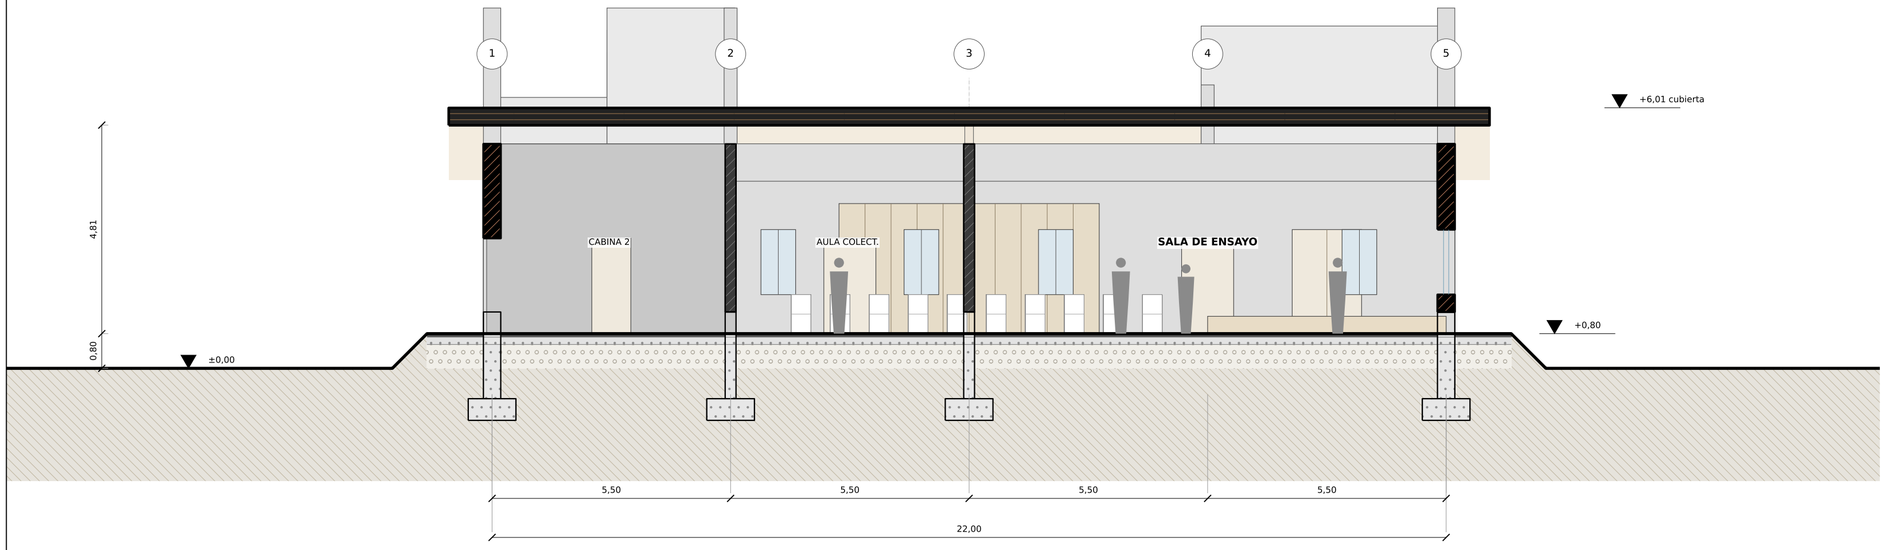

SECCIÓN D-D'

E 1:100

CASO_012 · PROPUESTA C	Anteproyecto
Secciones transversales C-C' y D-D' Escala 1:100	**S02**