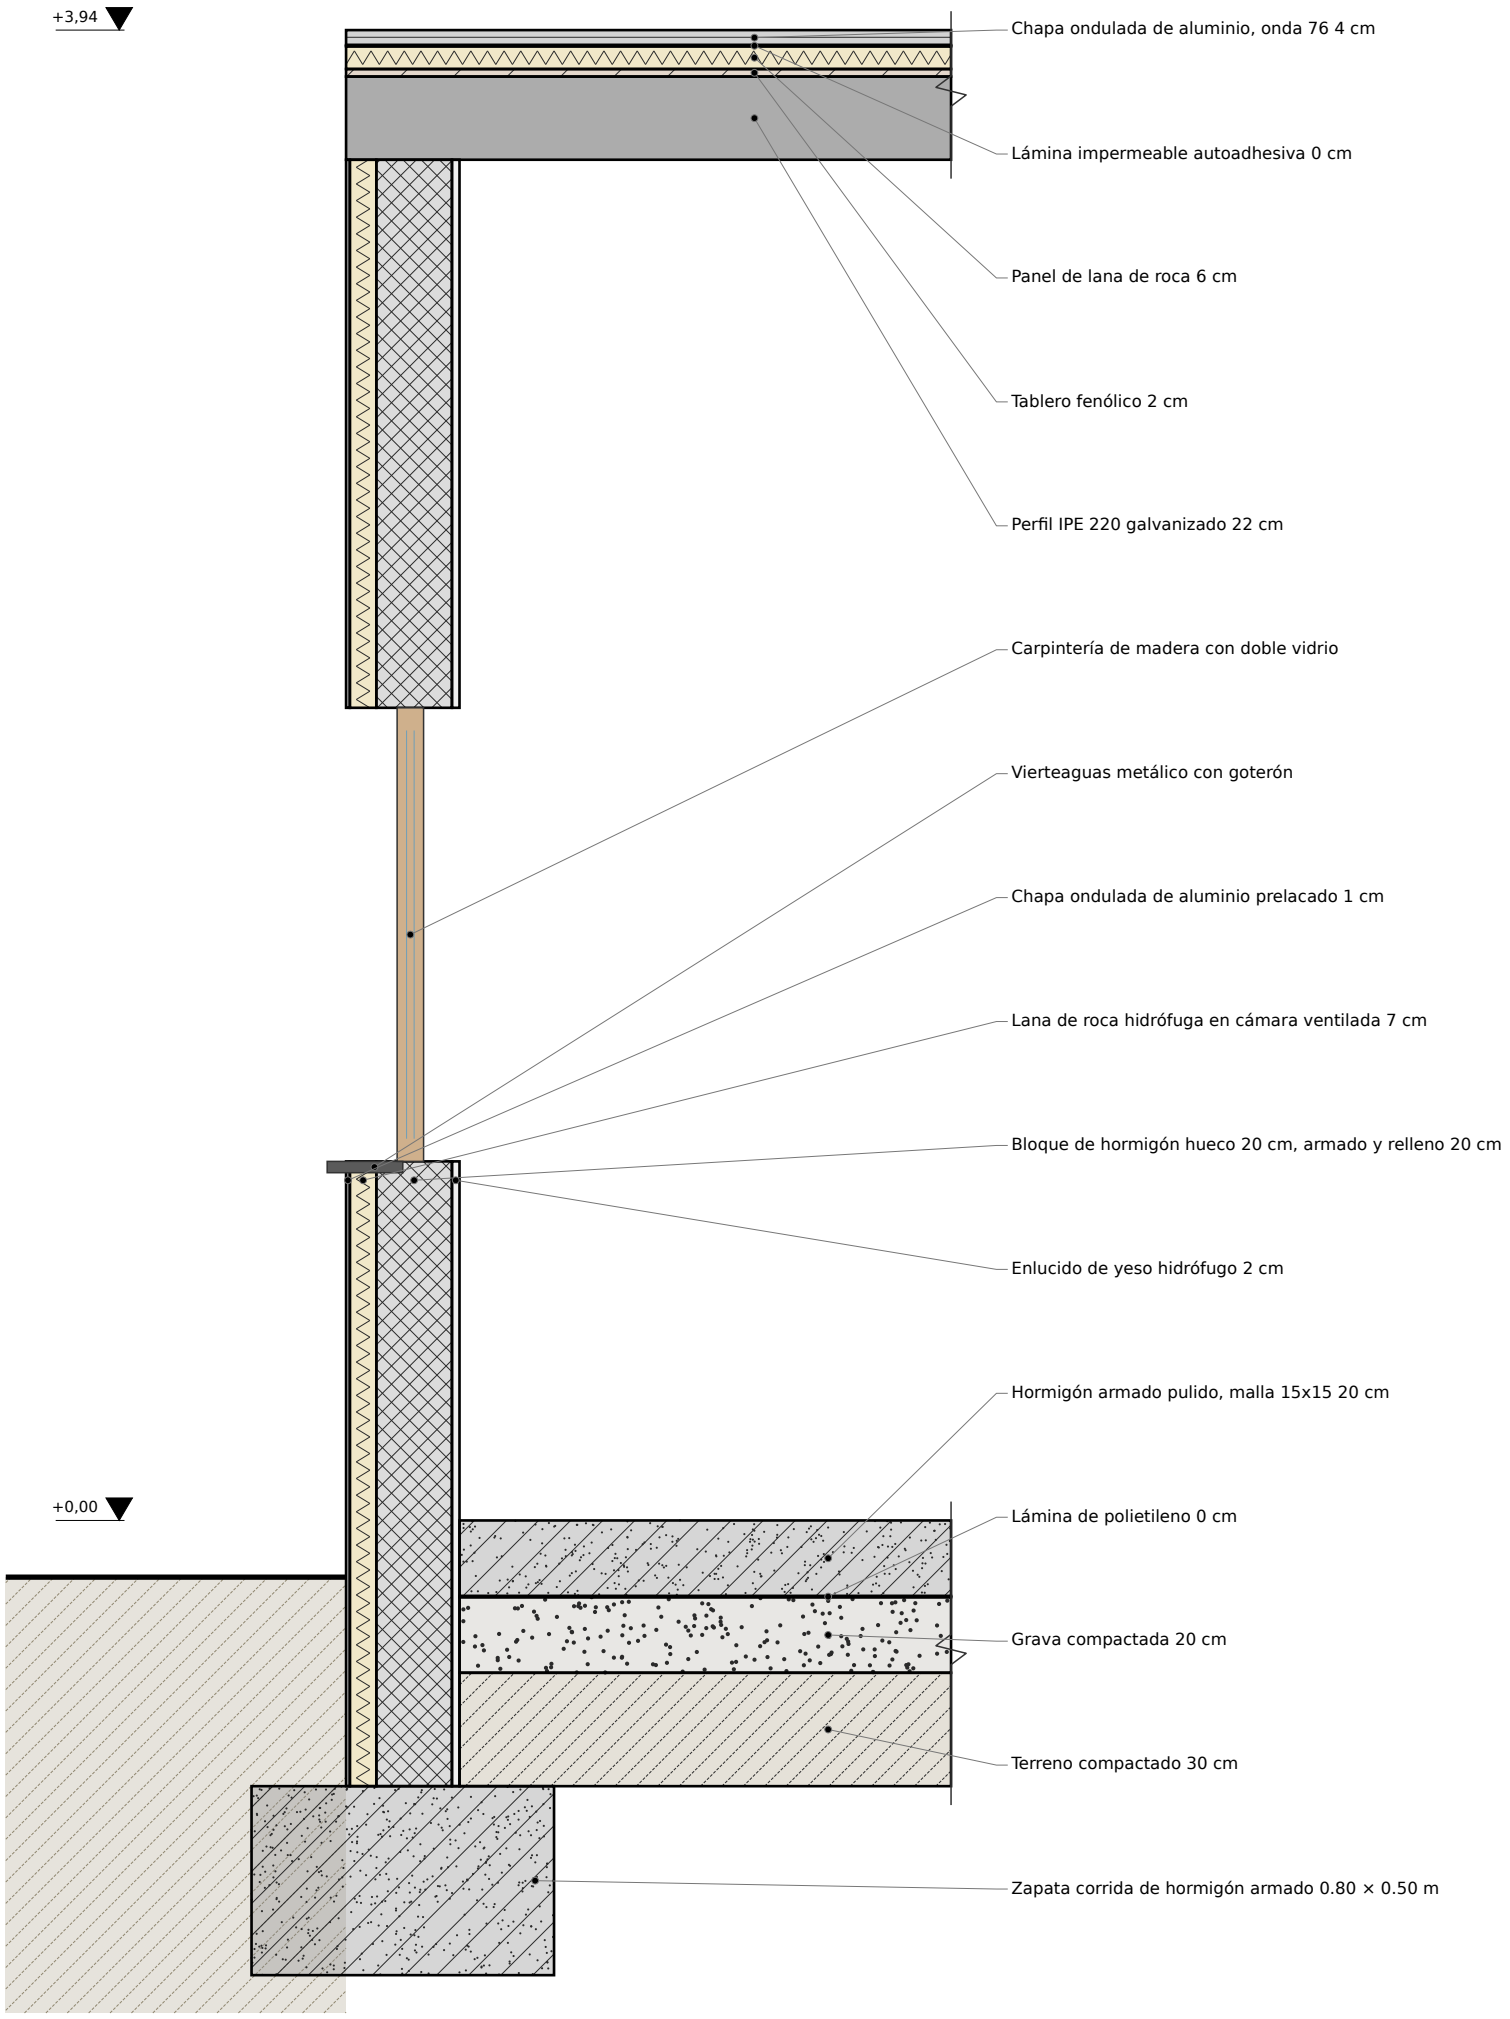

DETALLE CONSTRUCTIVO

E 1:20

0 0.5 1 2 m

CASO_014 · PROPUESTA B	E 1:20	**D01**
SECCIÓN CONSTRUCTIVA DE FACHADA	Anteproyecto	