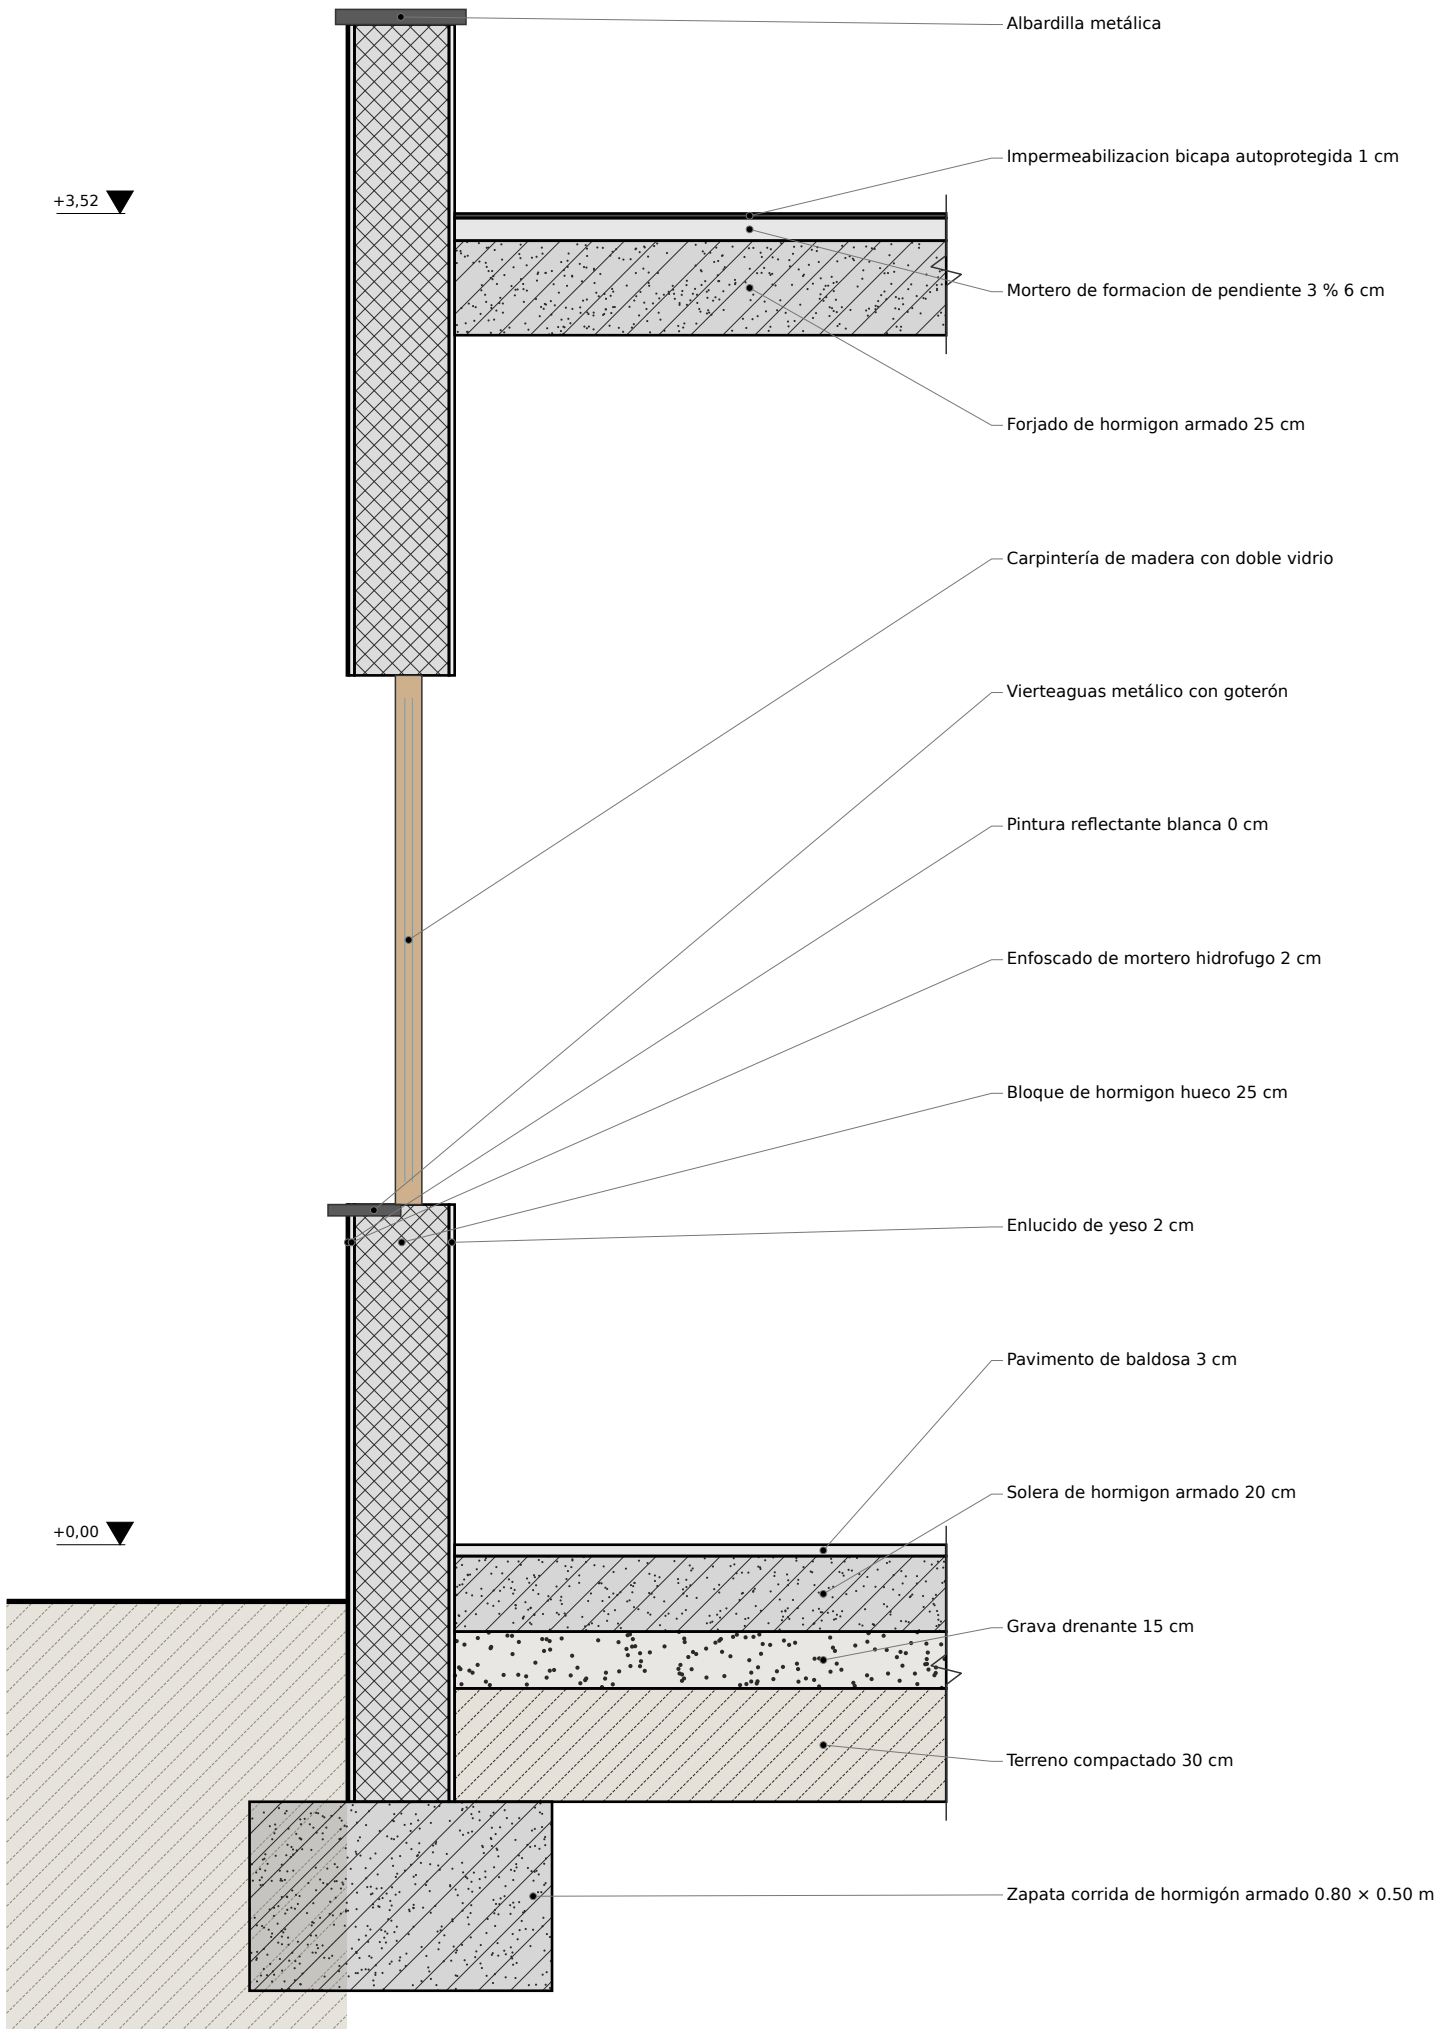


DETALLE CONSTRUCTIVO

E 1:20

0 0.5 1 2 m

CASO_014 · PROPUESTA C	E 1:20	**D01**
SECCION CONSTRUCTIVA DE FACHADA (TORRE) 1:20	Anteproyecto	