sol invierno 25,2°: lo detienen el vecino y el plano

sol verano 72,0° (79 % del pozo al sol)

sol equinoccio 48,6° (43 %)

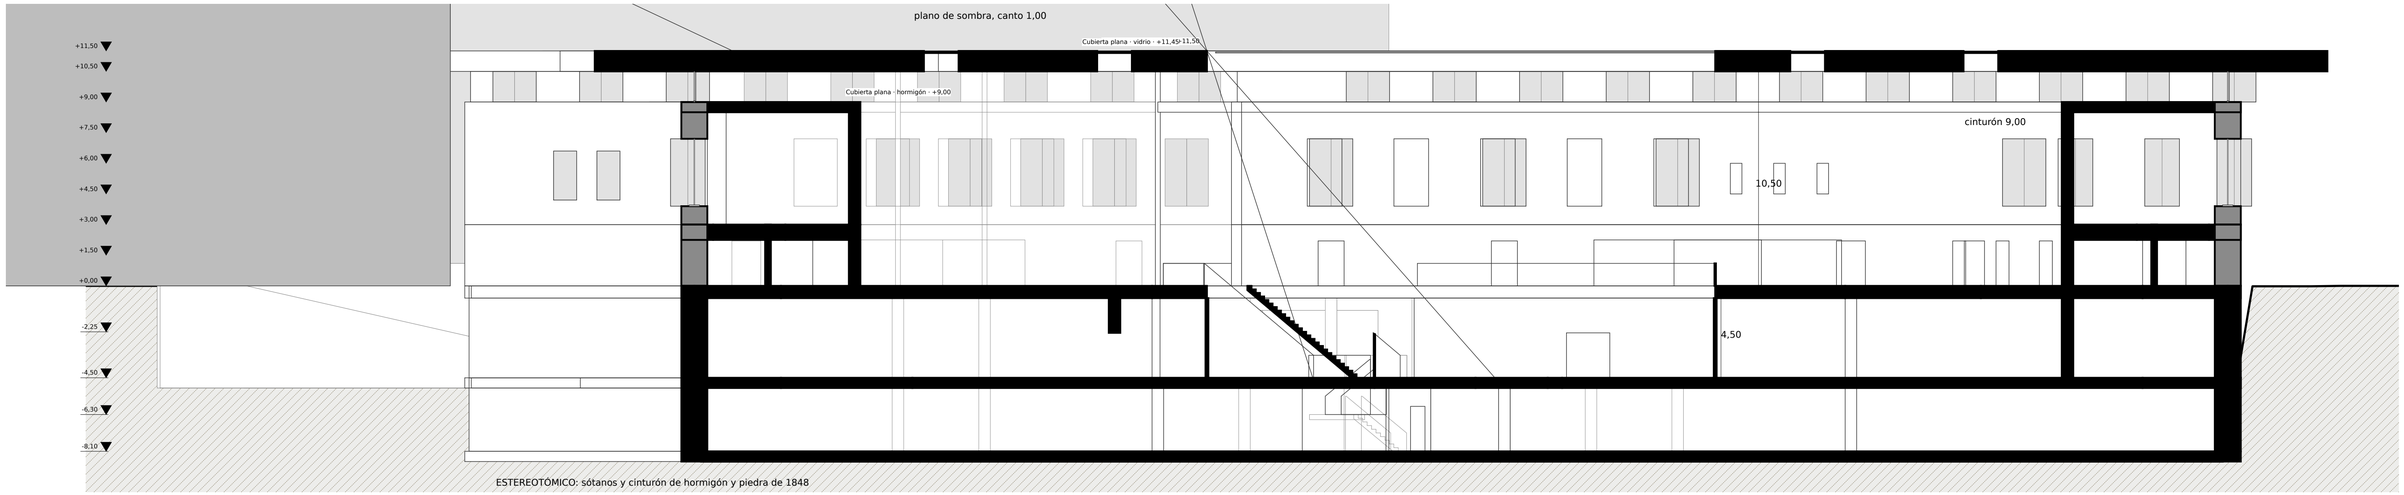

ESTEREOTÓMICO: sótanos y cinturón de hormigón y piedra de 1848

TECTÓNICO: plano de acero (canto 1,00) sobre pilares Ø 0,24 en retícula 12 x 6

MÓDULO 6 m: sala 10 x 7 m, pozo 4 x 3 m, alturas 4,50 y 10,50 (3,5 x 3)

SECCIÓN A-A'

E 1:150

0 1 2 5 10 m

CASO_019 · PROPUESTA A	E 1:150	**S01**
SECCIÓN GENERADORA	Anteproyecto	