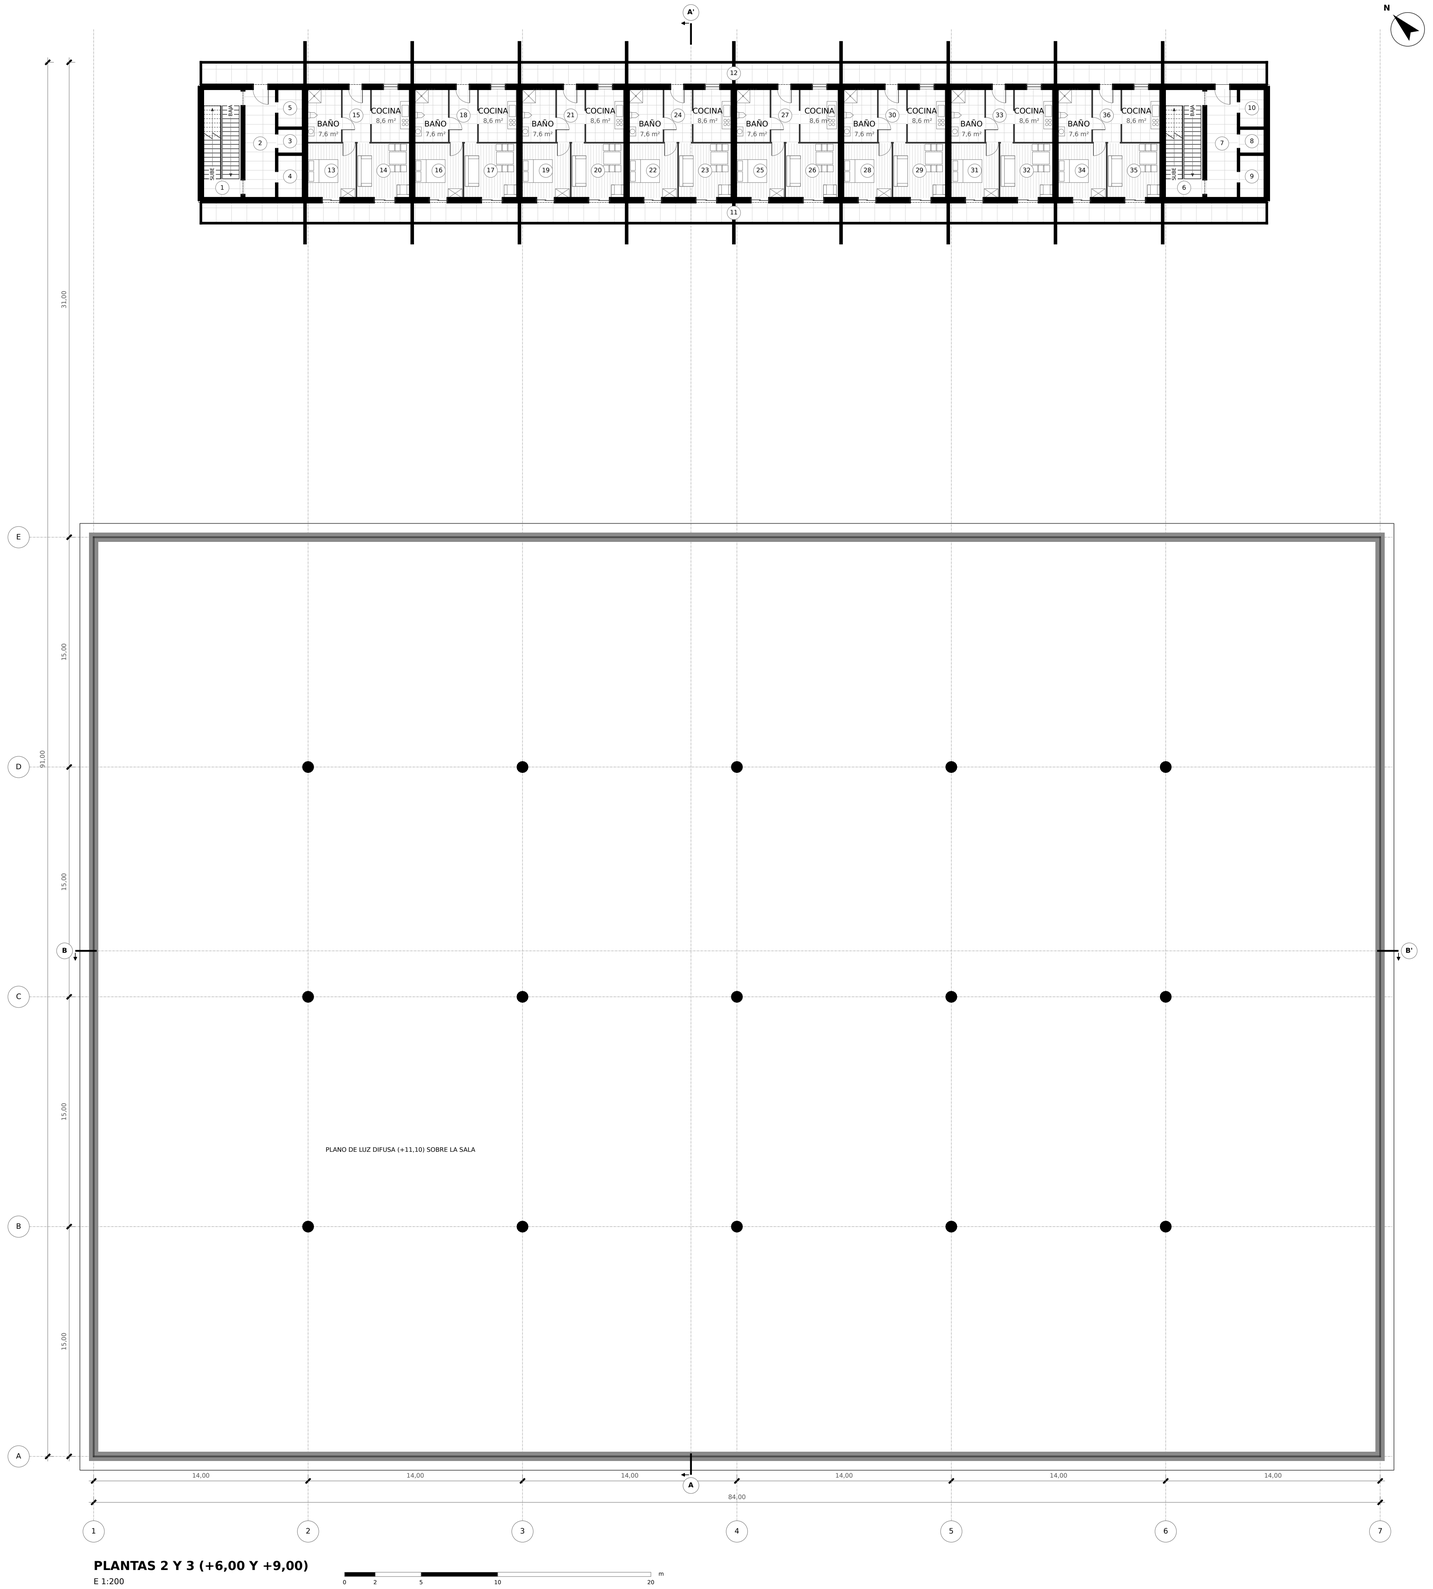


PLANTAS 2 Y 3 (+6,00 Y +9,00)

E 1:200

0 2 5 10 20 m

Obra nueva
Existente que se conserva
Existente que se demuele

1 Escalera · 3,3 m²
2 Vestíbulo · 14,6 m²
3 Ascensor · 2,6 m²
4 Patinillo de instalaciones · 4,6 m²
5 Patinillo de instalaciones · 4,1 m²
6 Escalera · 3,3 m²
7 Vestíbulo · 14,6 m²
8 Ascensor · 2,6 m²
9 Patinillo de instalaciones · 4,6 m²
10 Patinillo de instalaciones · 4,1 m²
11 Logia · 94,0 m²
12 Galería · 100,9 m²
13 Dormitorio · 11,2 m²
14 Estar-comedor · 12,2 m²
15 Vestíbulo · 6,2 m²
16 Dormitorio · 11,2 m²
17 Estar-comedor · 12,2 m²
18 Vestíbulo · 6,2 m²
19 Dormitorio · 11,2 m²
20 Estar-comedor · 12,2 m²
21 Vestíbulo · 6,2 m²
22 Dormitorio · 11,2 m²
23 Estar-comedor · 12,2 m²
24 Vestíbulo · 6,2 m²
25 Dormitorio · 11,2 m²
26 Estar-comedor · 12,2 m²
27 Vestíbulo · 6,2 m²
28 Dormitorio · 11,2 m²
29 Estar-comedor · 12,2 m²
30 Vestíbulo · 6,2 m²
31 Dormitorio · 11,2 m²
32 Estar-comedor · 12,2 m²
33 Vestíbulo · 6,2 m²
34 Dormitorio · 11,2 m²
35 Estar-comedor · 12,2 m²
36 Vestíbulo · 6,2 m²

CASO_019 · PROPUESTA B

PLANTAS SEGUNDA Y TERCERA

E 1:200

Anteproyecto

P05