21 DIC 12:00 · 25,2° (33,6° EN EL CORTE): ENTRA

21 JUN 12:00 · 72° (77° EN EL CORTE): NO ENTRA

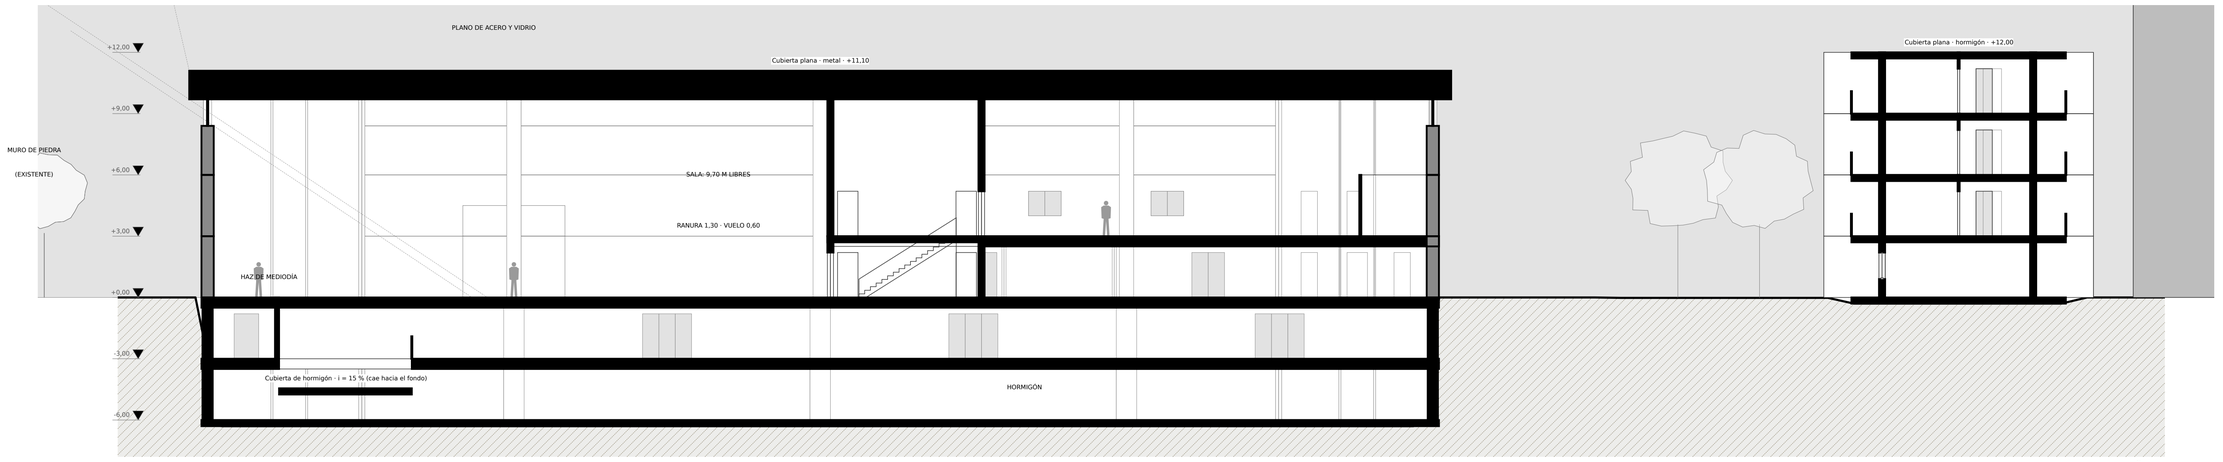

SECCIÓN A-A'

E 1:150

CORTE A-A'

CASO_019 · PROPUESTA B	E 1:150	**S01**
SECCIÓN GENERADORA	Anteproyecto	