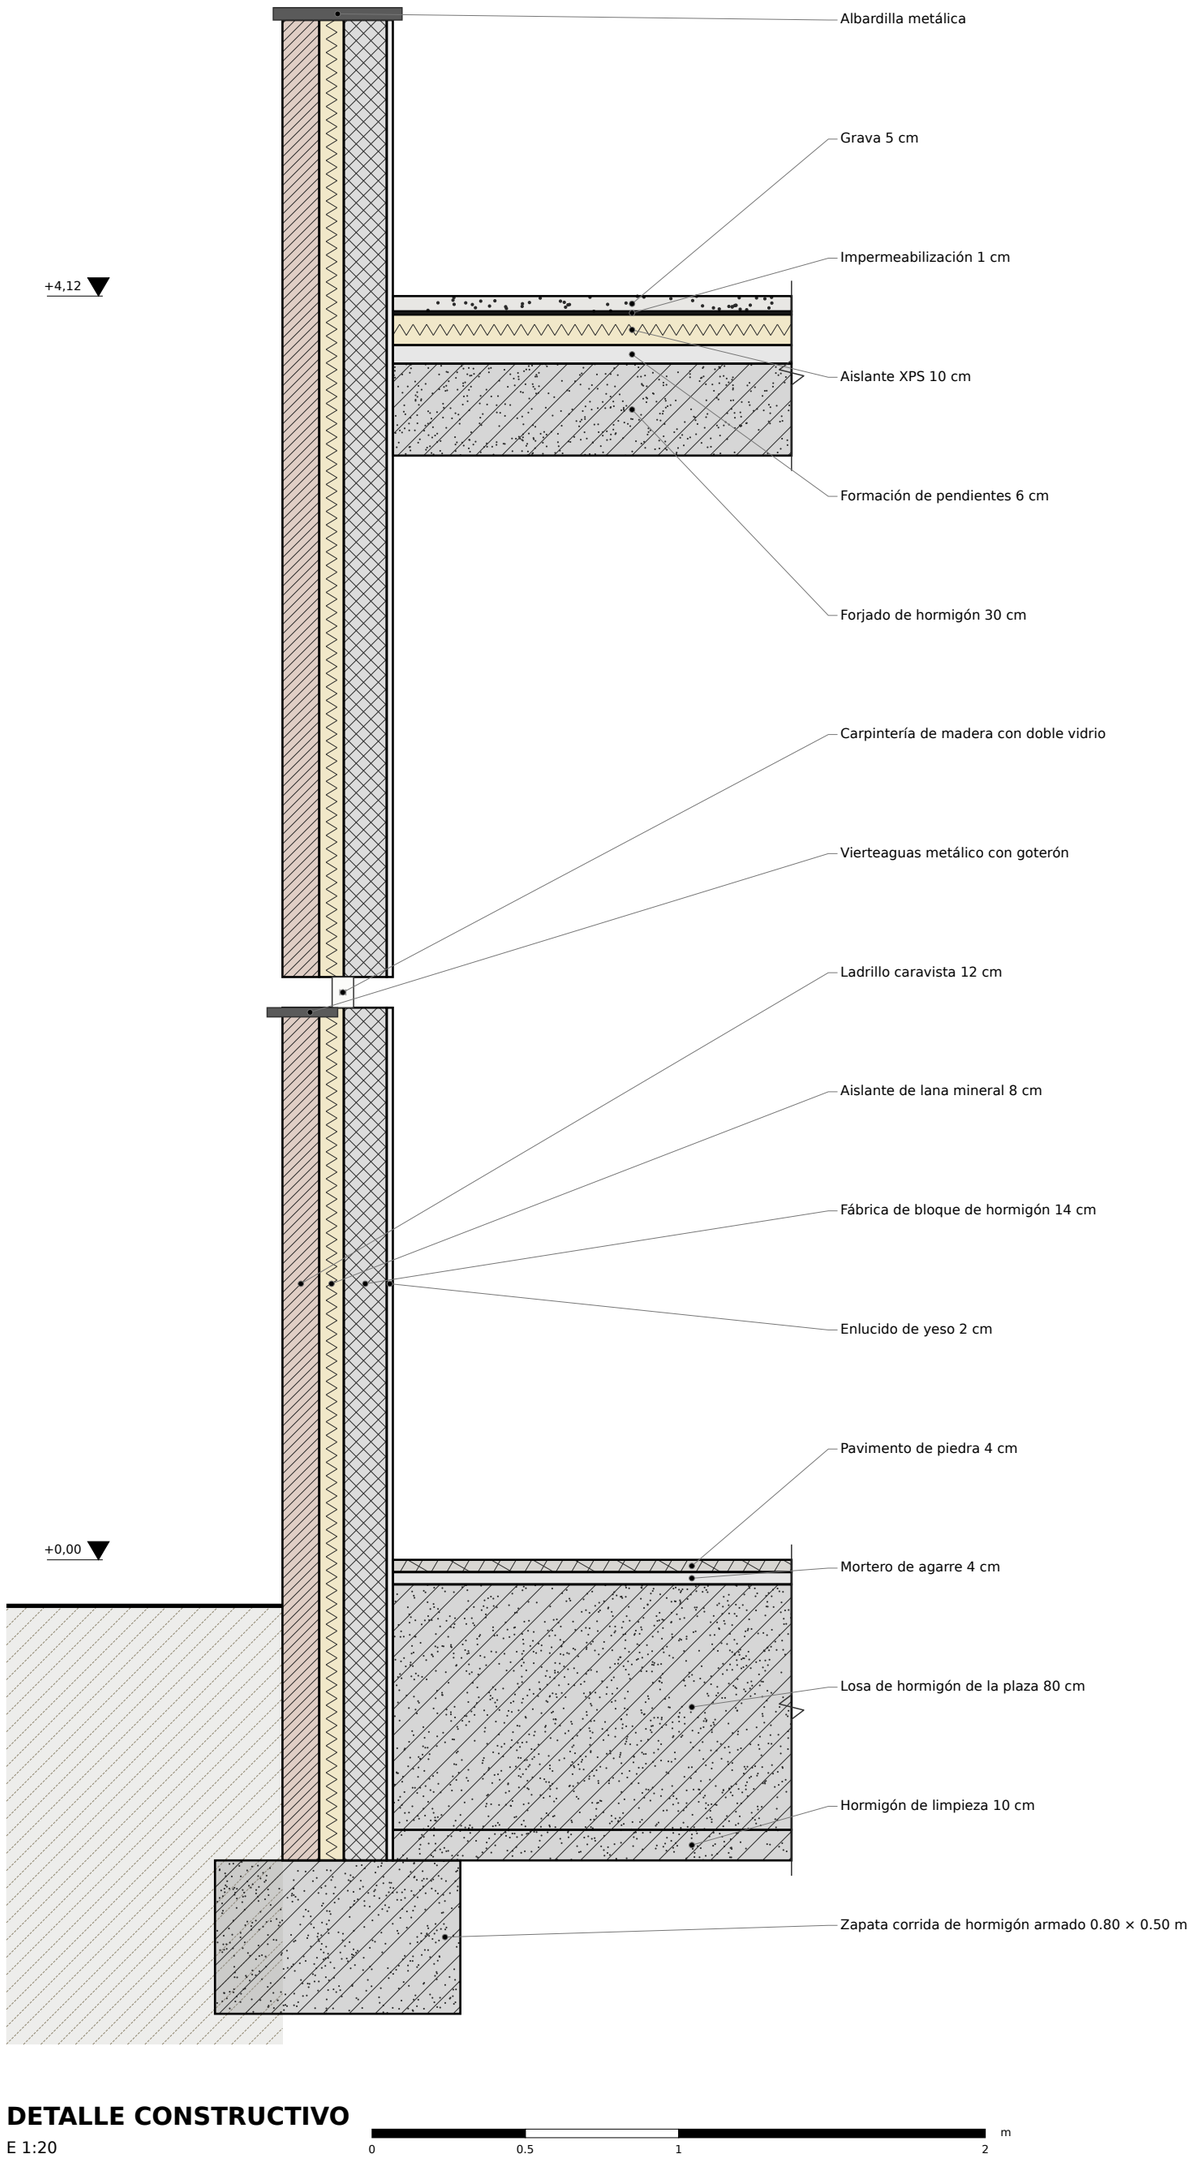


DETALLE CONSTRUCTIVO

E 1:20

CASO_020 · PROPUESTA A	E 1:20	**D01**
SECCIÓN CONSTRUCTIVA DE FACHADA DEL HOTEL	Anteproyecto	