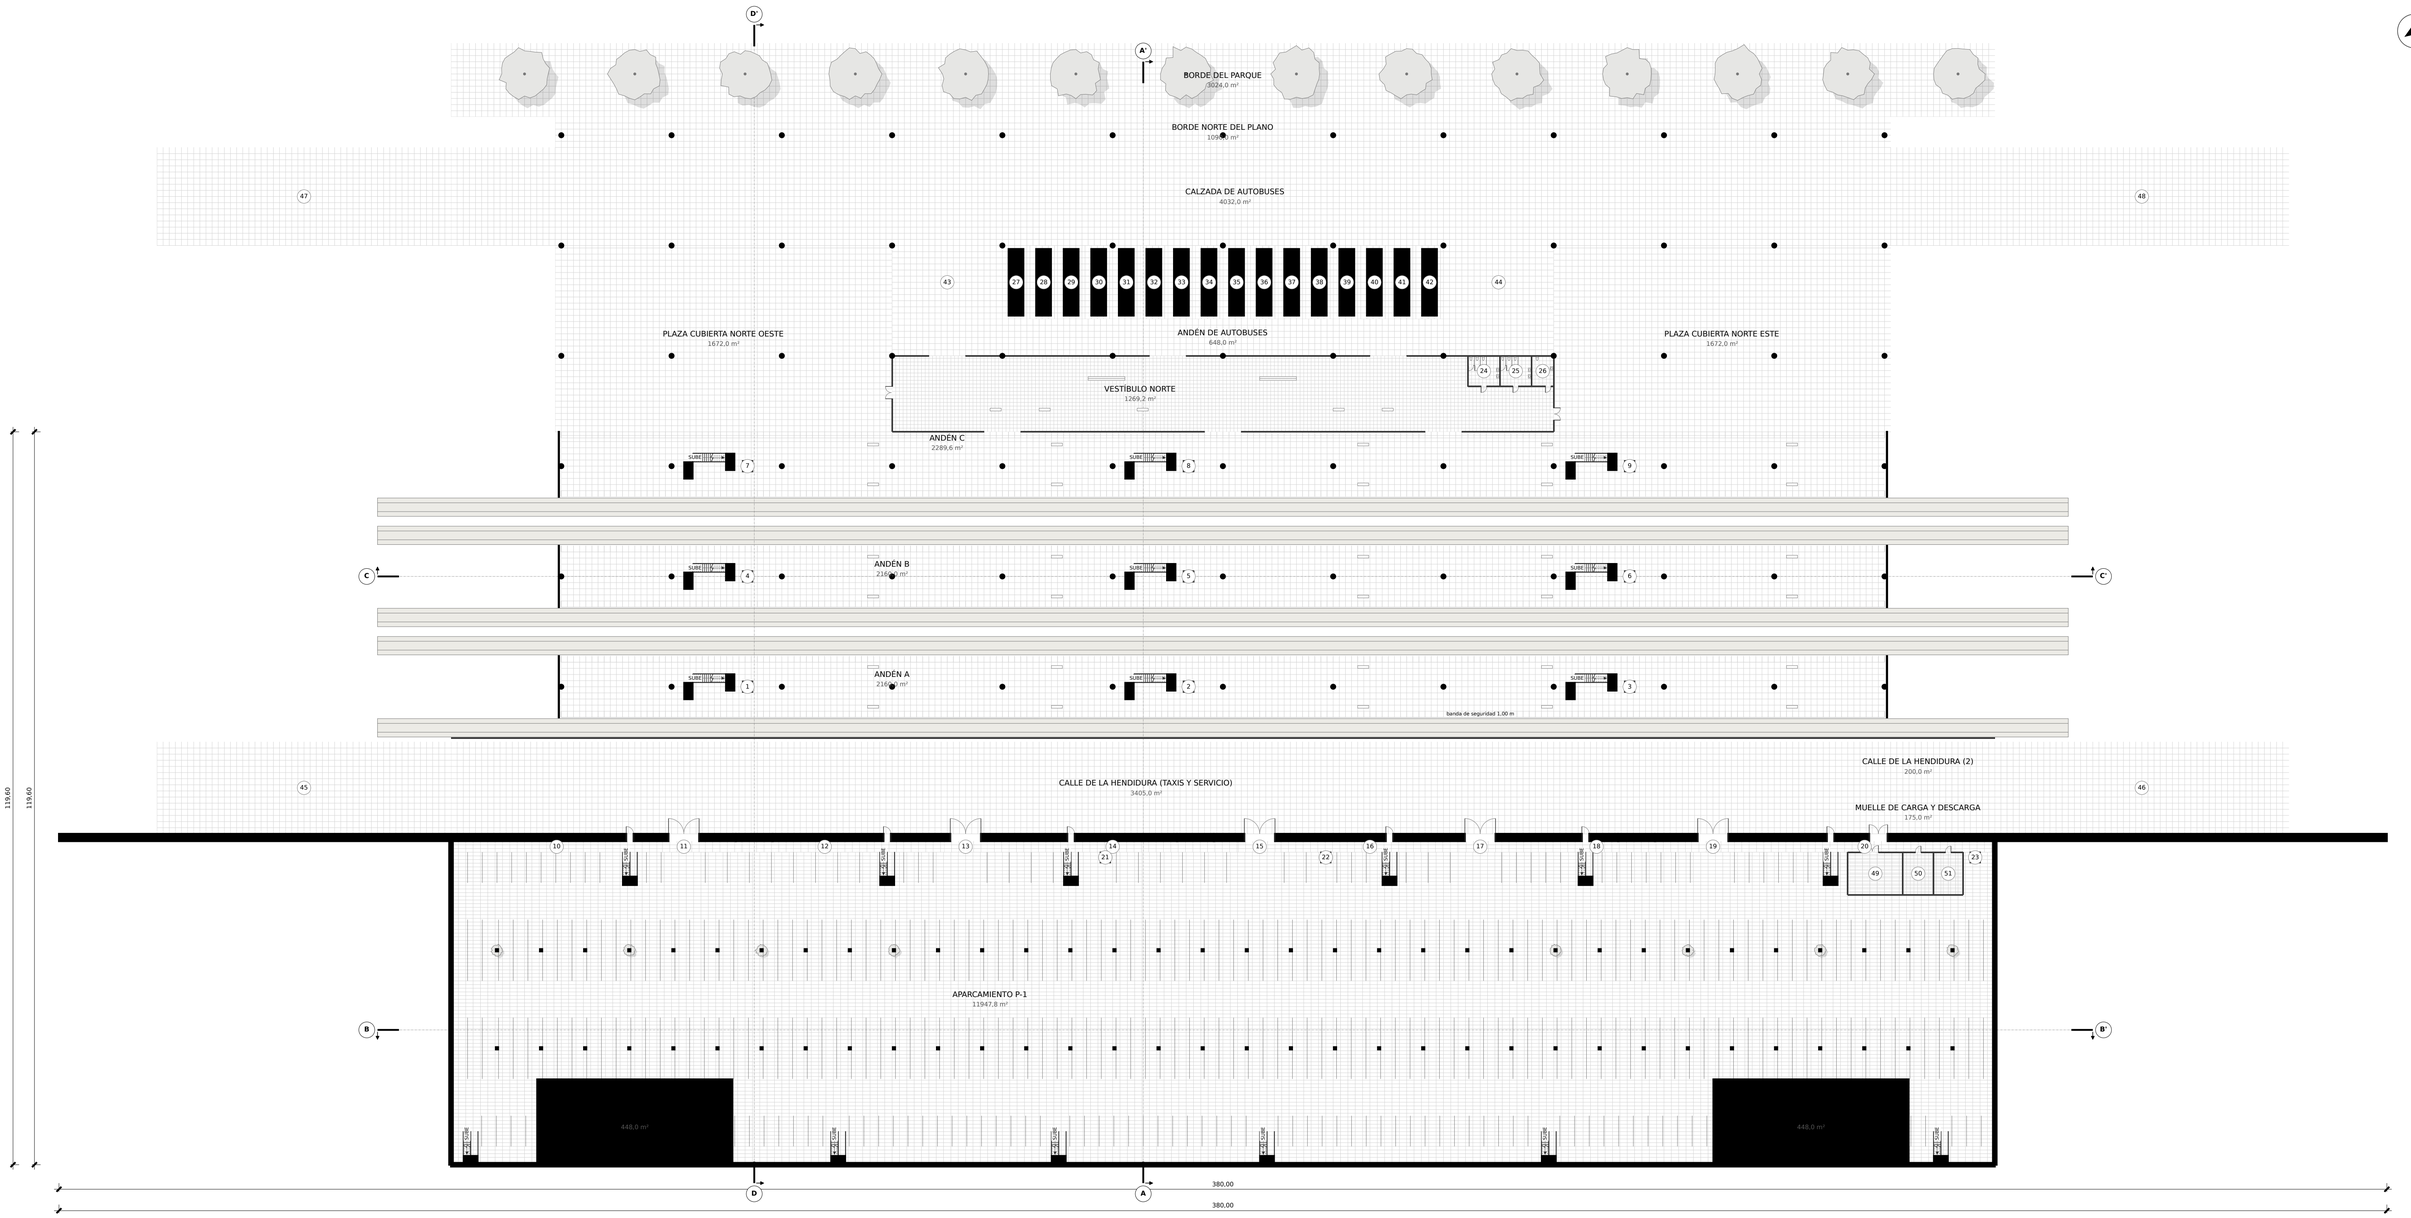


PLANTA BAJA +0,00

E 1:500

0 5 10 25 50 m

1 Ascensor · 2,7 m²
2 Ascensor · 2,7 m²
3 Ascensor · 2,7 m²
4 Ascensor · 2,7 m²
5 Ascensor · 2,7 m²
6 Ascensor · 2,7 m²
7 Ascensor · 2,7 m²
8 Ascensor · 2,7 m²
9 Ascensor · 2,7 m²
10 Pasillo peatonal norte P-1 (1) · 62,1 m²
11 Entrada de vehículos 1 · 12,6 m²
12 Pasillo peatonal norte P-1 (2) · 70,2 m²
13 Entrada de vehículos 2 · 12,6 m²
14 Pasillo peatonal norte P-1 (3) · 73,8 m²
15 Entrada de vehículos 3 · 12,6 m²
16 Pasillo peatonal norte P-1 (4) · 52,2 m²
17 Entrada de vehículos 4 · 12,6 m²
18 Pasillo peatonal norte P-1 (5) · 55,8 m²
19 Entrada de vehículos 5 · 12,6 m²
20 Pasillo peatonal norte P-1 (6) · 76,5 m²
21 Ascensor · 2,7 m²
22 Ascensor · 2,7 m²
23 Ascensor · 2,7 m²
24 Aseo mujeres · 26,0 m²
25 Aseo hombres · 26,0 m²
26 Aseo accesible · 18,0 m²
27 Dársena 1 · 54,0 m²
28 Dársena 2 · 54,0 m²
29 Dársena 3 · 54,0 m²
30 Dársena 4 · 54,0 m²
31 Dársena 5 · 54,0 m²
32 Dársena 6 · 54,0 m²
33 Dársena 7 · 54,0 m²
34 Dársena 8 · 54,0 m²
35 Dársena 9 · 54,0 m²
36 Dársena 10 · 54,0 m²
37 Dársena 11 · 54,0 m²
38 Dársena 12 · 54,0 m²
39 Dársena 13 · 54,0 m²
40 Dársena 14 · 54,0 m²
41 Dársena 15 · 54,0 m²
42 Dársena 16 · 54,0 m²
43 Plaza cubierta norte centro oeste · 216,0 m²
44 Plaza cubierta norte centro este · 216,0 m²
45 Calle de enlace viario oeste (entrada y salida de vehículos, 2 carriles de 3,0 m) · 720,0 m²
46 Calle de enlace viario este (entrada y salida de vehículos, 2 carriles de 3,0 m) · 720,0 m²
47 Calle de enlace de autobuses oeste (entrada, 2 carriles de 3,5 m) · 768,0 m²
48 Calle de enlace de autobuses este (salida, 2 carriles de 3,5 m) · 768,0 m²
49 Almacén de carga (comercio, restaurante y hotel) · 63,0 m²
50 Cuarto de instalaciones · 35,0 m²
51 Cuarto de basuras y jardinero · 33,6 m²

CASO_020 · PROPUESTA A	E 1:500	**P01**
PLANTA BAJA +0,00: VÍAS, ANDENES, AUTOBUSES Y APARCAMIENTO P-1	Anteproyecto	