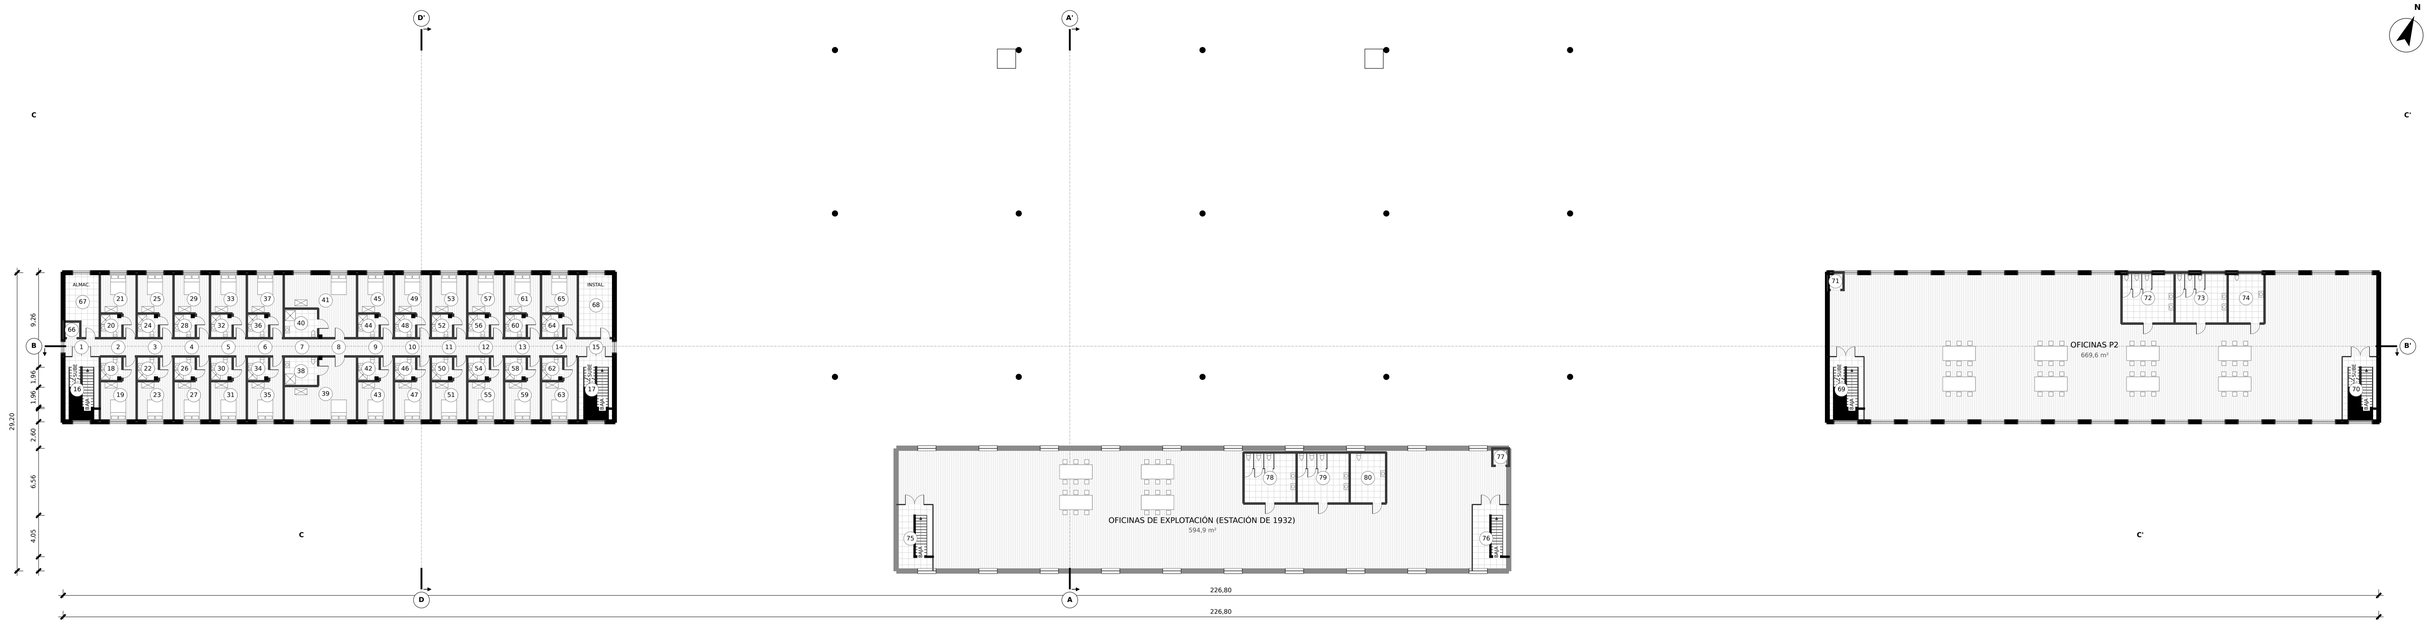
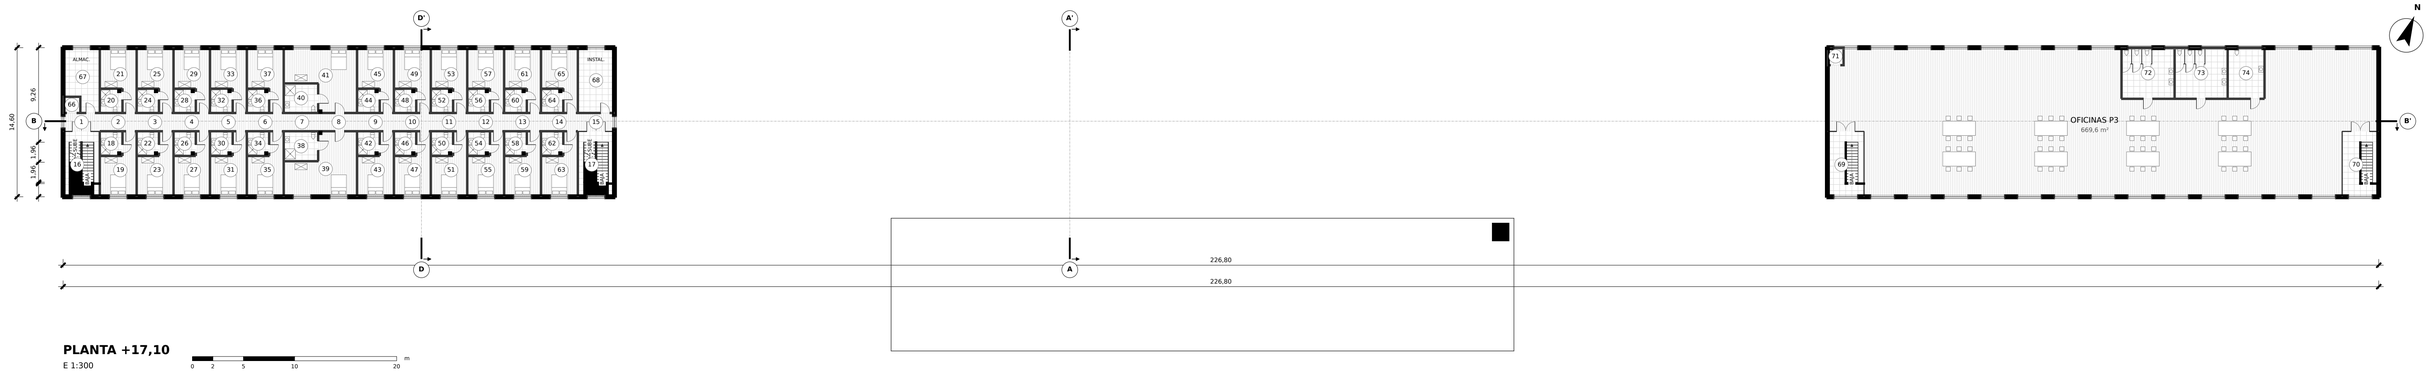


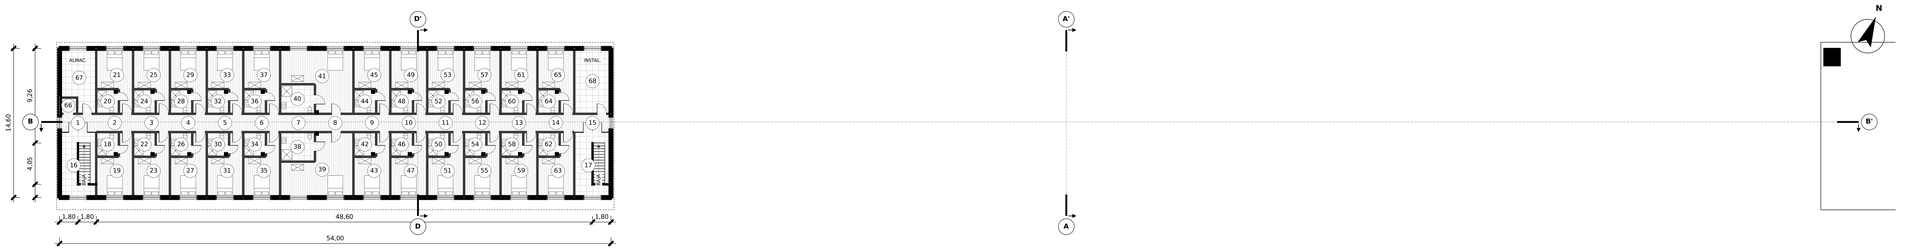

**PLANTA +13,50**
E 1:300

0 2 5 10 20 m




**PLANTA +17,10**
E 1:300

0 2 5 10 20 m




**PLANTA +20,70**
E 1:300

0 2 5 10 20 m

Obra nueva
Existente que se conserva
Existente que se demuele

**1** Pasillo del hotel 1 · 6,5 m²
**2** Pasillo del hotel 2 · 6,5 m²
**3** Pasillo del hotel 3 · 6,5 m²
**4** Pasillo del hotel 4 · 6,5 m²
**5** Pasillo del hotel 5 · 6,5 m²
**6** Pasillo del hotel 6 · 6,5 m²
**7** Pasillo del hotel 7 · 6,5 m²
**8** Pasillo del hotel 8 · 6,5 m²
**9** Pasillo del hotel 9 · 6,5 m²
**10** Pasillo del hotel 10 · 6,5 m²
**11** Pasillo del hotel 11 · 6,5 m²
**12** Pasillo del hotel 12 · 6,5 m²
**13** Pasillo del hotel 13 · 6,5 m²
**14** Pasillo del hotel 14 · 6,5 m²
**15** Pasillo del hotel 15 · 6,5 m²
**16** Escalera del hotel · 15,7 m²
**17** Escalera del hotel · 15,8 m²
**18** Baño 201 · 5,3 m²
**19** Habitación 201 · 17,8 m²
**20** Baño 221 · 5,3 m²
**21** Habitación 221 · 17,8 m²
**22** Baño 202 · 5,3 m²
**23** Habitación 202 · 17,8 m²
**24** Baño 222 · 5,3 m²
**25** Habitación 222 · 17,8 m²
**26** Baño 203 · 5,3 m²
**27** Habitación 203 · 17,8 m²
**28** Baño 223 · 5,3 m²
**29** Habitación 223 · 17,8 m²
**30** Baño 204 · 5,3 m²
**31** Habitación 204 · 17,8 m²
**32** Baño 224 · 5,3 m²
**33** Habitación 224 · 17,8 m²
**34** Baño 205 · 5,3 m²
**35** Habitación 205 · 17,8 m²
**36** Baño 225 · 5,3 m²
**37** Habitación 225 · 17,8 m²
**38** Habitación accesible 206 · 9,9 m²
**39** Habitación accesible 206 · 36,2 m²
**40** Baño accesible 226 · 9,9 m²
**41** Habitación accesible 226 · 36,2 m²
**42** Baño 208 · 5,3 m²
**43** Habitación 208 · 17,8 m²
**44** Baño 228 · 5,3 m²
**45** Habitación 228 · 17,8 m²
**46** Baño 209 · 5,3 m²
**47** Habitación 209 · 17,8 m²
**48** Baño 229 · 5,3 m²
**49** Habitación 229 · 17,8 m²
**50** Baño 210 · 5,3 m²
**51** Habitación 210 · 17,8 m²
**52** Baño 230 · 5,3 m²
**53** Habitación 230 · 17,8 m²
**54** Baño 211 · 5,3 m²
**55** Habitación 211 · 17,8 m²
**56** Baño 231 · 5,3 m²
**57** Habitación 231 · 17,8 m²

**CASO_020 · PROPUESTA A**

PLANTAS +13,50, +17,10 Y +20,70

E 1:300

Anteproyecto

**P04**